


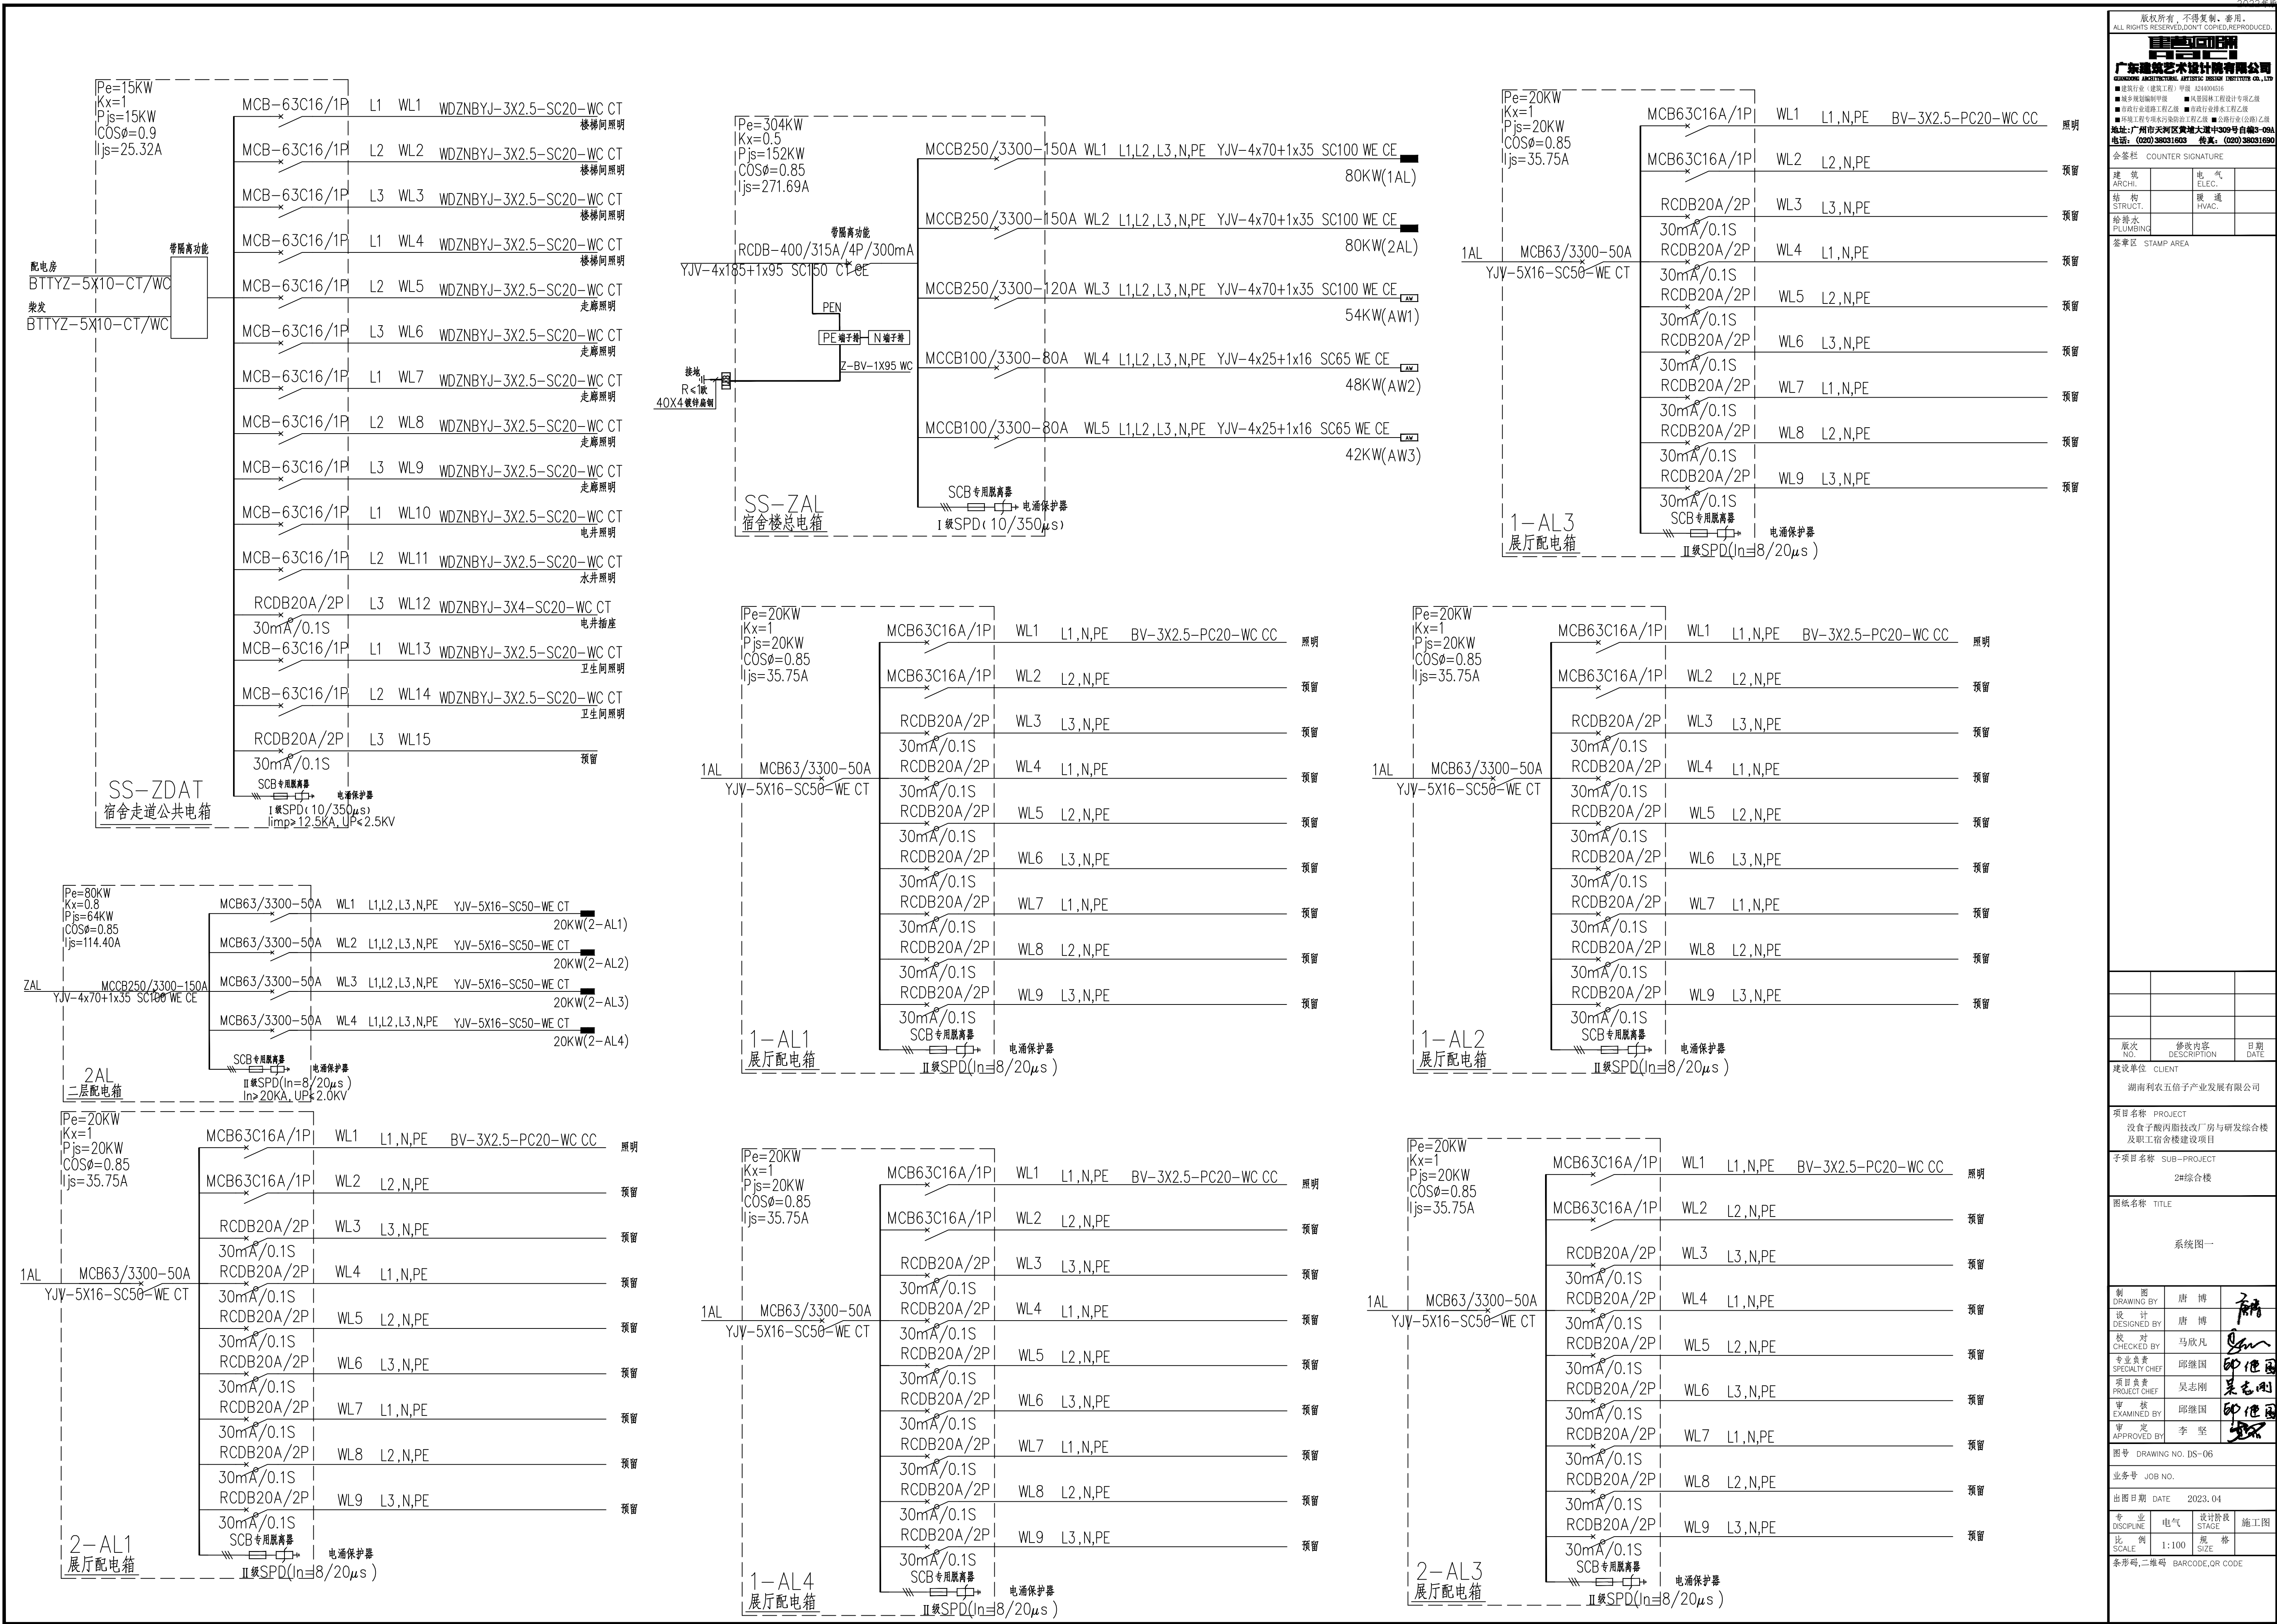

Copyright notice and company information for Guangdong Architectural Design Institute Co., Ltd.

版权所有，不得复制、套用。
ALL RIGHTS RESERVED, DON'T COPIED, REPRODUCED.

广东建筑艺术设计院有限公司
GUANGDONG ARCHITECTURAL ARTIST DESIGN INSTITUTE CO., LTD.

■ 建筑行业（建筑工程）甲级（含增项）
■ 城乡规划编制甲级
■ 风景园林工程设计专项乙级
■ 市政公用行业设计专项乙级
■ 环境工程专项设计（给排水工程、暖通工程、电气专业）乙级
■ 环境工程专项设计（暖通工程、给排水工程、电气专业）乙级

地址：广州市天河区黄埔大道中309号自编3-05A
电话：(020) 38021622 传真：(020) 38021620

会签栏 COUNTER SIGNATURE

建筑	电气	暖通
ARCHT.	ELEC.	HVAC
STRUCT.		
PLUMBING		

签字区 STAMP AREA

版次	修改内容	日期
NO.	DESCRIPTION	DATE

建设单位 CLIENT
湖南利农五倍子产业发展有限公司

项目名称 PROJECT
没食子酸丙脂技改厂房与研发综合楼及职工宿舍楼建设项目

子项目名称 SUB-PROJECT
2#综合楼

图纸名称 TITLE
系统图一

制图 DRAWING BY 唐博
设计 DESIGNED BY 唐博
校对 CHECKED BY 马欣凡
专业负责 SPECIALLY CHIEF 邱继国
项目负责人 PROJECT CHIEF 吴志刚
审核 EXAMINED BY 邱继国
审定 APPROVED BY 李坚

图号 DRAWING NO. DS-06

业务号 JOB NO.

出图日期 DATE 2023.04

专业 DISCIPLINE 电气 设计阶段 STAGE 施工图
比例 SCALE 1:100 规格 SIZE
条形码、二维码 BARCODE, QR CODE