


照明计算表																						
房间参数							利用系数表参数		其他计算参数								计算结果					
序号	房间名称	房间长 (m)	房间宽 (m)	面积 (m²)	灯安装高度 (m)	工作面高度 (m)	数据来源	利用系数值	光源种类	单灯光源数	光源功率 (W)	光通量(lm)	总光通量 (lm)	镇流器功率 (W)	房间类别	维护系数	要求照度值 (lx)	功率密度规范值 (W/m²)	灯具数	总功率 (W)	计算照度值 (lx)	功率密度计算值 (W/m²)
1	展厅	61.40(周长)	170.22	3.90	0.75	《照明设计手册(第三版)》	0.65	T8标准直管荧光灯	2	64	2975	5950	9	一般展厅	0.80	200.00	8.00	13	949	237.75	5.58	
2	展厅	60.06(周长)	178.22	3.90	0.75	《照明设计手册(第三版)》	0.66	T8标准直管荧光灯	2	64	2975	5950	9	一般展厅	0.80	200.00	8.00	12	876	212.18	4.92	
3	展厅	35.80(周长)	77.38	3.90	0.75	《照明设计手册(第三版)》	0.62	T8标准直管荧光灯	2	64	2975	5950	9	一般展厅	0.80	200.00	8.00	6	438	227.36	5.66	
4	展厅	33.00(周长)	67.16	3.90	0.75	《照明设计手册(第三版)》	0.61	T8标准直管荧光灯	2	100	4000	8000	12	一般展厅	0.80	200.00	8.00	4	448	230.99	6.67	

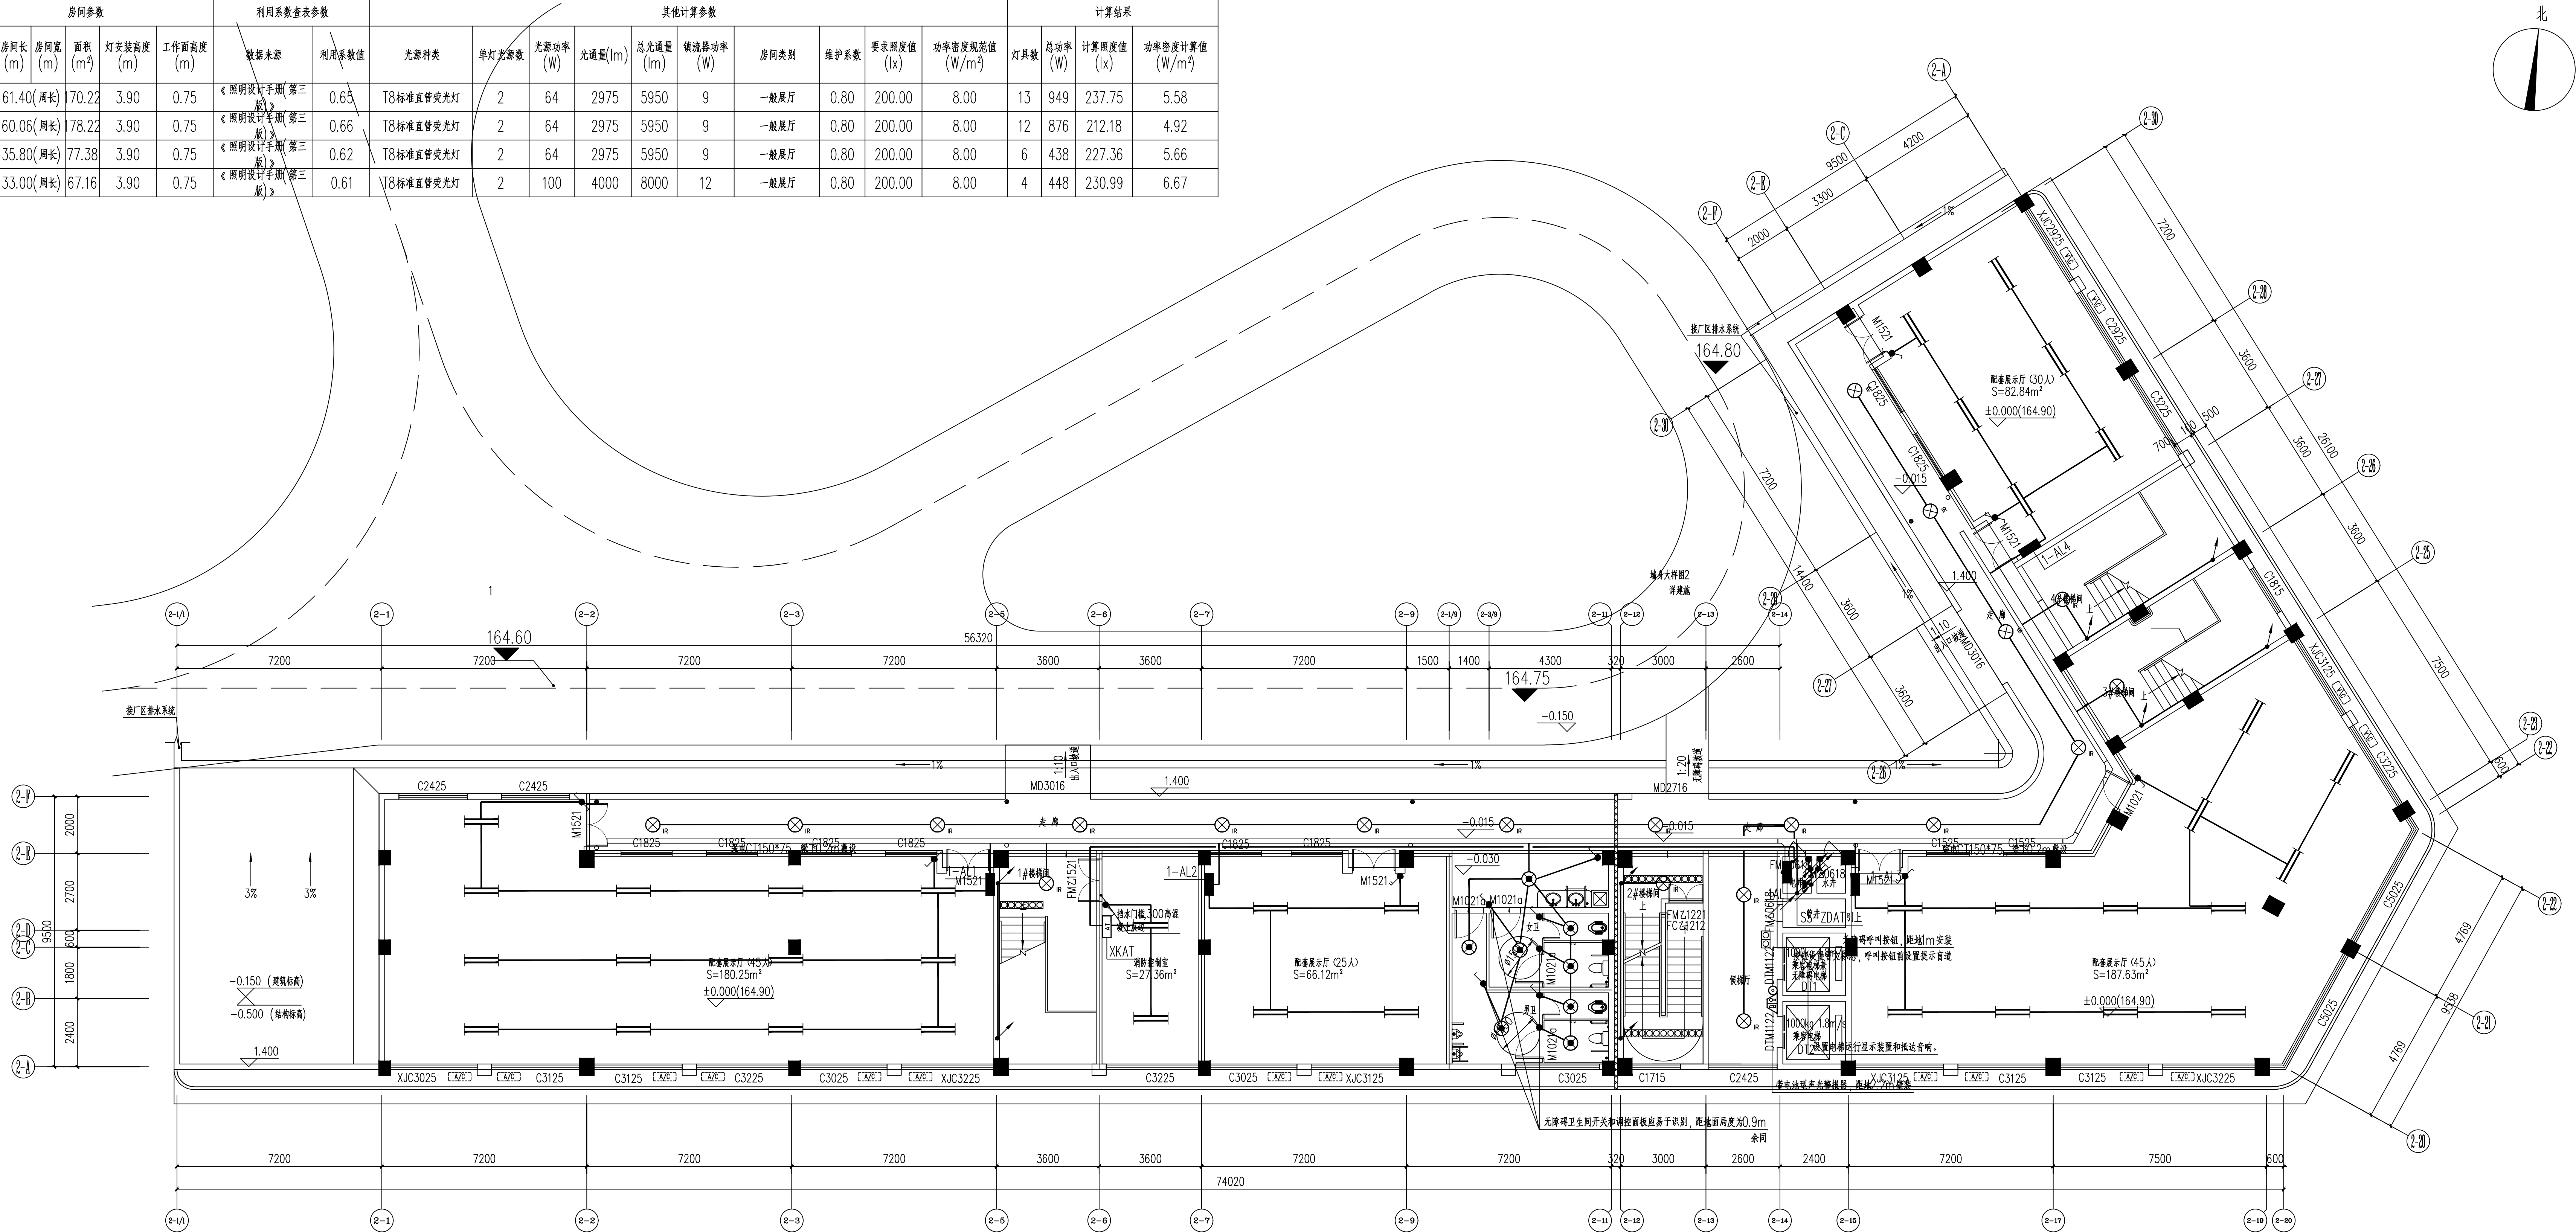

2#综合楼一层强电平面图 1:100

2022年版

版权所有，不得复制、套用。
ALL RIGHTS RESERVED.DONT COPIED,REPRODUCED.

广东建筑设计研究院有限公司

GUANGDONG ARCHITECTURAL RESEARCH INSTITUTE CO.,LTD

■建筑行业(建筑工程)甲级 AS44061616
■城乡规划编制甲级 ■风景园林工程设计专项乙级
■市政公用工程设计乙级 ■室内环境设计乙级
■环境工程专项污染防治工程乙级 ■公路行业(公路)乙级

地址:广州市天河区黄埔大道中309号自编3-09A
电话: (020)28831603 传真: (020)28831690

会签栏 COUNTER SIGNATURE

建 筑 ARCHI.	电 气 ELEC.
结 构 STRUCT.	暖 通 HVAC.
给 排 水 PLUMBING	

签字区 STAMP AREA

版次 NO.	修改内容 DESCRIPTION	日期 DATE
建设单位 CLIENT	湖南利农五倍子产业发展有限公司	
项目名称 PROJECT	没食子酸内酯技改厂房与研发综合楼 及职工宿舍楼建设项目	
子项目名称 SUB-PROJECT	2#综合楼	
图纸名称 TITLE	一层强电平面图	
制 图 DRAWING BY	唐 博	2023.04
设 计 DESIGNED BY	唐 博	
校 对 CHECKED BY	马欣凡	
专业负责 SPECIALTY CHIEF	邱继国	
项目负责人 PROJECT CHIEF	吴志刚	
审 核 EXAMINED BY	邱继国	
审 定 APPROVED BY	李 坚	
图号 DRAWING NO.	DS-09	
业务号 JOB NO.		
出图日期 DATE	2023.04	
专 业 DISCIPLINE	电气	设计阶段 STAGE
比 例 SCALE	1:100	施 工 图
条形码、二维码 BARCODE,QR CODE		