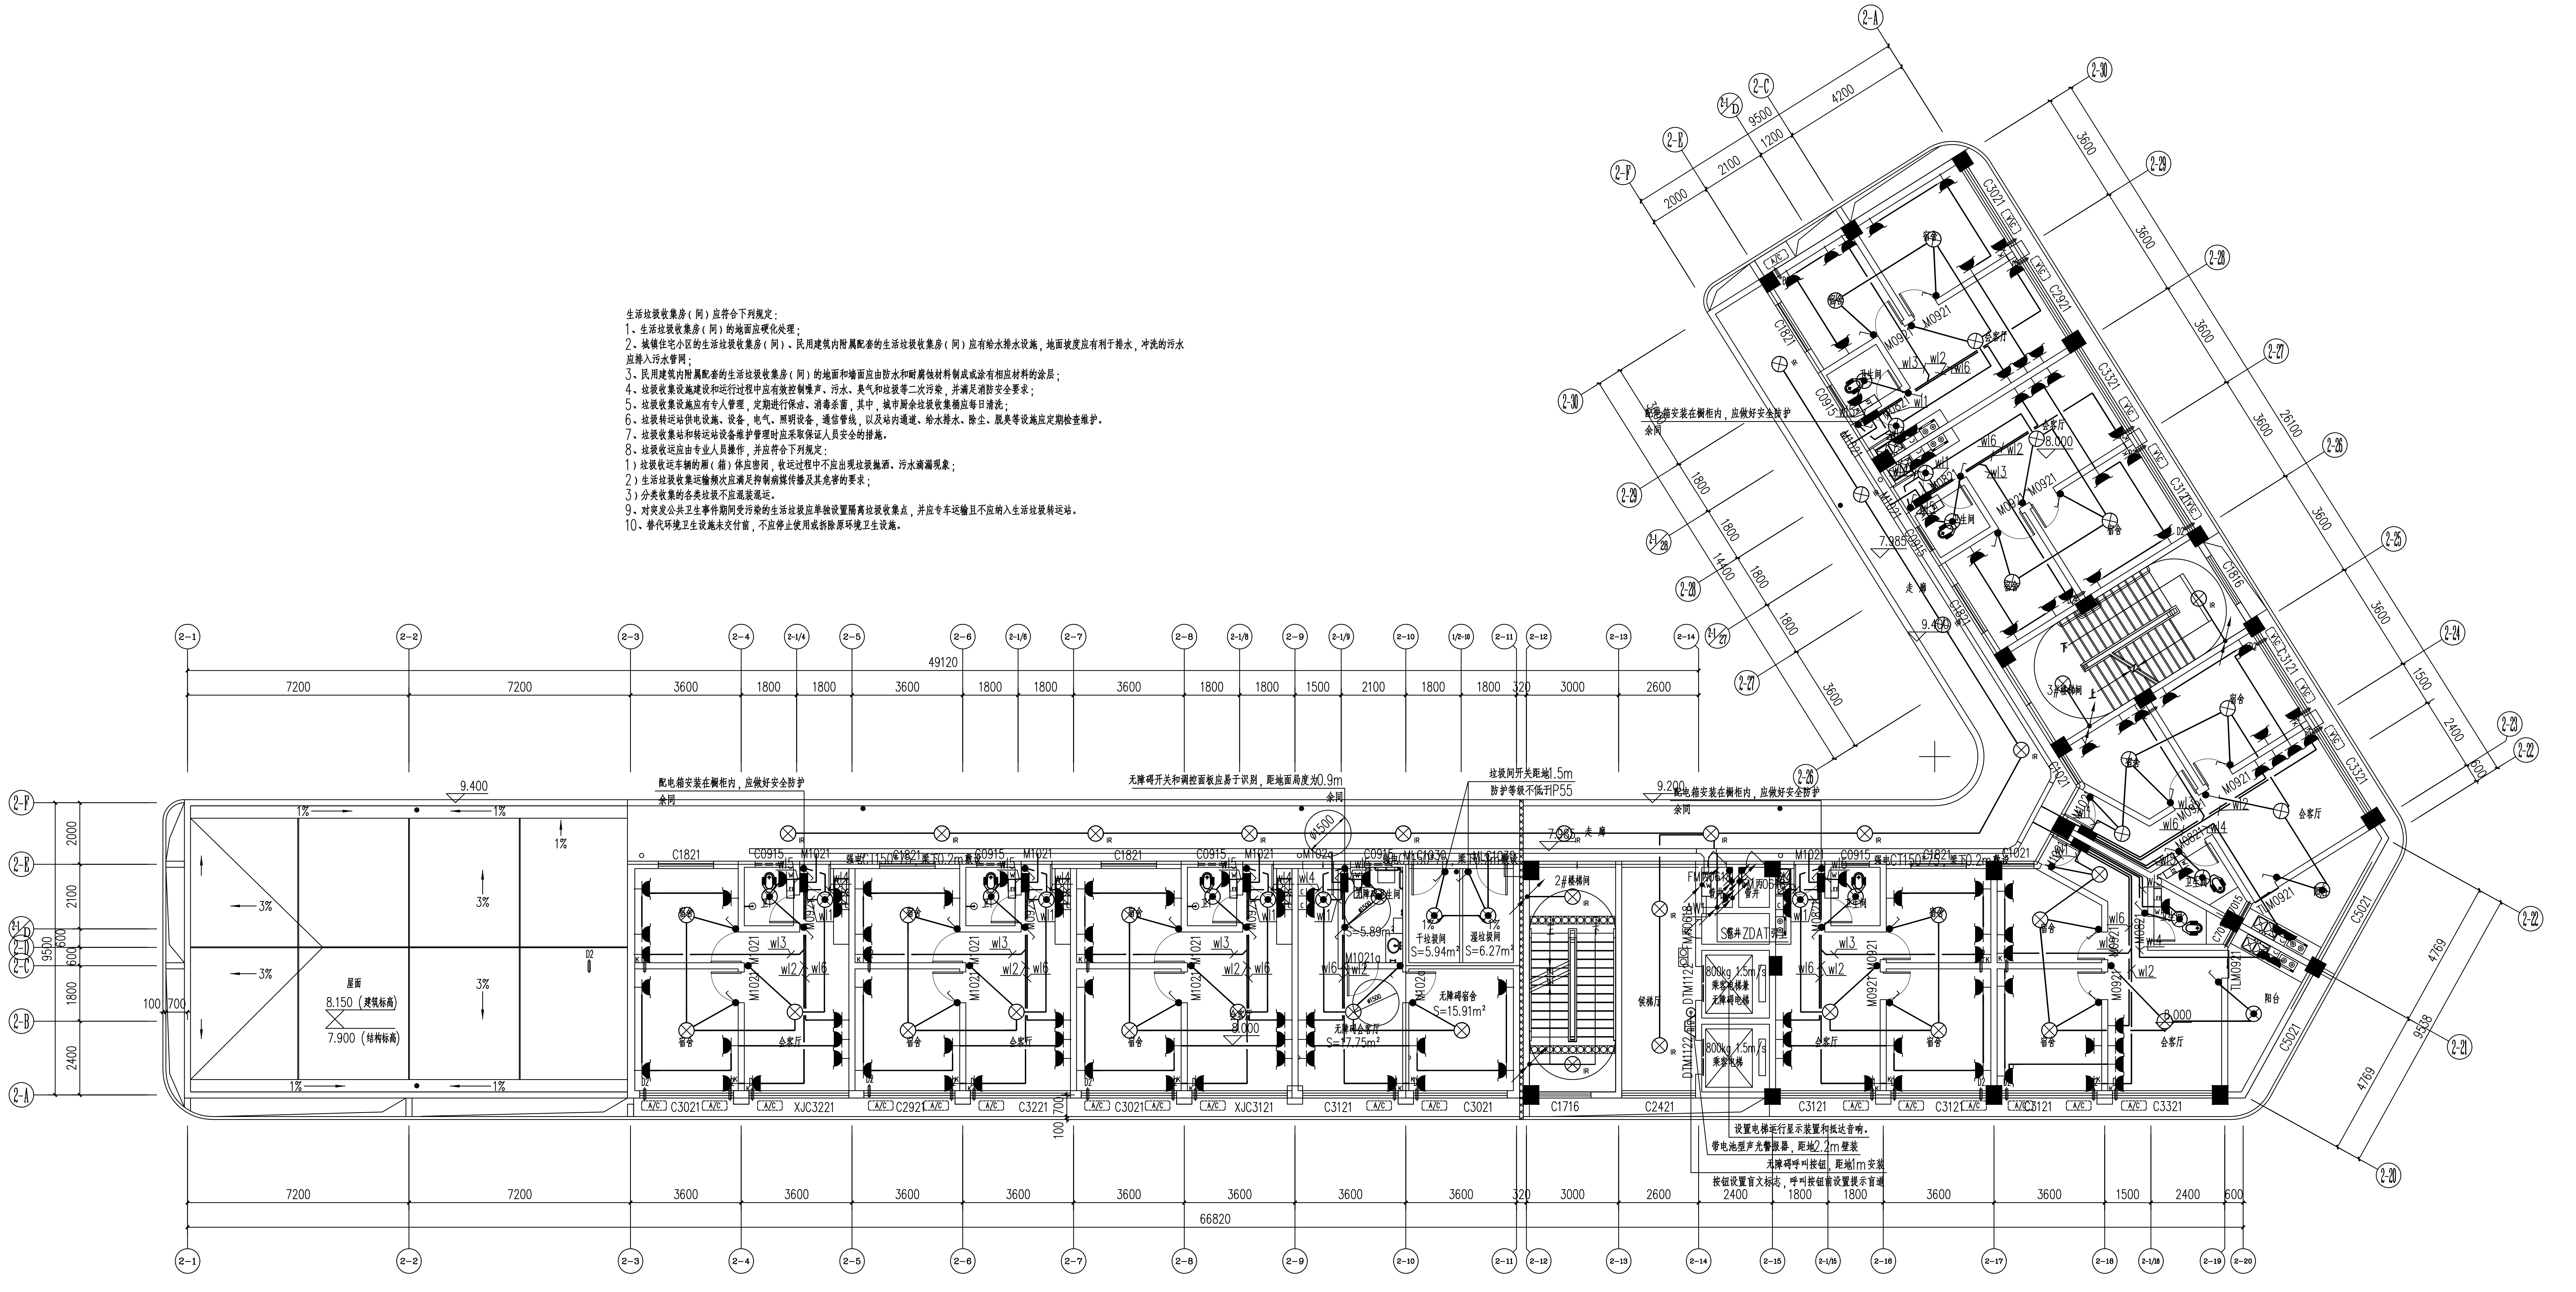

生活垃圾收集房（间）应符合下列规定：

1、生活垃圾收集房（间）的地面应硬化处理；

2、城镇住宅小区的生活垃圾收集房（间）、民用建筑内附属配套的生活垃圾收集房（间）应有给水排水设施，地面坡度应有利于排水，冲洗的污水应排入污水管网；

3、民用建筑内附属配套的生活垃圾收集房（间）的地面和墙面应由防水和耐腐蚀材料制成或涂有相应材料的涂层；

4、垃圾收集设施建设和运行过程中应有效控制噪声、污水、臭气和垃圾等二次污染，并满足消防安全要求；

5、垃圾收集设施应有专人管理，定期进行保洁、消毒杀菌，其中，城市厨余垃圾收集桶应每日清洗；

6、垃圾转运站供电设施、设备，电气、照明设备，通信管线，以及站内通道、给水排水、除尘、脱臭等设施应定期检查维护。

7、垃圾收集站和转运站设备维护管理时应采取保证人员安全的措施。

8、垃圾收运应由专业人员操作，并应符合下列规定：

1）垃圾收运车辆的厢（箱）体应密闭，收运过程中不应出现垃圾抛洒、污水滴漏现象；

2）生活垃圾收集运输频次应满足抑制病媒传播及其危害的要求；

3）分类收集的各类垃圾不应混装混运。

9、对突发公共卫生事件期间受污染的生活垃圾应单独设置隔离垃圾收集点，并应专车运输且不应纳入生活垃圾转运站。

10、替代环境卫生设施未交付前，不应停止使用或拆除原环境卫生设施。

2#综合楼三层强电平面图 1:100

2022年版

版权所有，不得复制、套用。
ALL RIGHTS RESERVED,DON'T COPIED,REPRODUCED.

广东建筑艺术设计院有限公司
GUANGDONG ARCHITECTURAL ARTISTIC DESIGN INSTITUTE CO.,LTD
■建筑行业（建筑工程）甲级 A244004516
■城乡规划编制甲级 ■风景园林工程设计专项乙级
■市政行业道路工程乙级 ■市政行业排水工程乙级
■环境工程专项水污染防治工程乙级 ■公路行业(公路)乙级
地址:广州市天河区黄埔大道中309号自编3-09A
电话：(020)38031603 传真：(020)38031690

会签栏 COUNTER SIGNATURE

建筑 ARCHI.		电气 ELEC.	
结构 STRUCT.		暖通 HVAC.	
给排水 PLUMBING			

签章区 STAMP AREA

版次 NO.	修改内容 DESCRIPTION	日期 DATE

建设单位 CLIENT
湖南利农五倍子产业发展有限公司

项目名称 PROJECT
没食子酸丙脂技改厂房与研发综合楼
及职工宿舍楼建设项目

子项目名称 SUB-PROJECT
2#综合楼

图纸名称 TITLE
三层强电平面图

制图 DRAWING BY	唐博	唐博
设计 DESIGNED BY	唐博	
校对 CHECKED BY	马欣凡	
专业负责 SPECIALTY CHIEF	邱继国	邱继国
项目负责 PROJECT CHIEF	吴志刚	吴志刚
审核 EXAMINED BY	邱继国	邱继国
审定 APPROVED BY	李坚	

图号 DRAWING NO. DS-11

业务号 JOB NO.

出图日期 DATE 2023.04

专业 DISCIPLINE	电气	设计阶段 STAGE	施工图
比例 SCALE	1:100	规格 SIZE	

条形码,二维码 BARCODE,QR CODE