


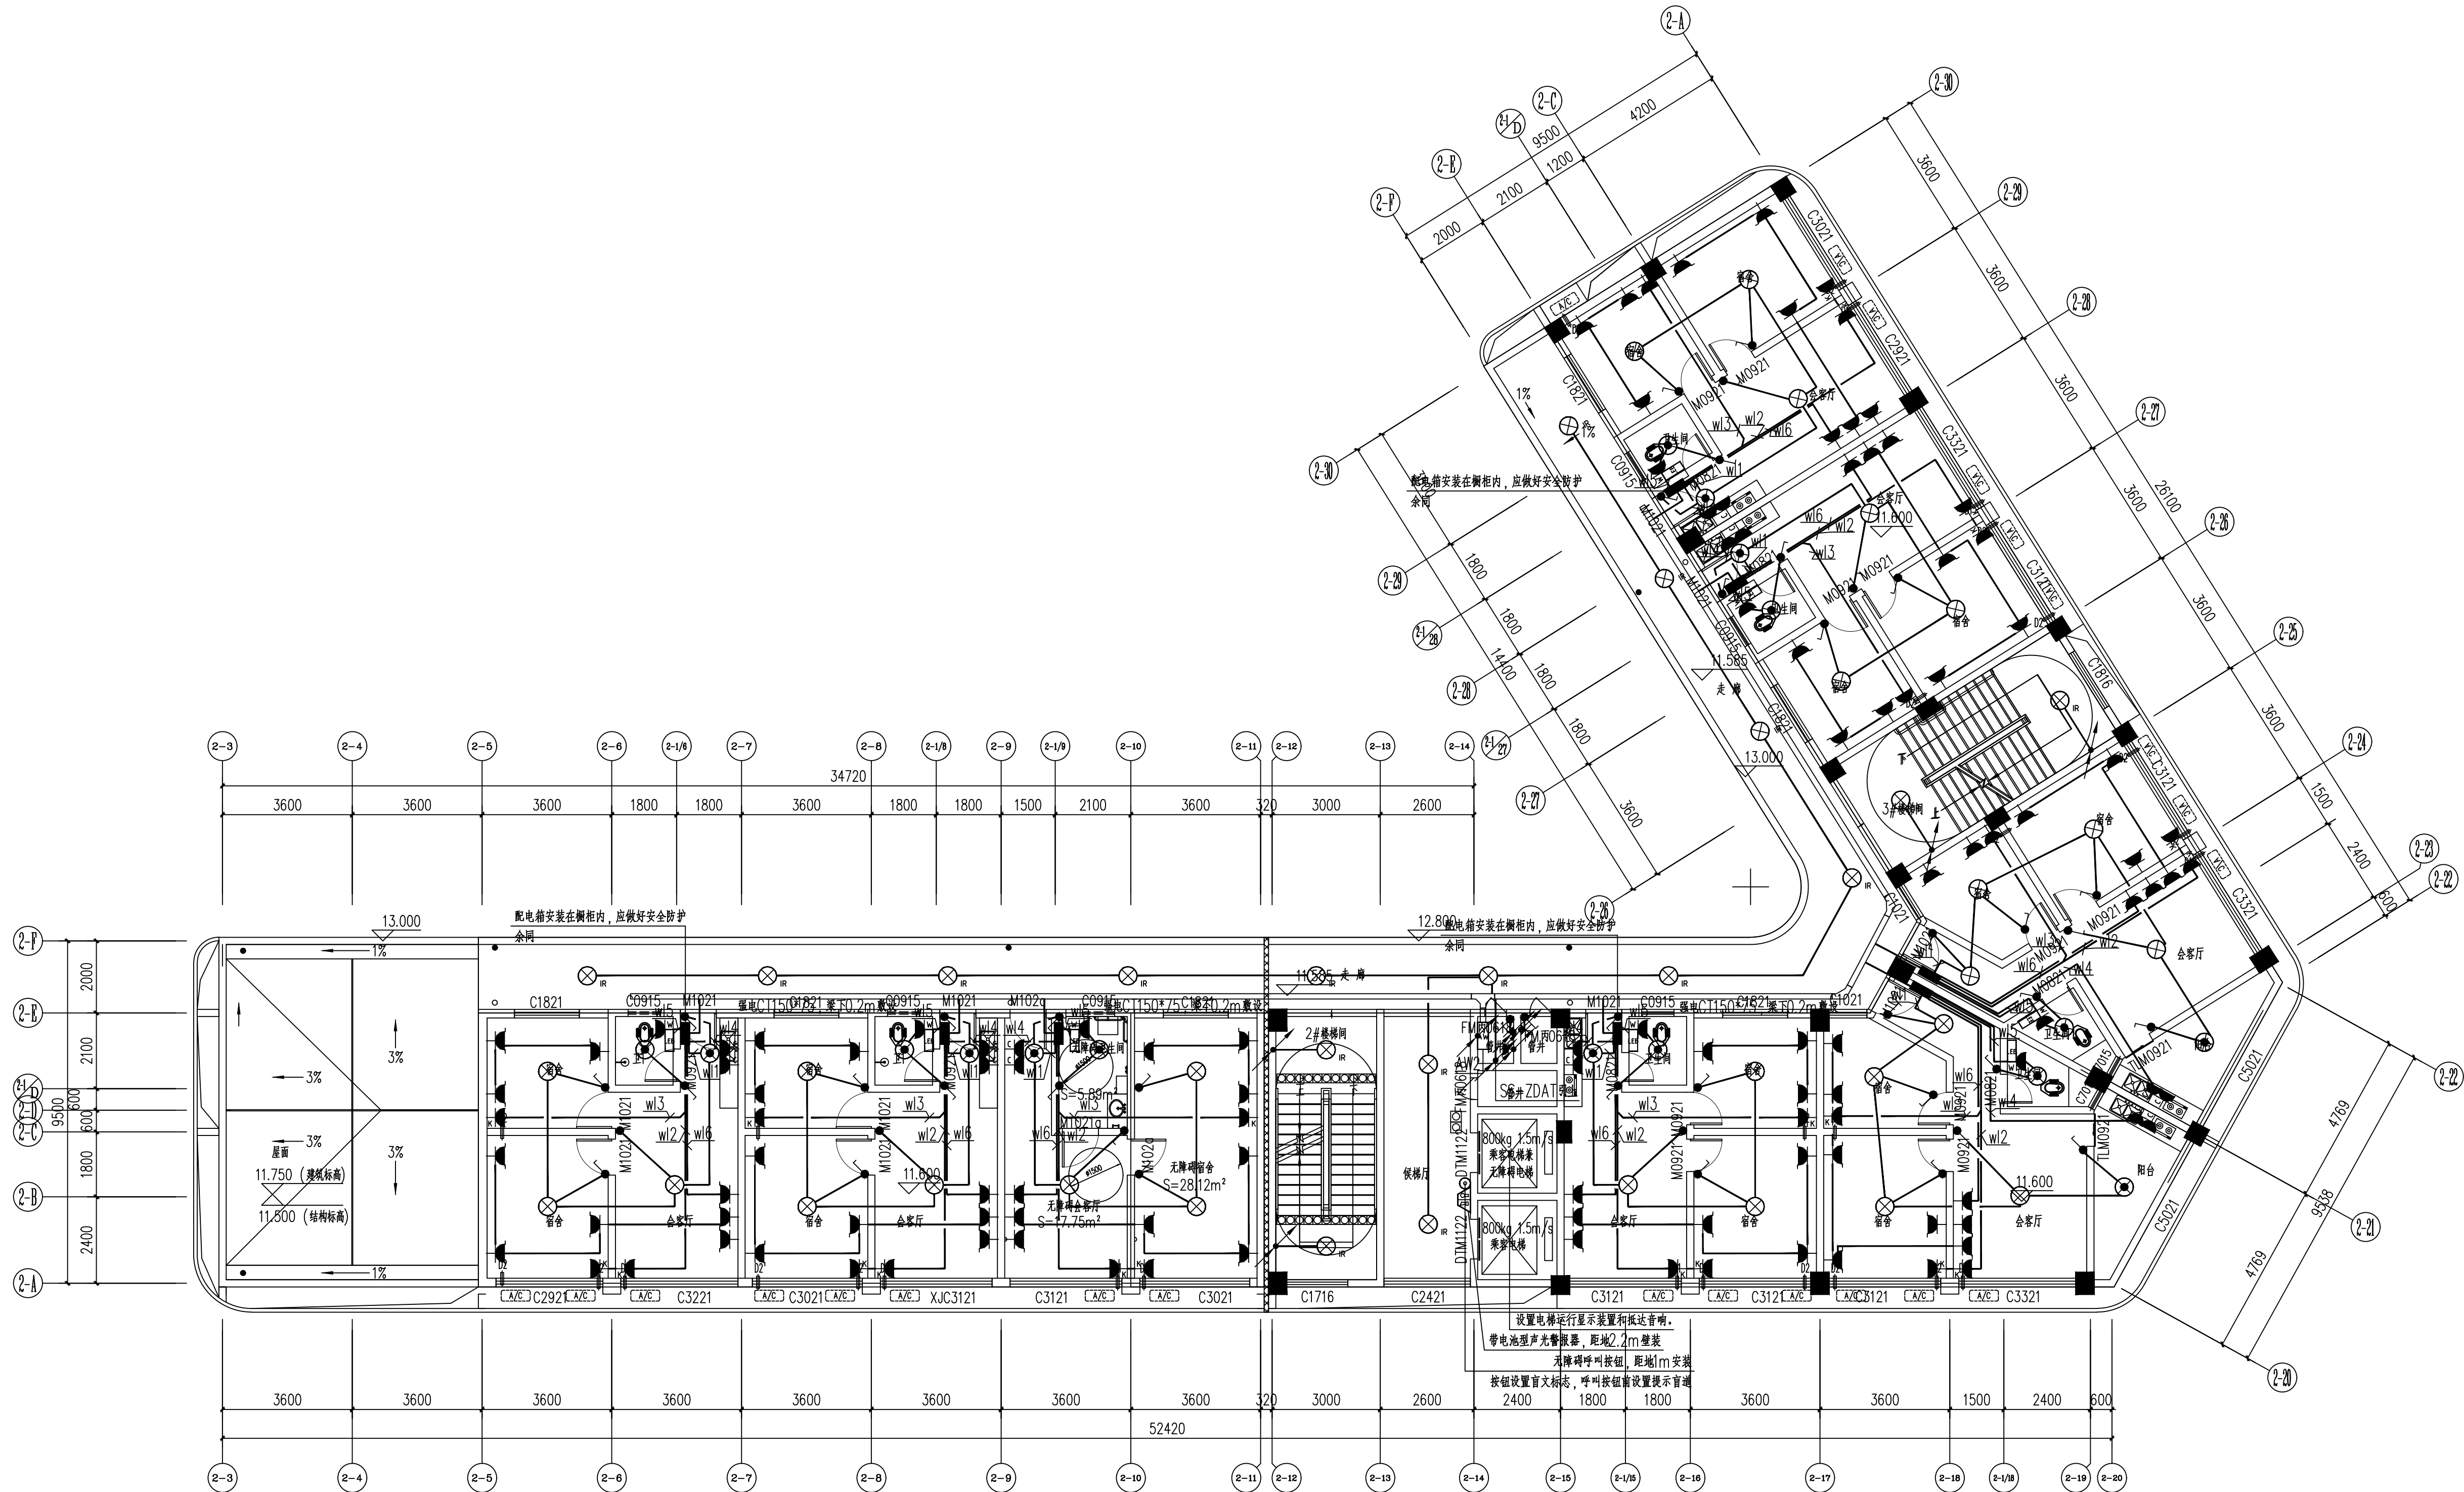

2#综合楼四层强电平面图 1:100

图次 NO.

修改内容 DESCRIPTION

日期 DATE

建设单位 CLIENT

湖南利农五倍子产业发展有限公司

项目名称 PROJECT

设食子酸内脂技改厂房与研发综合楼

及职工宿舍楼建设项目

子项目名称 SUB-PROJECT

2#综合楼

图纸名称 TITLE

四层强电平面图

制图 DRAWING BY

设计 DESIGNED BY

校对 CHECKED BY

专业负责 SPECIALTY CHIEF

项目负责 PROJECT CHIEF

审核 EXAMINED BY

审定 APPROVED BY

图号 DRAWING NO. DS-12

业务号 JOB NO.

出图日期 DATE 2023.04

专业 DISCIPLINE 电气

设计阶段 STAGE 施工图

比例 SCALE 1:100

图例 SIZE 图 格

条形码、二维码 BARCODE, QR CODE