


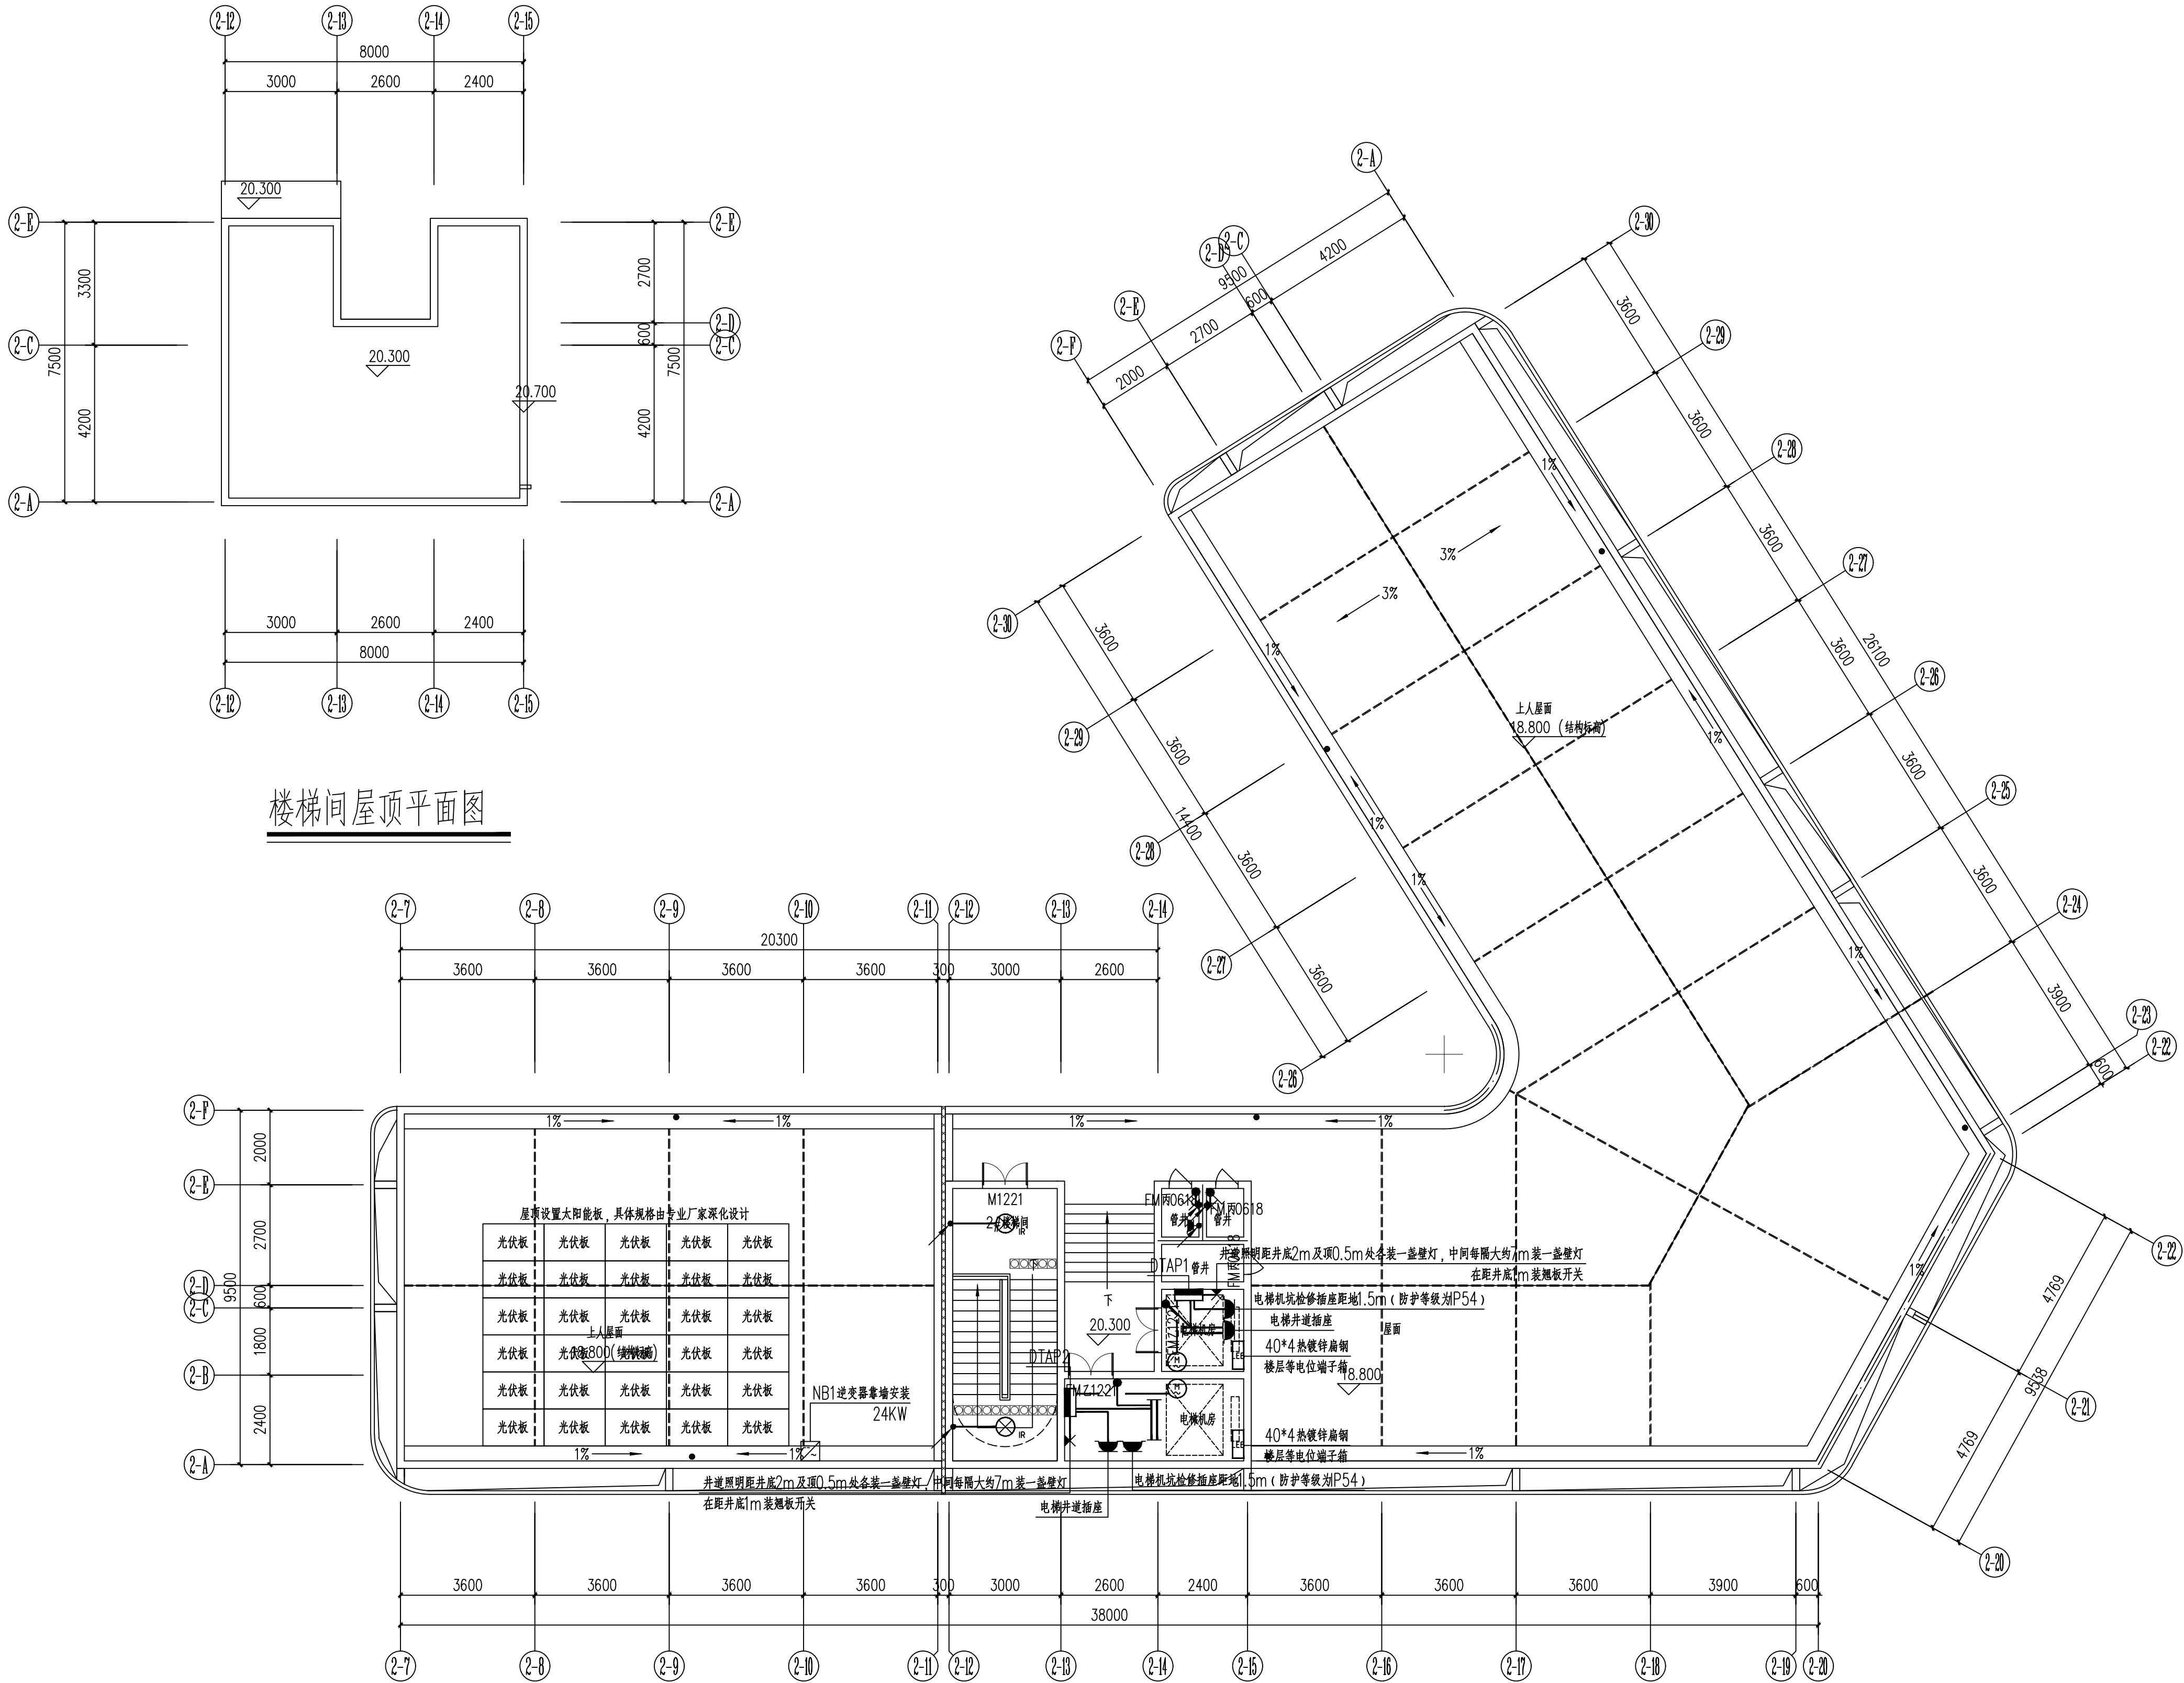

2#综合楼屋顶强电平面图 1:100

版次 NO. 修改内容 DESCRIPTION 日期 DATE

建设单位 CLIENT

湖南利农五倍子产业发展有限公司

项目名称 PROJECT

设食子酸内脂技改厂房与研发综合楼

及职工宿舍楼建设项目

子项目名称 SUB-PROJECT

2#综合楼

图纸名称 TITLE

屋顶层强电平面图

制图 DRAWING BY 唐 博

设计 DESIGNED BY 唐 博

校对 CHECKED BY 马欣凡

专业负责 SPECIALTY CHIEF 邱继国

项目负责 PROJECT CHIEF 吴志刚

审核 EXAMINED BY 邱继国

审定 APPROVED BY 李 坚

图号 DRAWING NO. DS-14

业务号 JOB NO.

出图日期 DATE 2023.04

专业 DISCIPLINE 电气 设计阶段 STAGE 施工图

比例 SCALE 1:100 版 数 SIZE 1

条形码、二维码 BARCODE, QR CODE