


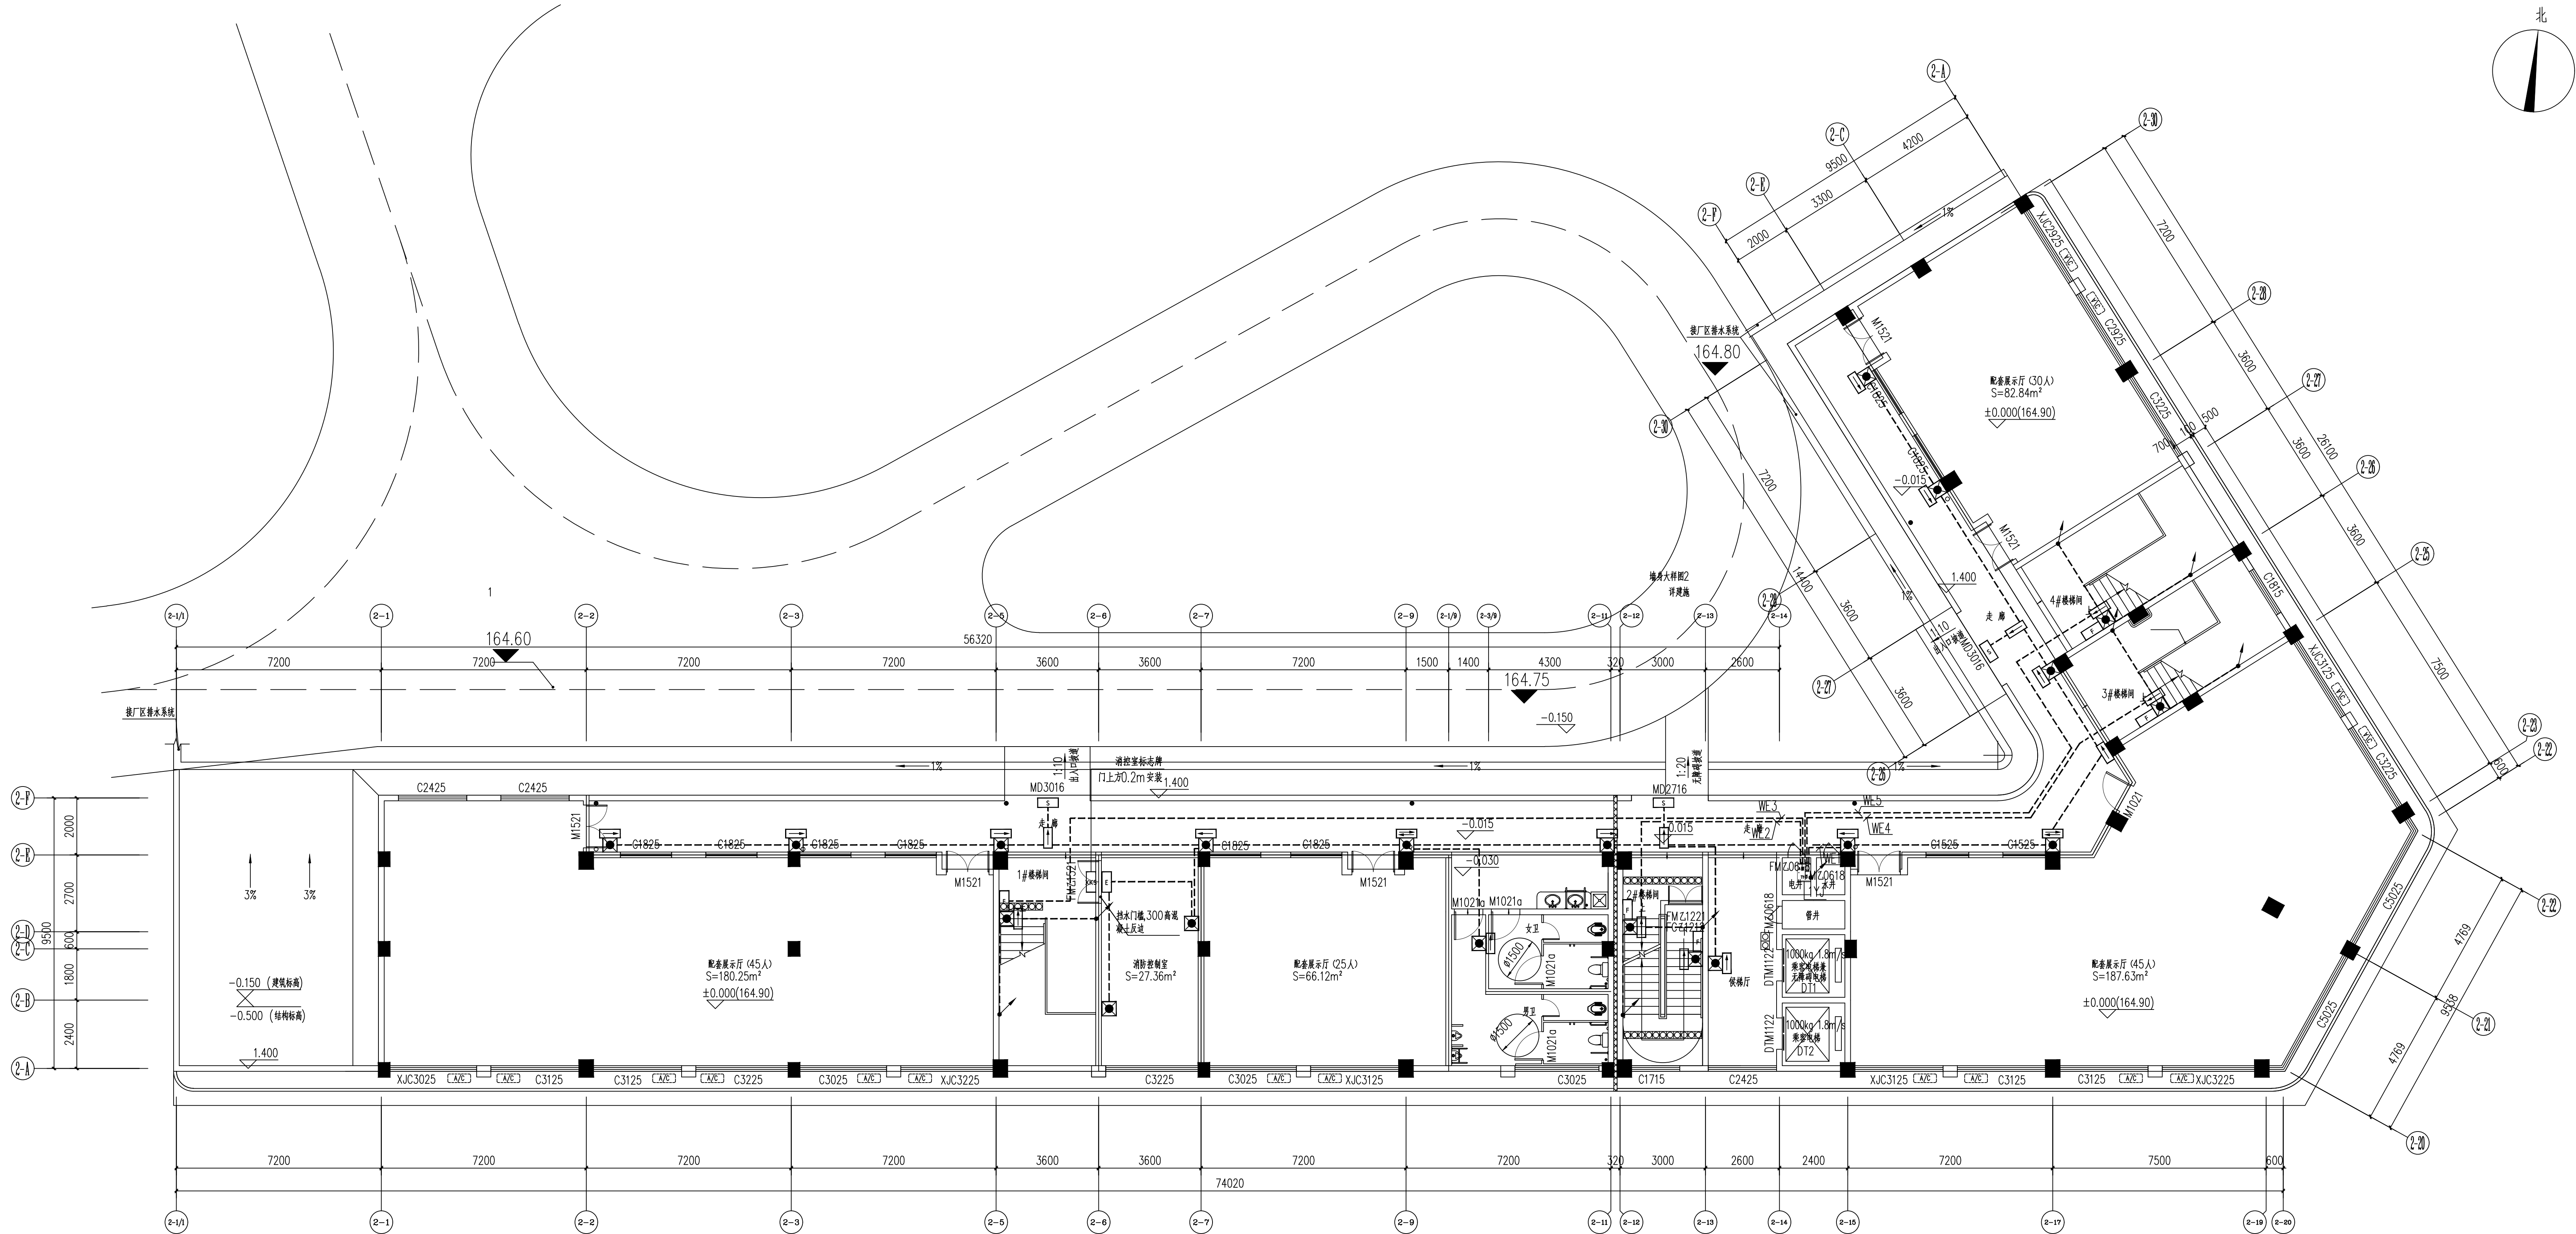

2#综合楼一层应急照明平面图 1:100

2022年版

版权所有，不得复制、套用。
ALL RIGHTS RESERVED.DONT COPIED,REPRODUCED.

广东建筑设计研究院有限公司

GUANGDONG ARCHITECTURAL RESEARCH INSTITUTE CO.,LTD

■建筑行业（建筑工程）甲级 A24400616

■城乡规划编制甲级

■风景园林工程设计专项乙级

■市政公用道路工程乙级

■市政公用排水工程乙级

■环境工程专项污染防治工程乙级

■公路行业（公路）乙级

地址：广州市天河区黄埔大道中309号自编3-09A
电话：(020)38031603 传真：(020)38031600

会签栏 COUNTER SIGNATURE

建 筑	电 气
ARCHI.	ELEC.
结 构	暖 通
STRUCT.	HVAC.
给 排 水	
PLUMBING	

盖章区 STAMP AREA

版次	修改内容	日期
NO.	DESCRIPTION	DATE

建设单位	CLIENT
湖南利农五倍子产业发展有限公司	

项目名称	PROJECT
没食子酸内酯技改厂房与研发综合楼及职工宿舍楼建设项目	

子项目名称	SUB-PROJECT
2#综合楼	

图纸名称	TITLE
一层应急照明平面图	

制图	唐 博	2
DRAWING BY	唐 博	
设计	唐 博	
DESIGNED BY	唐 博	
校对	马欣凡	
CHECKED BY	马欣凡	
专业负责	邱继国	
SPECIALTY CHIEF	邱继国	
项目负责人	吴志刚	
PROJECT CHIEF	吴志刚	
审核	邱继国	
EXAMINED BY	邱继国	
审批	李 坚	
APPROVED BY	李 坚	

图号	DRAWING NO. DS-15
业务号	JOB NO.

出图日期	DATE	2023.04
专业	电气	设计阶段
DISCIPLINE	电气	STAGE
比例	1:100	图 格
SCALE	1:100	SIZE
条形码、二维码	BARCODE,QR CODE	