


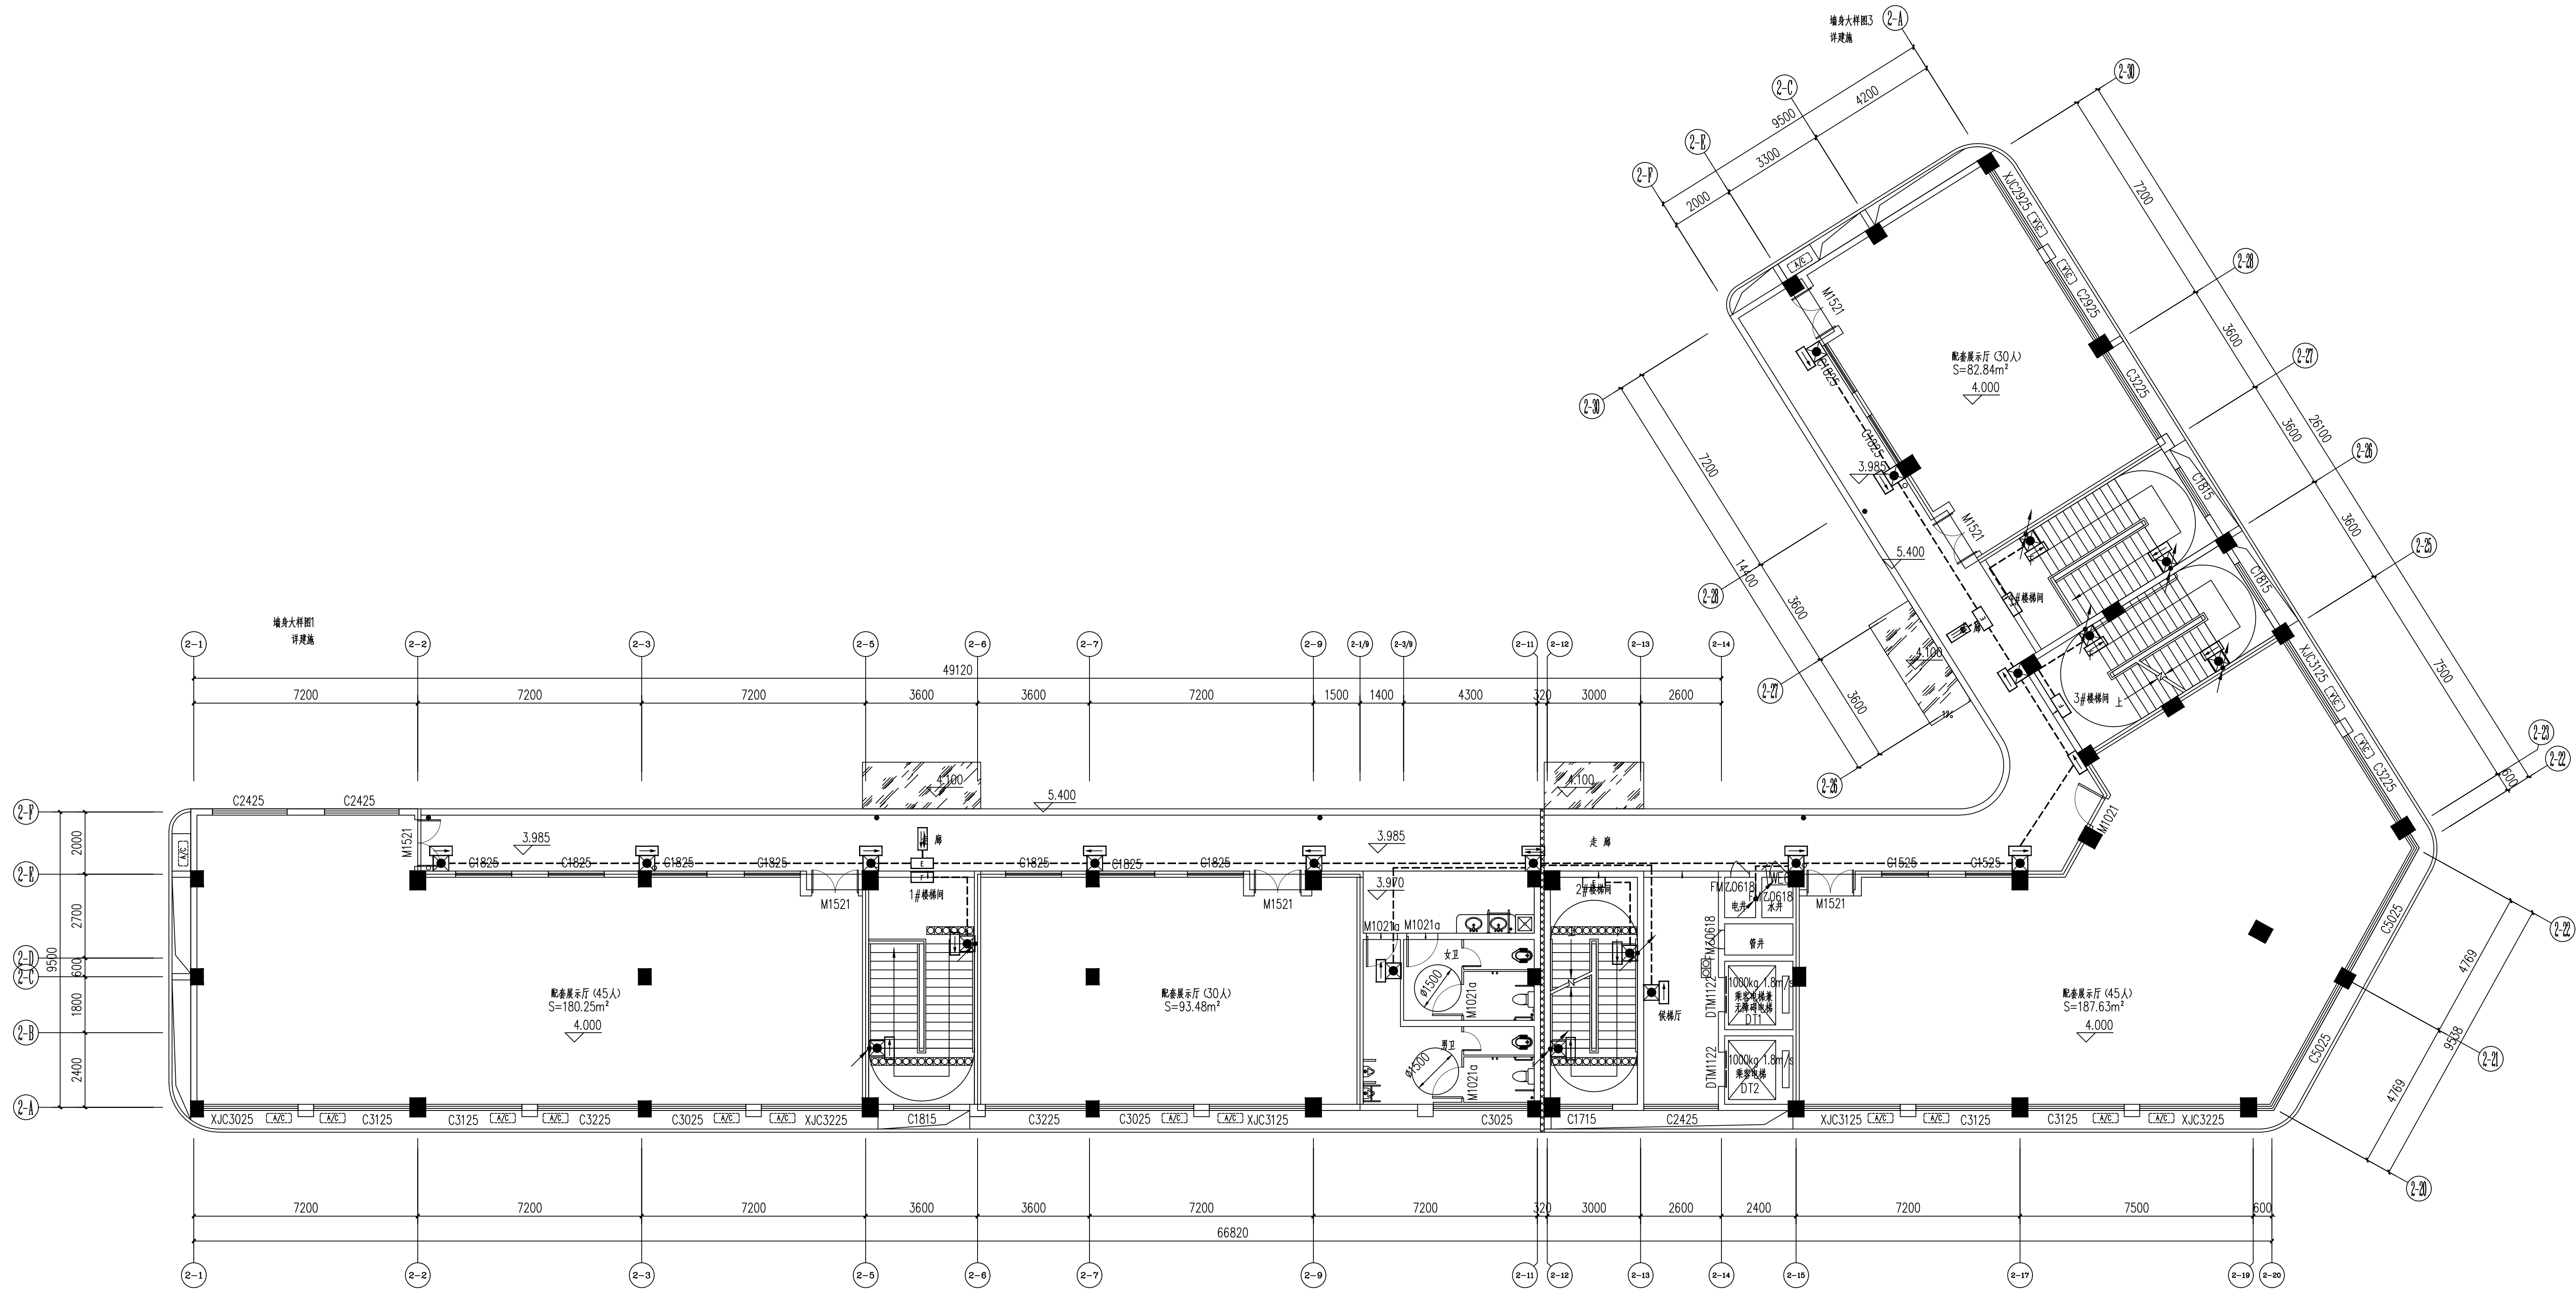

2#综合楼二层应急照明平面图 1:100

2022年版

版权所有，不得复制、套用。
ALL RIGHTS RESERVED.DONT COPYED,REPRODUCED.

广东建筑设计有限公司

GUANGDONG ARCHITECTURAL DESIGN RESEARCH INSTITUTE CO., LTD

■建筑行业（建筑工程）甲级 A34400616

■城乡规划编制甲级

■风景园林工程设计专项乙级

■市政公用工程施工乙级

■市政公用排水工程乙级

■环境工程专项资质（污染防治工程）乙级

■公路行业（公路）乙级

地址：广州市天河区黄埔大道中309号自编3-09A

电话：(020)28031603 传真：(020)28031690

会签栏 COUNTER SIGNATURE

建 筑 ARCHT.	电 气 ELEC.
结 构 STRUCT.	暖 通 HVAC
给 排 水 PLUMBING	

盖章区 STAMP AREA

版次 NO.	修改内容 DESCRIPTION	日期 DATE
建设单位 CLIENT 湖南利农五倍子产业发展有限公司		
项目名称 PROJECT 没食子酸内脂技改厂房与研发综合楼 及职工宿舍楼建设项目		
子项目名称 SUB-PROJECT 2#综合楼		
图纸名称 TITLE 二层应急照明平面图		
制 图 DRAWING BY	唐 博	解
设 计 DESIGNED BY	唐 博	
校 对 CHECKED BY	马欣凡	解
专业负责 SPECIALTY CHIEF	邱继国	邱继国
项目负责人 PROJECT CHIEF	吴志刚	吴志刚
审 核 EXAMINED BY	邱继国	邱继国
审 定 APPROVED BY	李 坚	李 坚
图号 DRAWING NO. DS-16		
业务号 JOB NO.		
出图日期 DATE 2023.04		
专 业 DISCIPLINE	电 气	设计阶段 STAGE 施工图
比 例 SCALE	1:100	修 改 SIZE
条形码、二维码 BARCODE,QR CODE		