


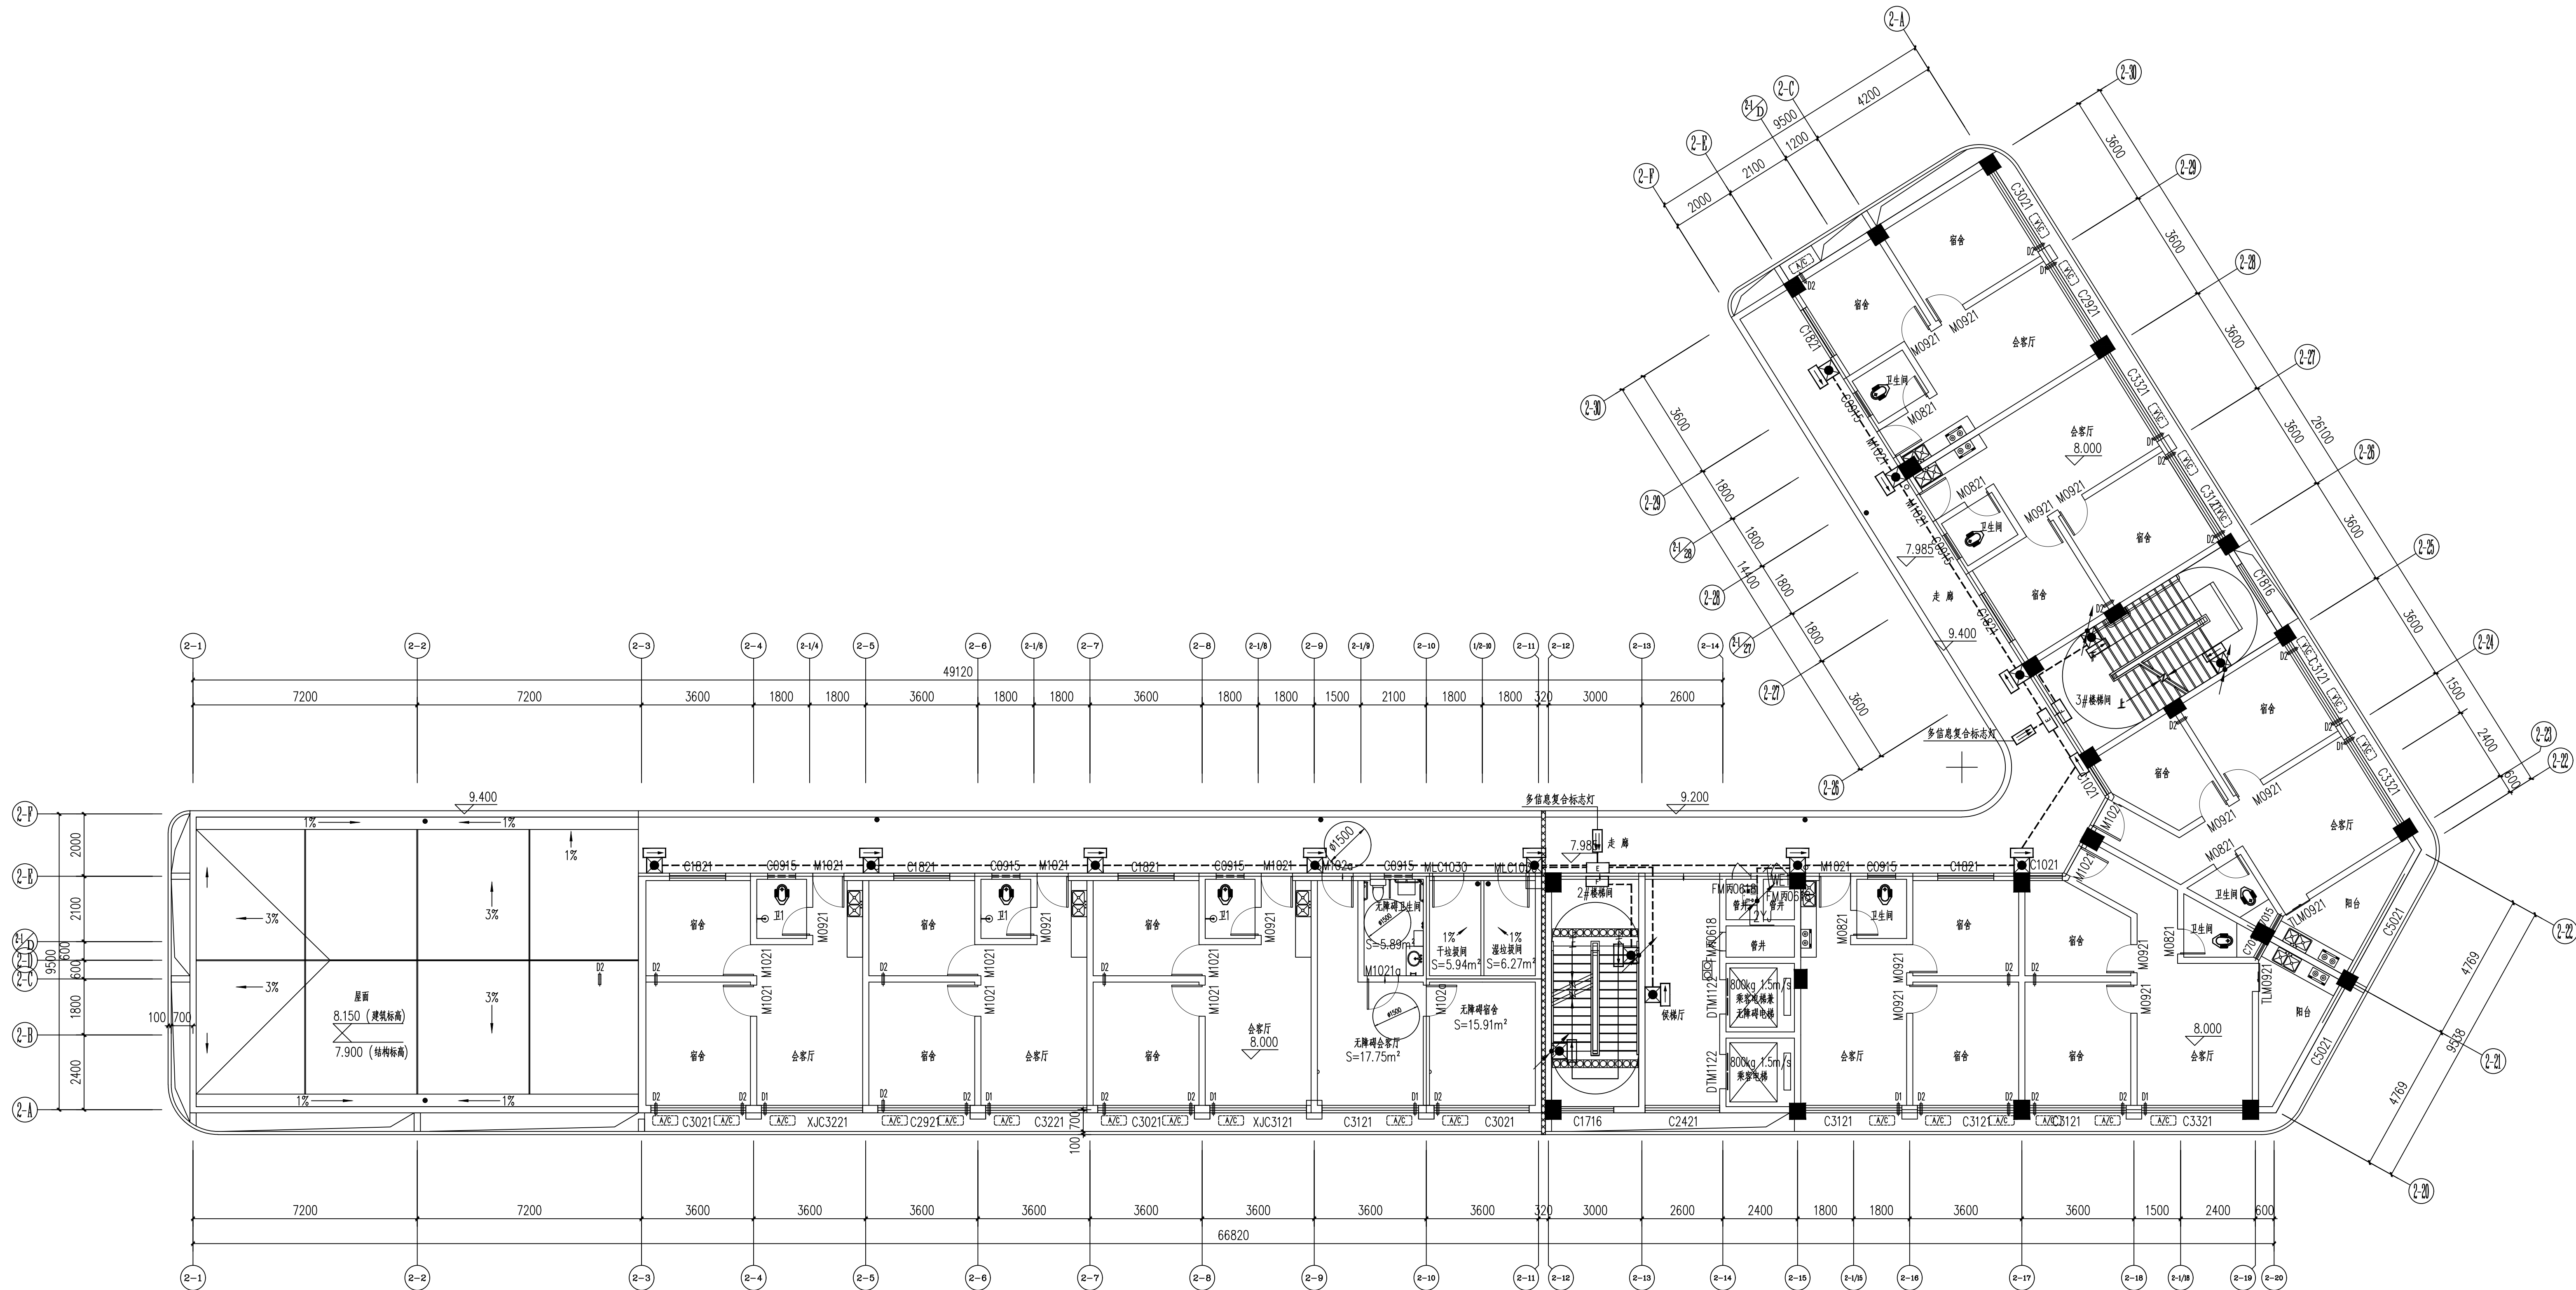

2#综合楼三层应急照明平面图 1:100

2022年版

版权所有，不得复制、套用。
ALL RIGHTS RESERVED.DONT COPYED,REPRODUCED.

广东建筑设计院有限公司

GUANGDONG ARCHITECTURAL DESIGN RESEARCH INSTITUTE CO.,LTD

■建筑行业（建筑工程）甲级 A34404616

■城乡规划编制甲级

■风景园林工程设计专项乙级

■市政公用工程设计乙级

■市政公用工程乙级

■环境工程专项设计乙级

■公路行业（公路）乙级

地址：广州市天河区黄埔大道中309号自编3-09A
电话：(020)38031603 传真：(020)38031600

会签栏 COUNTER SIGNATURE

建 筑

ARCHI.

电 气

ELEC.

结 构

STRUCT.

暖 通

HVAC.

给 排 水

PLUMBING

盖章区 STAMP AREA

版次	修改内容	日期
NO.	DESCRIPTION	DATE
建设单位	CLIENT	
湖南利农五倍子产业发展有限公司		
项目名称	PROJECT	
没食子酸丙酯技改厂房与研发综合楼及职工宿舍楼建设项目		
子项目名称	SUB-PROJECT	
2#综合楼		
图纸名称	TITLE	
三层应急照明平面图		
制图	DRAWING BY	唐 博
设计	DESIGNED BY	唐 博
校对	CHECKED BY	马欣凡
专业负责	SPECIALTY CHIEF	邱继国
项目负责人	PROJECT CHIEF	吴志刚
审核	EXAMINED BY	邱继国
审批	APPROVED BY	李 坚
图号	DRAWING NO.	DS-17
业务号	JOB NO.	
出图日期	DATE	2023.04
专业	DISCIPLINE	电气
设计阶段	STAGE	施工图
比例	SCALE	1:100
修 改	REV.	
条形码、二维码	BARCODE,QR CODE	