


建设单位/CLIENT:
麻阳苗族自治县远桥房地产开发有限公司

项目名称/PROJECT:
远程国际

子项目名称/SUB-PROJECT:
远程国际

区位图/REGIONAL LOCATION MAP :

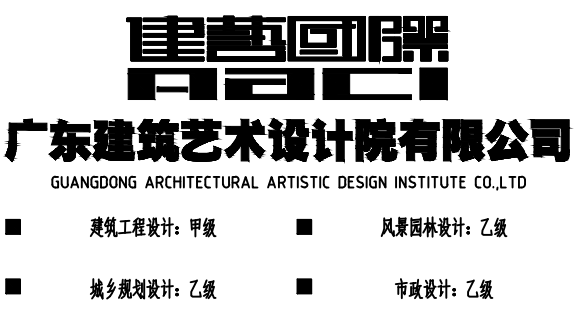

图纸名称/TITLE:
五~十三层平面图
十四层平面图

项目名称/PROJECT:
远程国际

设计 DESIGNED	古新辉	
校对 CHECKED	吴新红	
专业负责人 CHIEF	吴志刚	
项目负责人 PROJECT CHIEF	吴志刚	
审核 IDENTIFIED	黄履优	
审定 APPROVED	李 坚	

业务号/JOB NO.

设计阶段/STATUS: 施工图

专业/DISCIPLINE: 建筑

比例/
SCALE: 1: 100 规格/
SIZE: A1


出图日期/DATE: 2021. 06

图号/DRAWING NO. JS-19

版次 NO.	修改内容 DESCRIPTION	日期 DATE


条形码/BARCODE:

版权所有，不得复制、套用。
ALL RIGHTS RESERVED, DON'T COPIED, REPRODUCED.

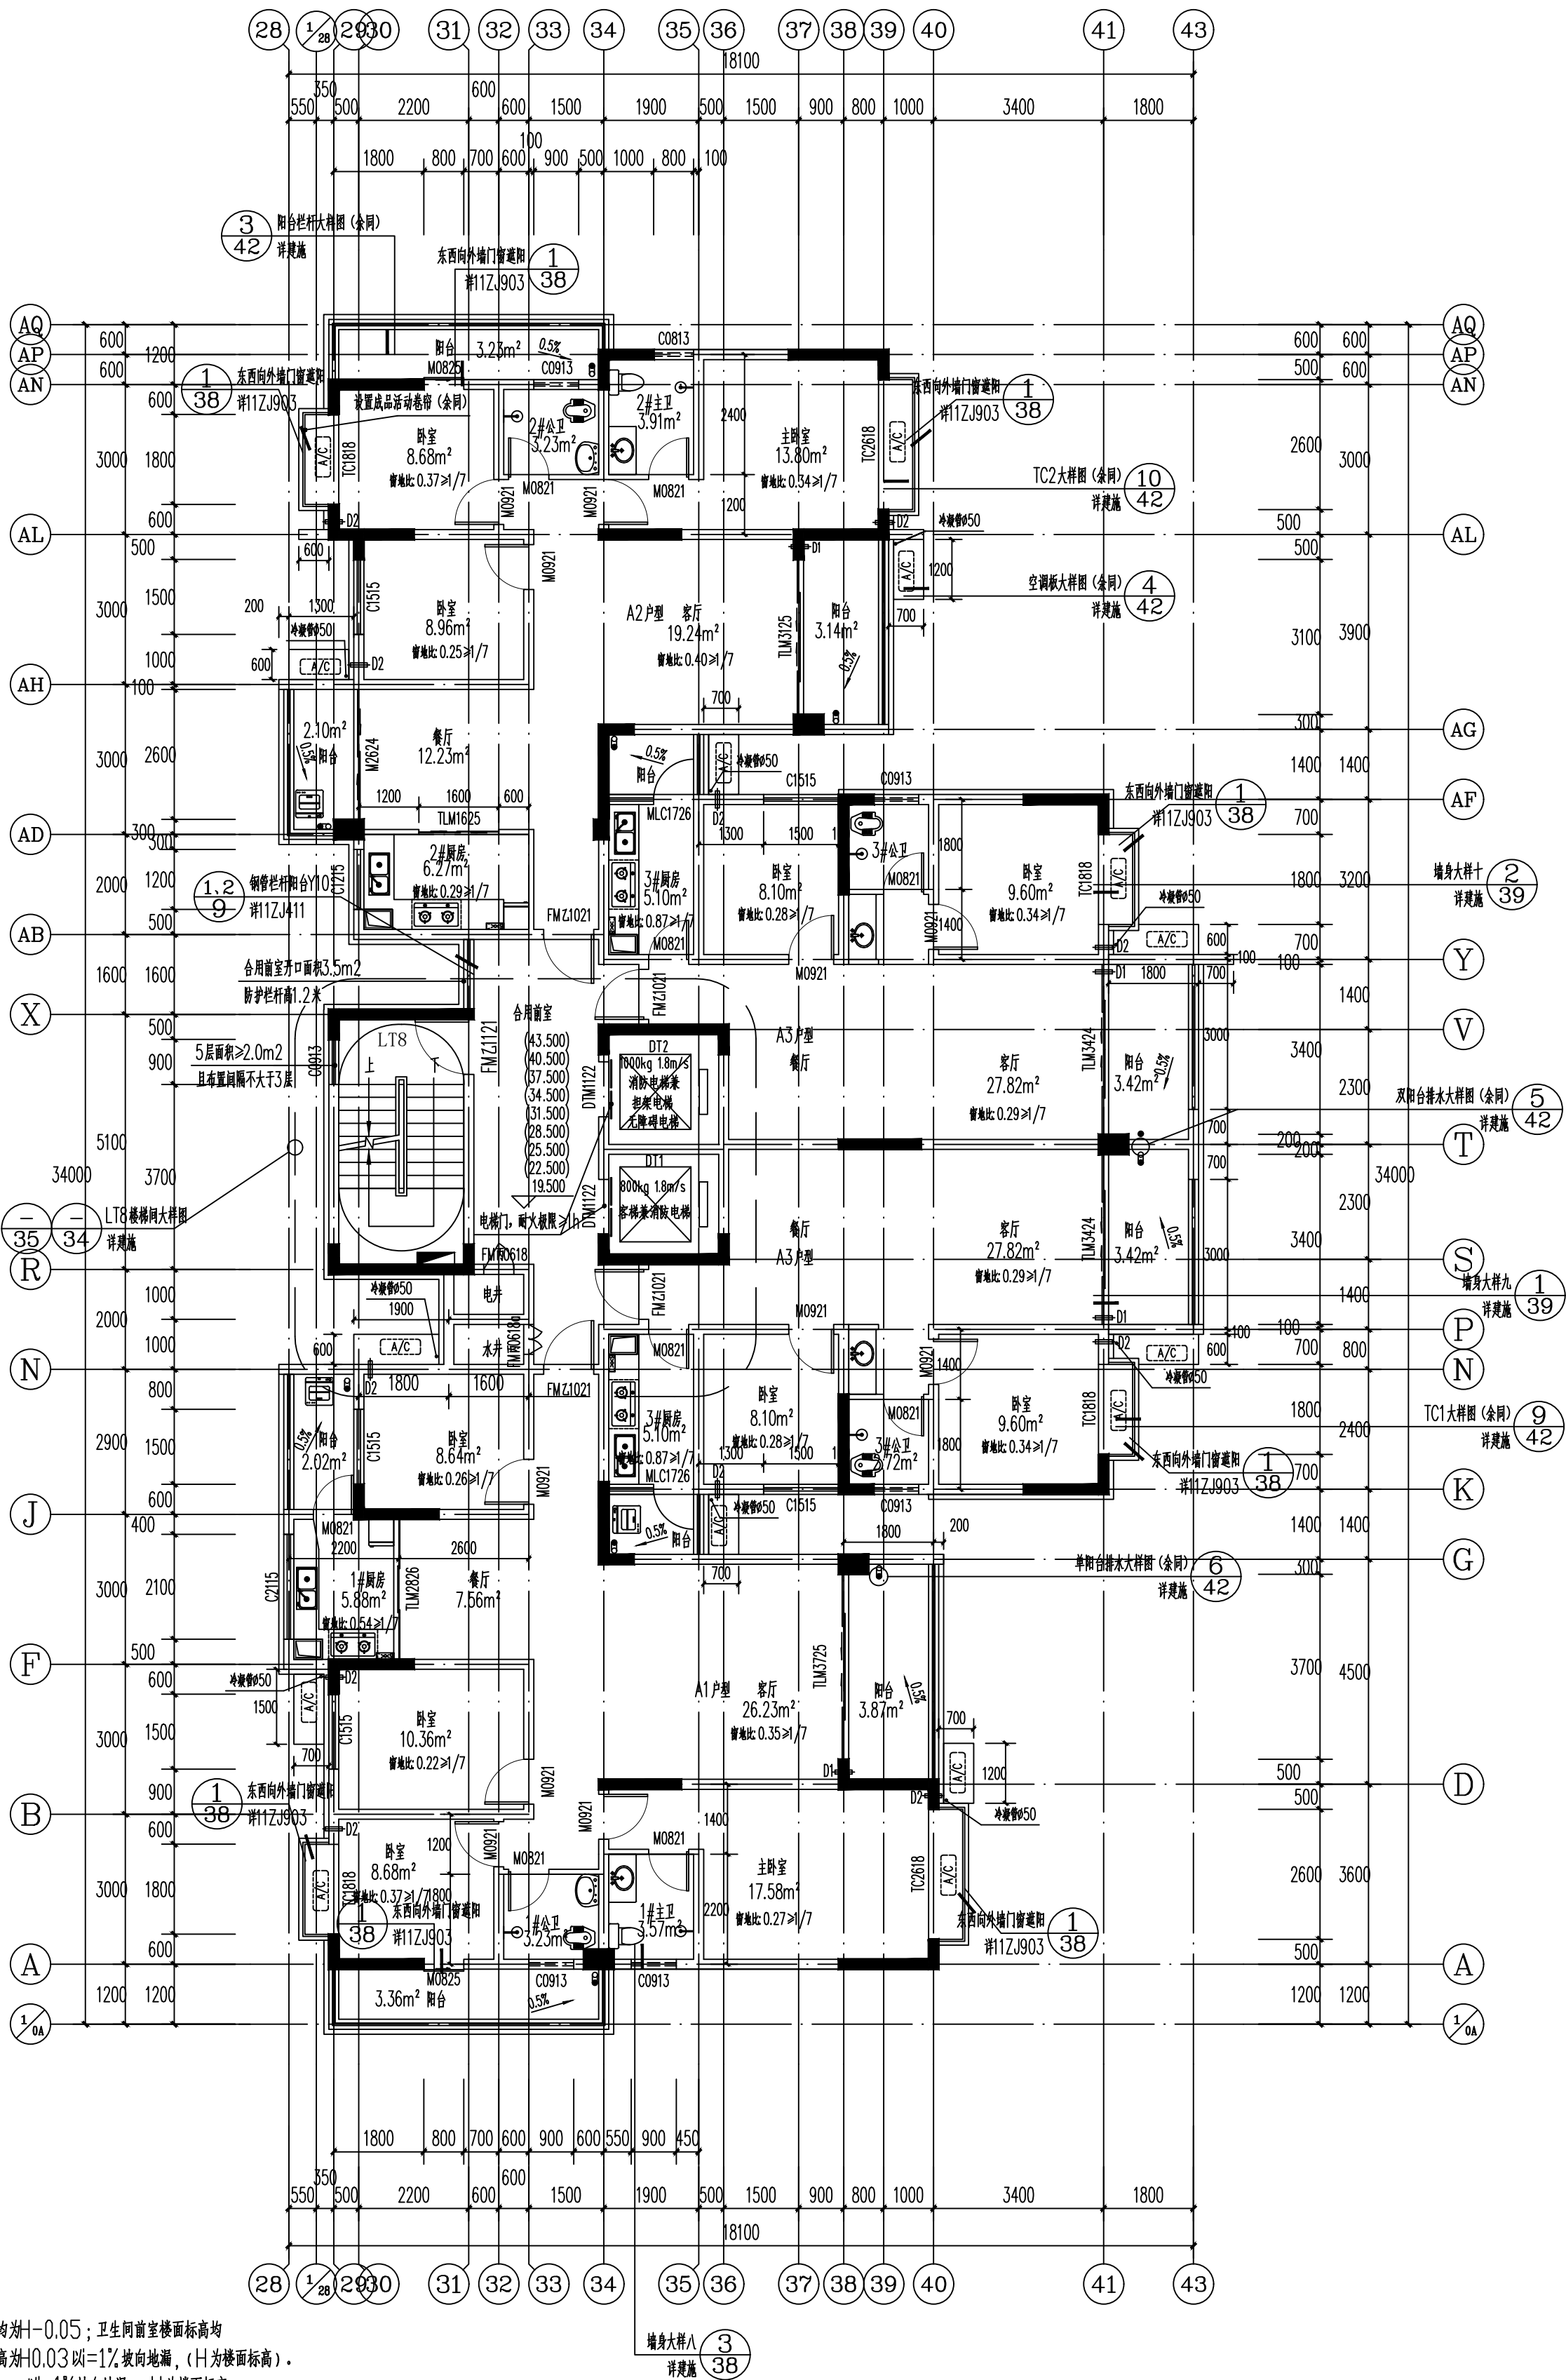

- 说明:
- 除注明者外，卫生间楼面标高均 ± 0.05 ；卫生间首层楼面标高均 ± 0.03 。厨房楼面标高为 ± 0.03 或 $\pm 1\%$ 坡向地漏，(H为楼面标高)。
 - 阳台楼面标高均 ± 0.05 ， $\text{H}=\pm 1\%$ 坡向地漏，(H为楼面标高)。
 - ②为80空调穿线管预留洞，管向室外倾斜 10% ，距中心距地漏 2200 高，中心距地漏 150 或平挂。
 - ③为80空调穿线管预留洞，管向室外倾斜 10% ，距中心距地漏 300 高，中心距地漏 150 或平挂。
 - 凡露台高小 $\geq 900\text{mm}$ 时，作防护栏杆具体做法详见11ZJ401 ③防护栏杆要符合安全防护要求，以防止人坠落。
 - 所有凸窗均设 $\geq 900\text{mm}$ 高防护栏杆。
 - 通风处预留洞(位置见上图) 700×800 (H)，距底距顶层面 950 (H)。
 - 图中未注尺寸位置已在同一户型相应位置标注。
 - 图中设备预留洞尺寸及位置与设备专业图纸冲突时应及时通知设计院。

五~十三层平面图 1:100
本层建筑面积: 420.60m²

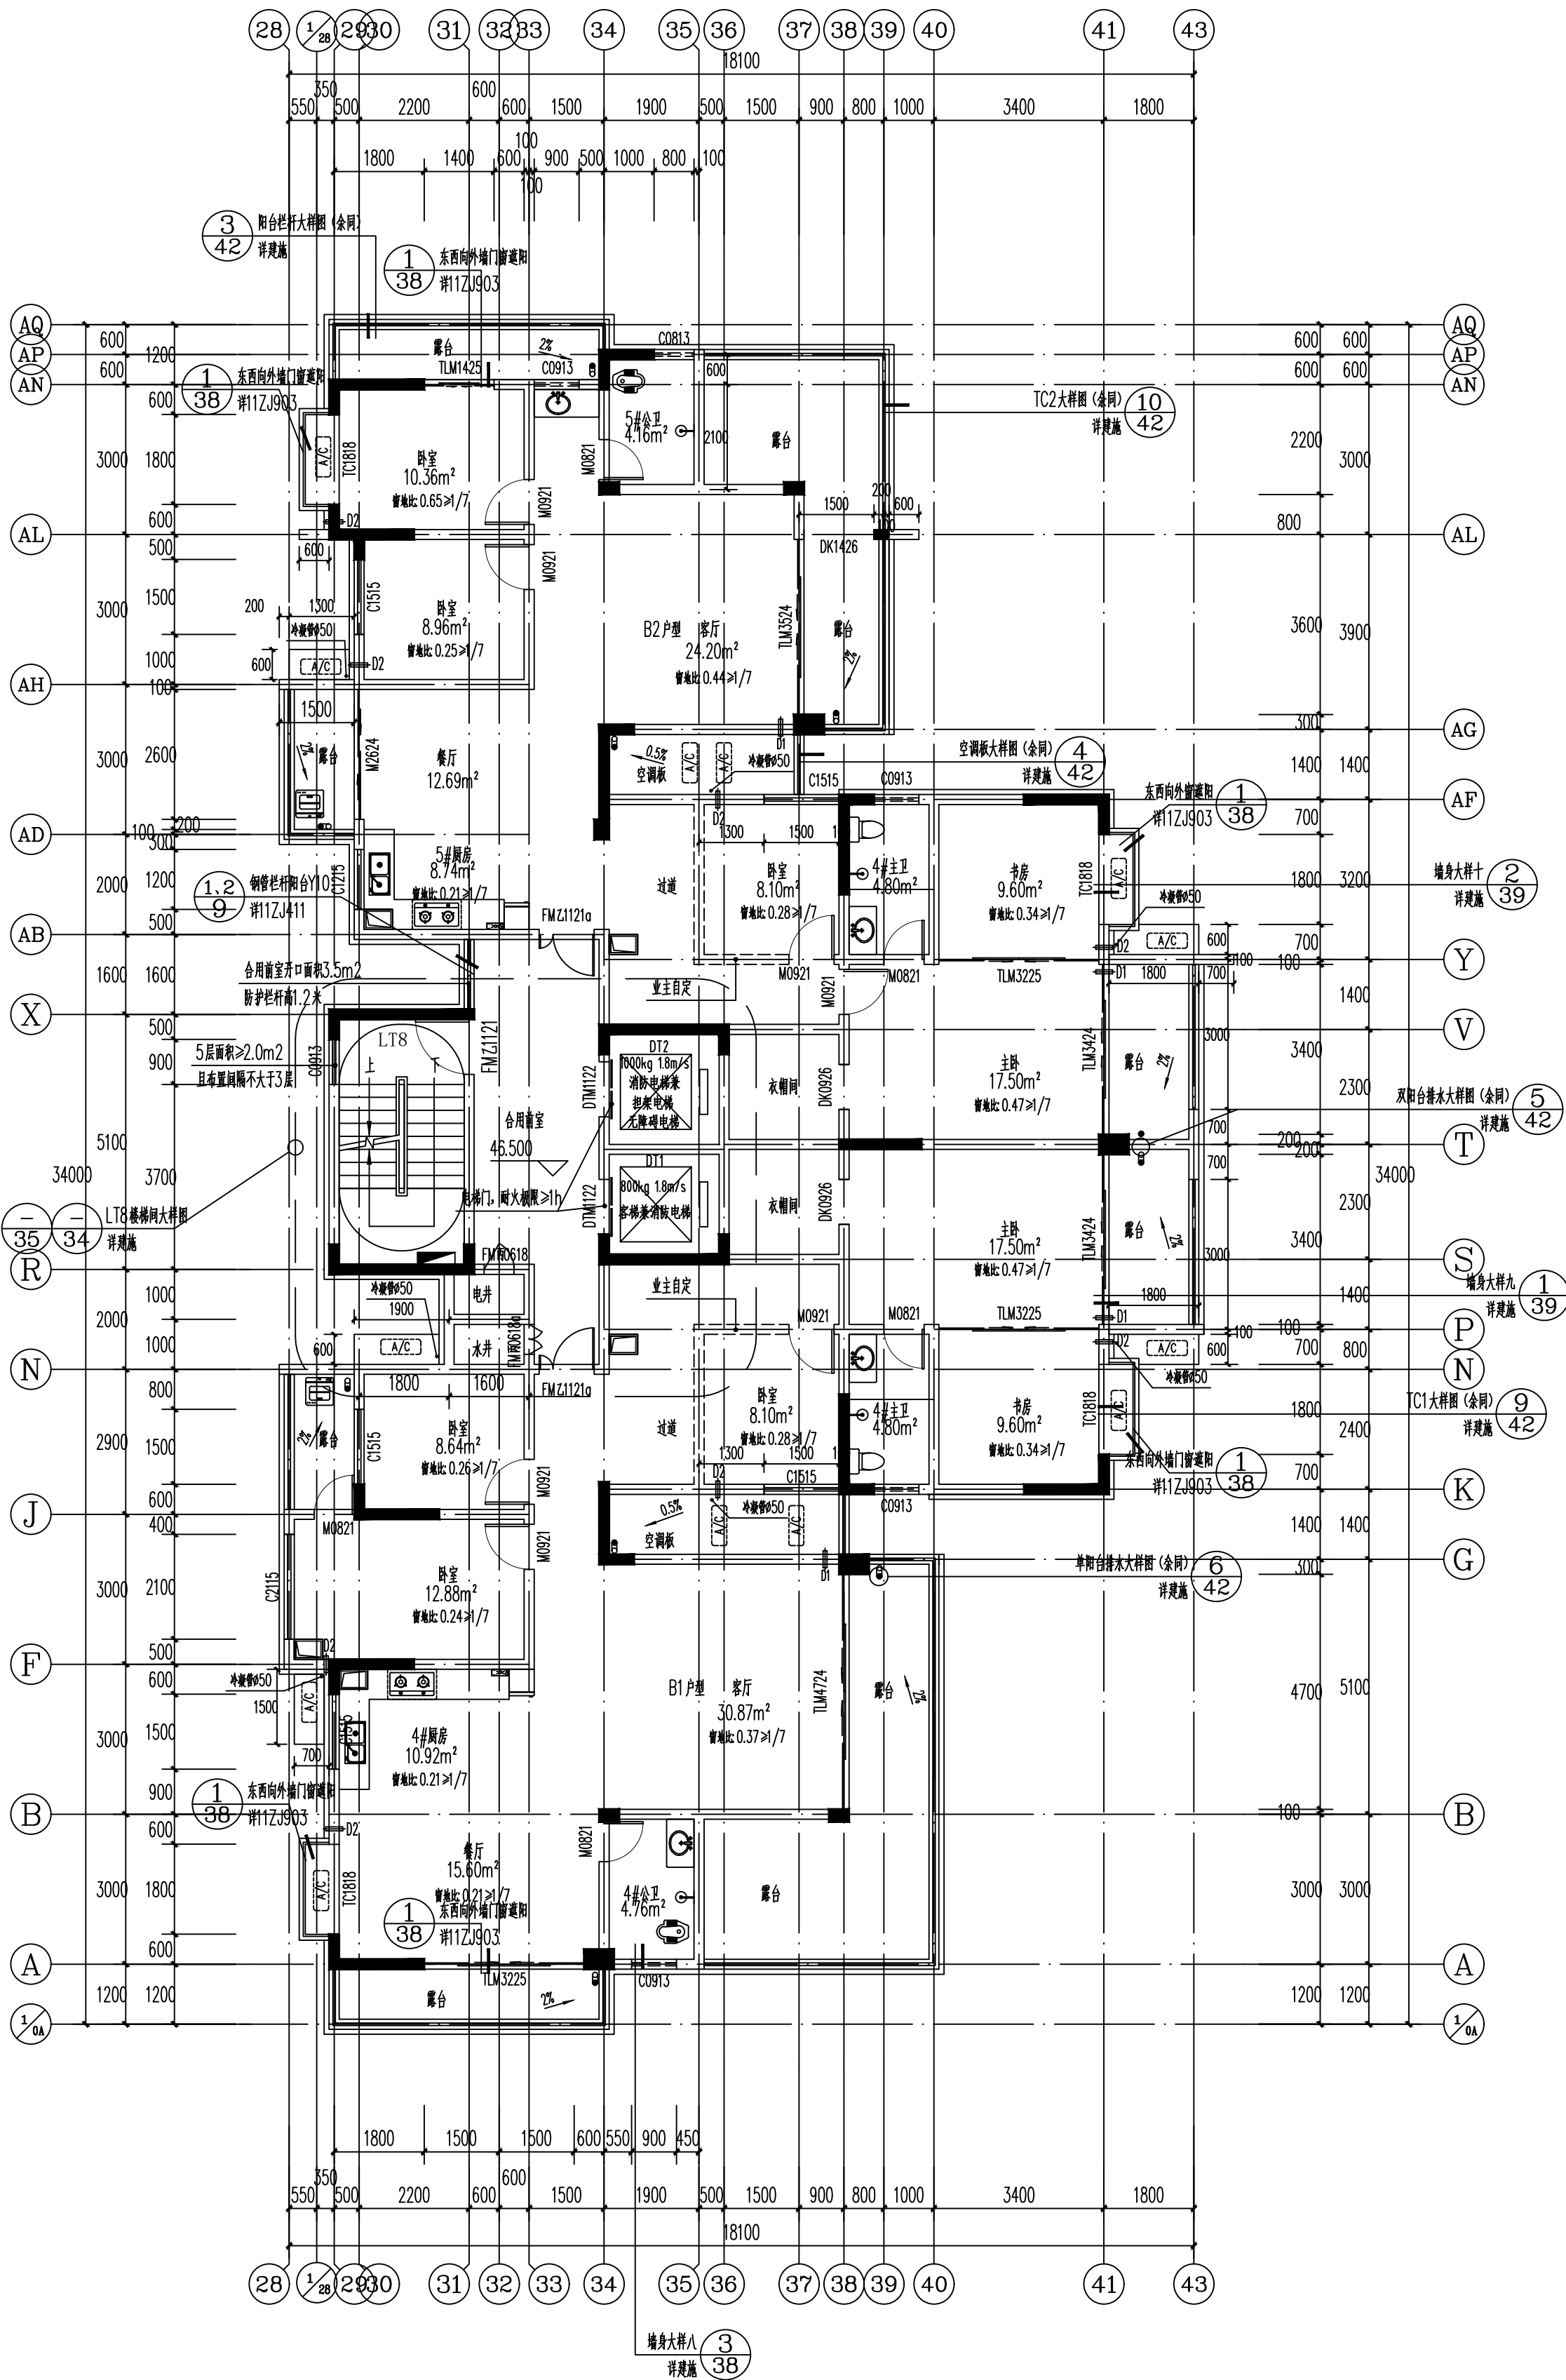

十四层平面图 1:100
本层建筑面积: 363.48m²