

建设单位/CLIENT:
麻阳苗族自治县远桥房地产开发有限公司

项目名称/PROJECT:
远程国际

子项目名称/SUB-PROJECT:
远程国际

区位图/REGIONAL LOCATION MAP :



图纸名称/TITLE:
住宅屋顶平面图
屋顶构件平面图

项目名称/PROJECT:
远程国际

设计 DESIGNED	古新辉	
校对 CHECKED	吴新红	
专业负责人 CHIEF	吴志刚	
项目负责人 PROJECT CHIEF	吴志刚	
审核 IDENTIFIED	黄履优	
审定 APPROVED	李 坚	

业务号/JOB NO.

设计阶段/STATUS: 施工图

专业/DISCIPLINE: 建筑

比例/
SCALE: 1: 100 规格/
SIZE: A1


出图日期/DATE: 2021. 06

图号/DRAWING NO. JS-20

版次 NO.	修改内容 DESCRIPTION	日期 DATE

条形码/BARCODE:


版权所有，不得复制、套用。
ALL RIGHTS RESERVED, DON'T COPIED, REPRODUCED.

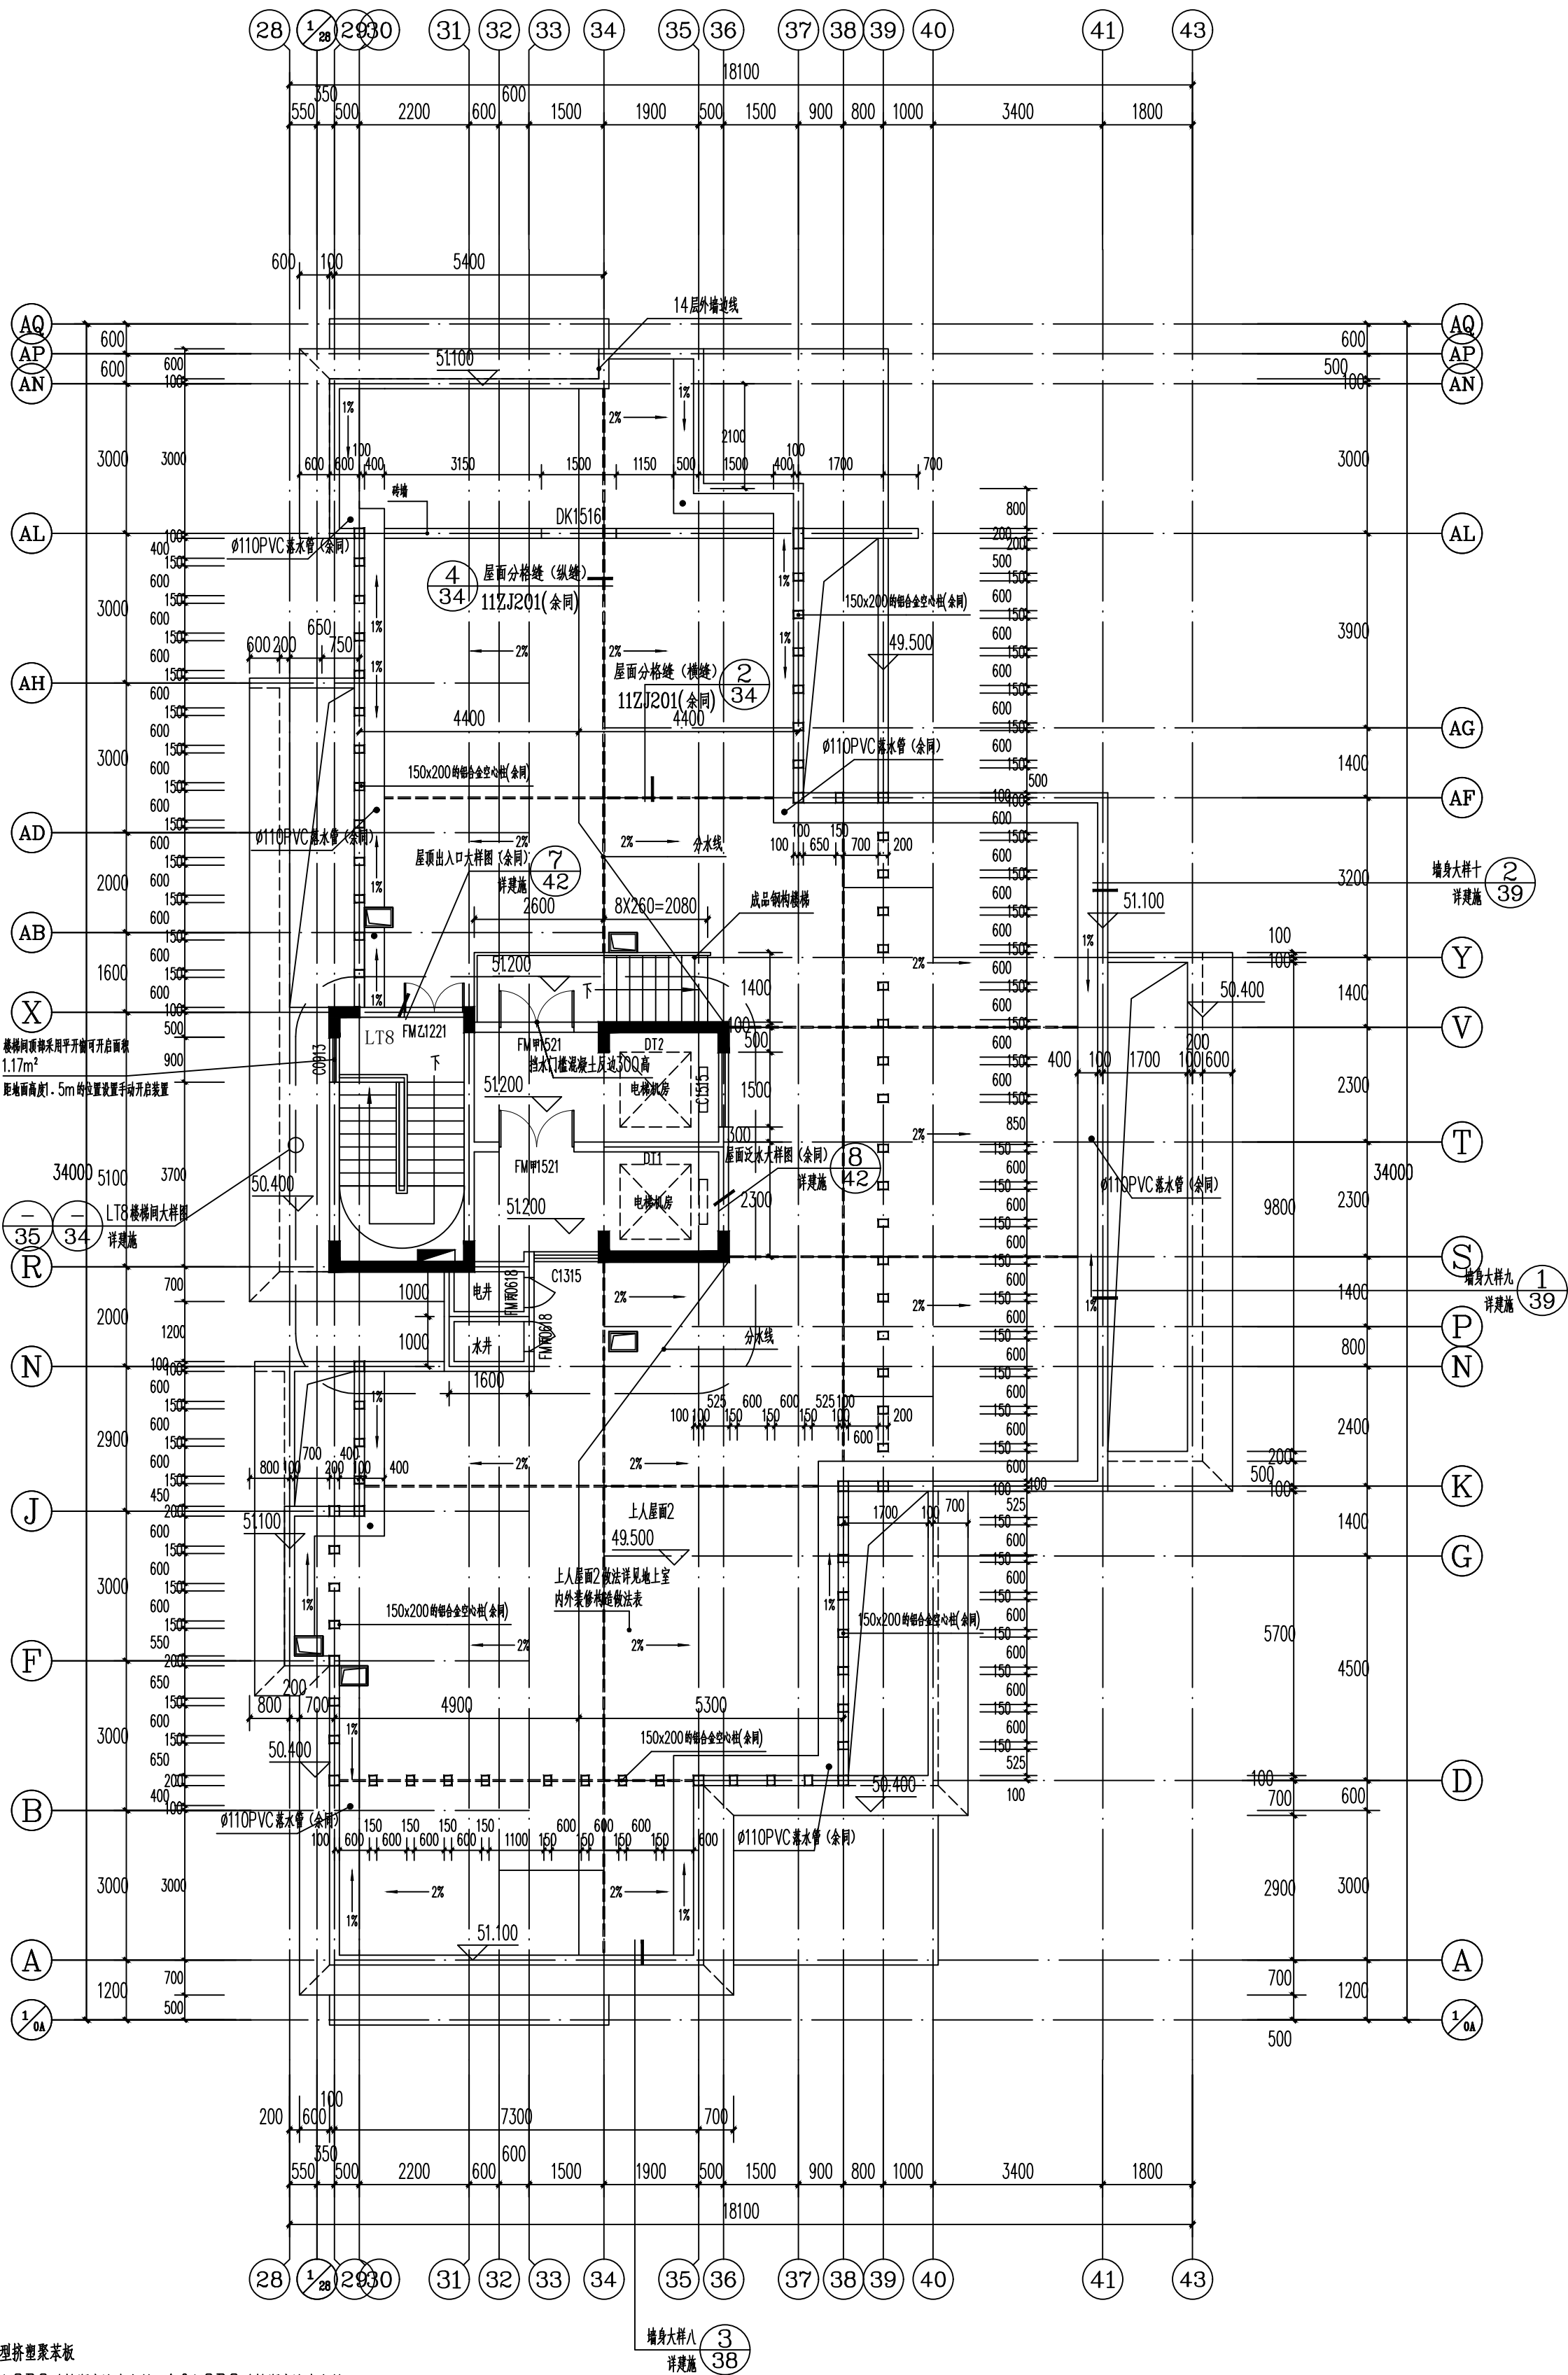

住宅屋顶平面图 1:100

本层建筑面积: 43.69m²

- 注:
- 保温材料为: 难燃型挤塑聚苯板
防水材料为: 3.0㎜SBS改性沥青防水卷材+4.0㎜SBS改性沥青防水卷材
上人平屋面做法见SJJ001-128~图106
非上人平屋面做法见SJJ001-122~图105
屋面分格缝做法见SJJ201-图106分格缝6m×6m
 - 小屋面至大屋面的雨水管下方设水簸箕, 做法见SJJ201-图106
 - 屋面采用φ110UPVC雨水管, 做法见115ZJ201-图106
 - 檐口、雨篷滴水线做法见117J901-图106
 - 透气道出屋面做法见SJJ201-图106

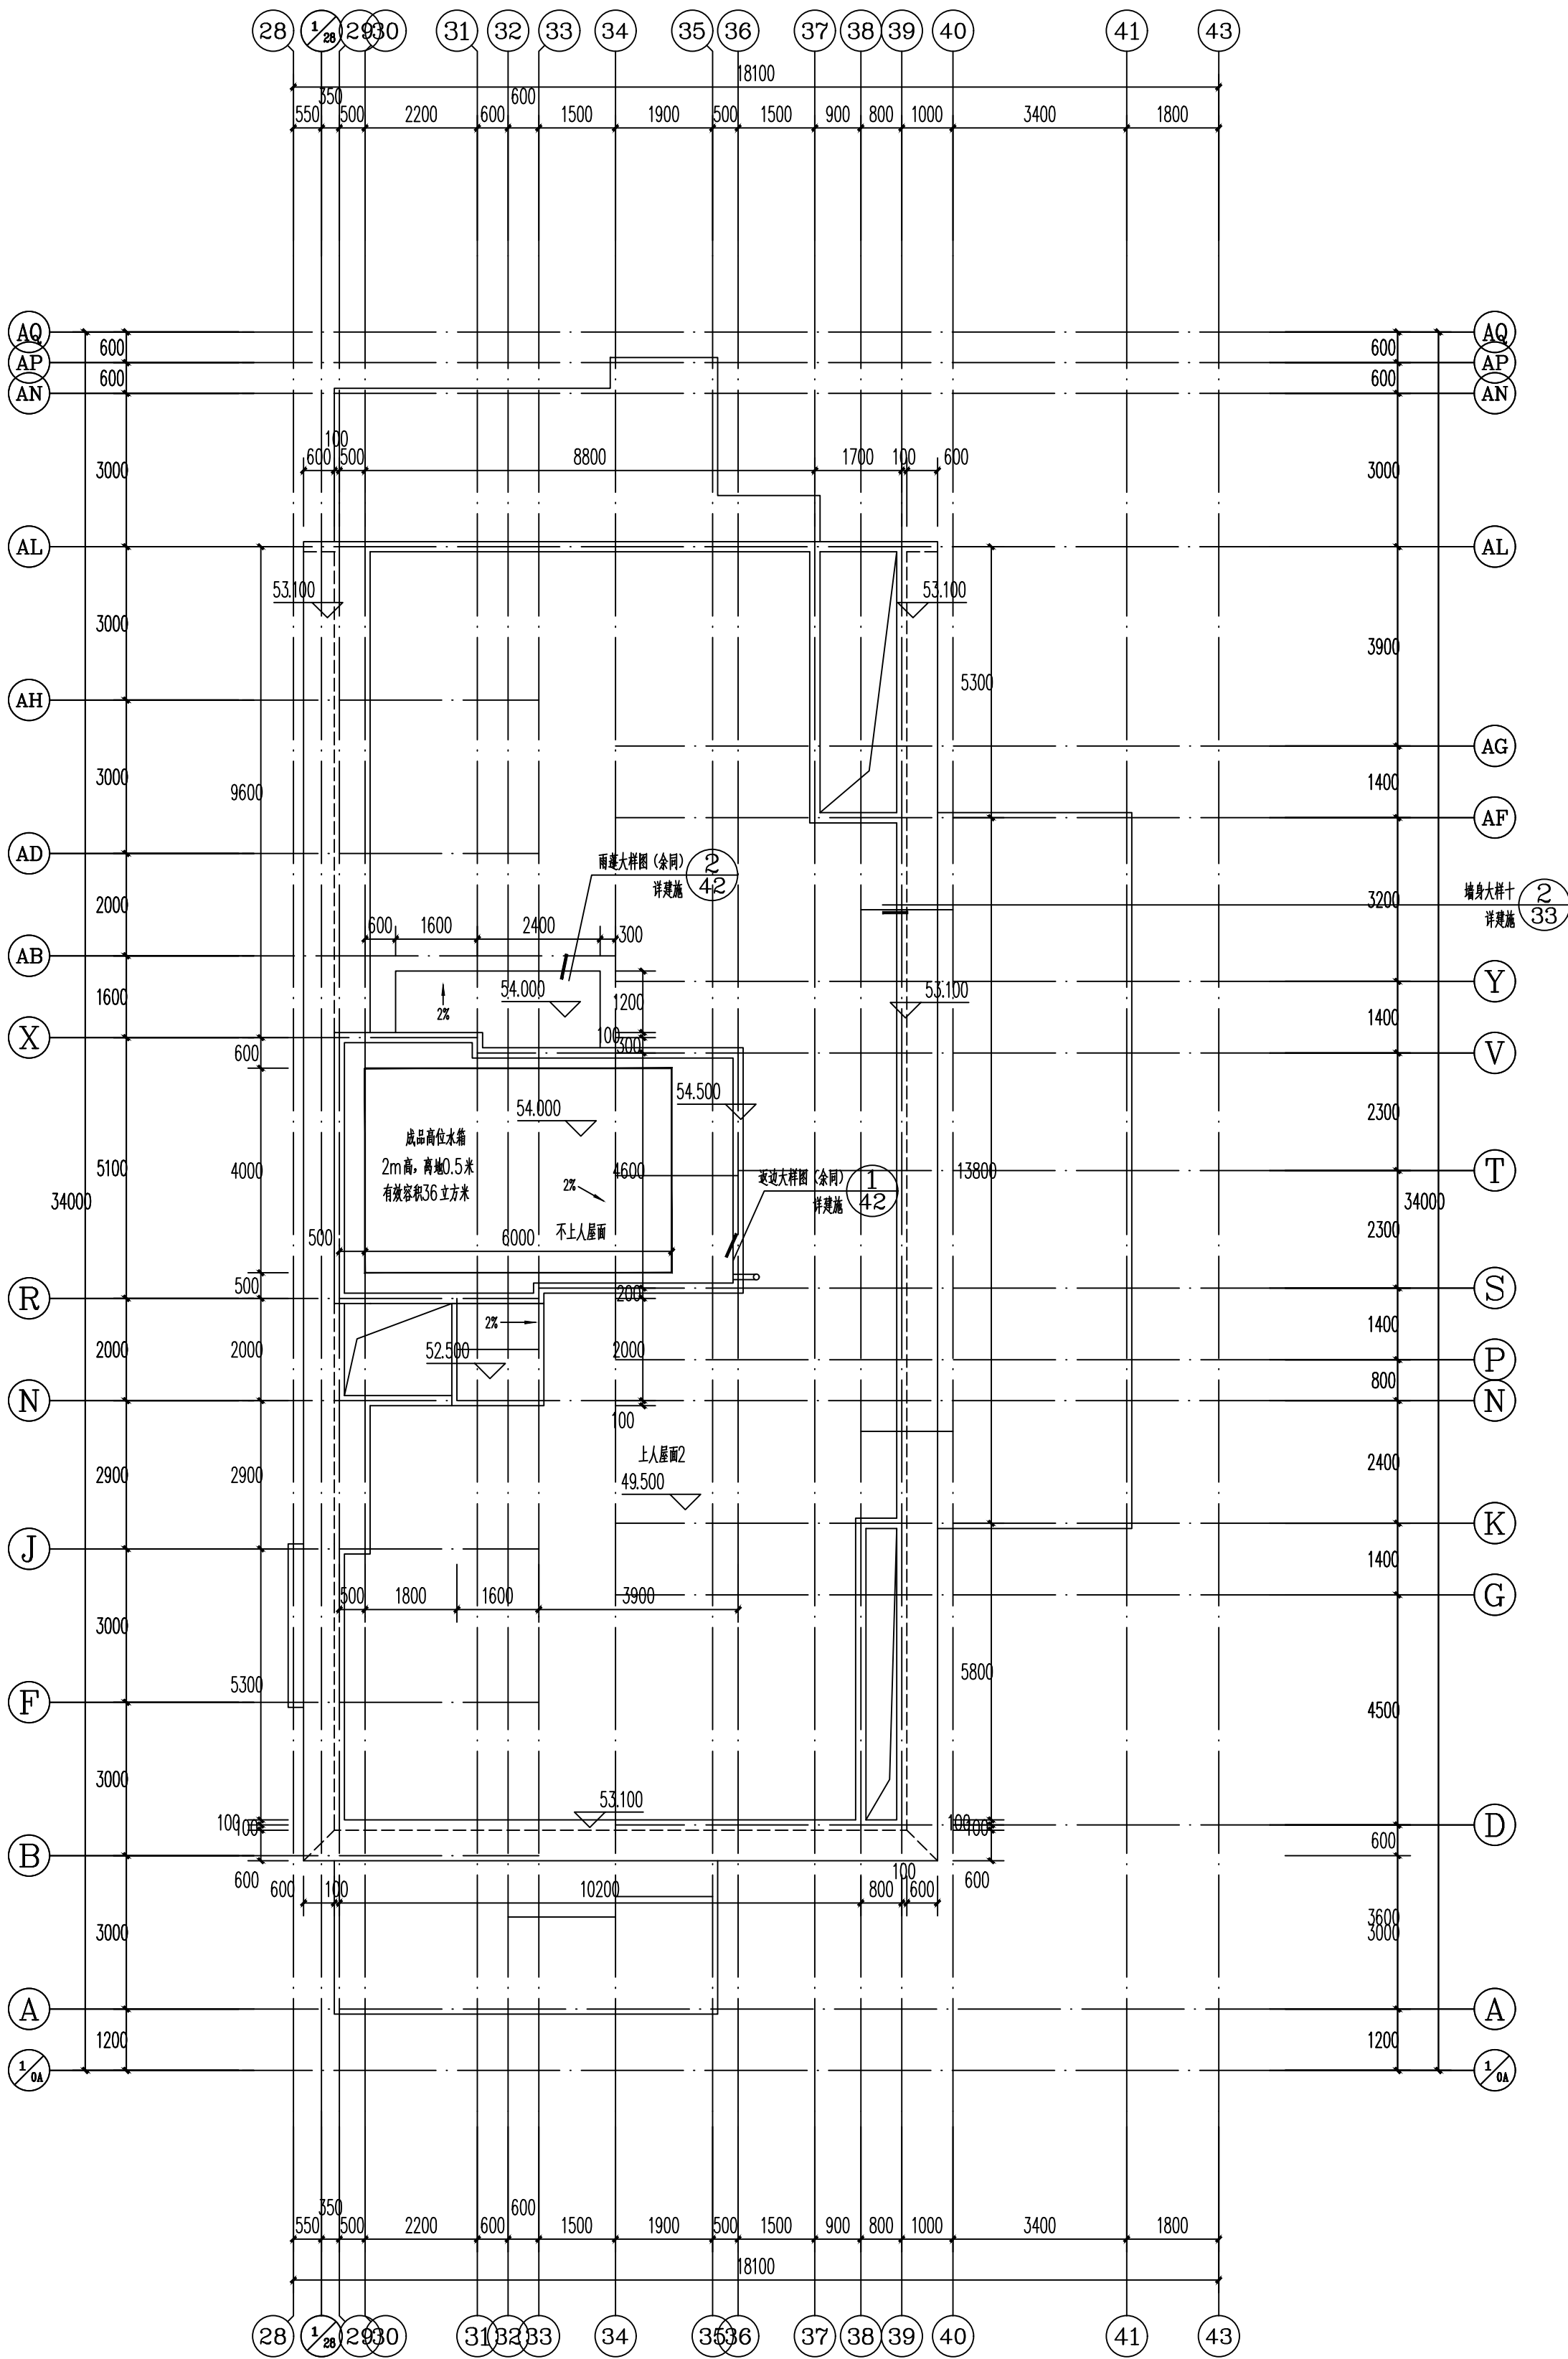

屋顶构件平面图 1:100