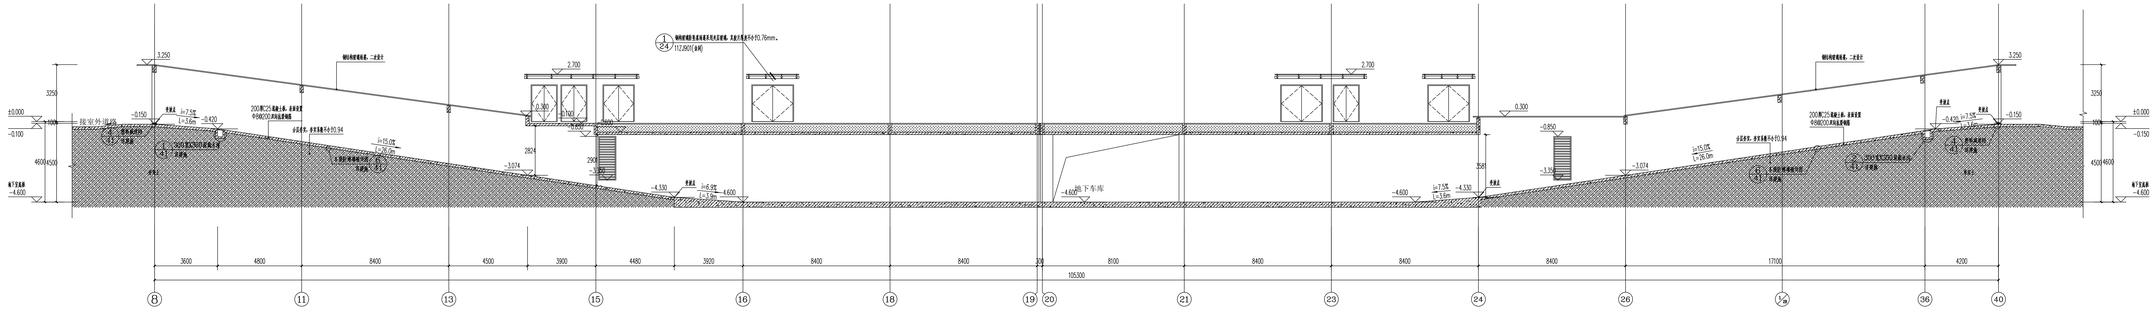

车道1-1剖面 1:100

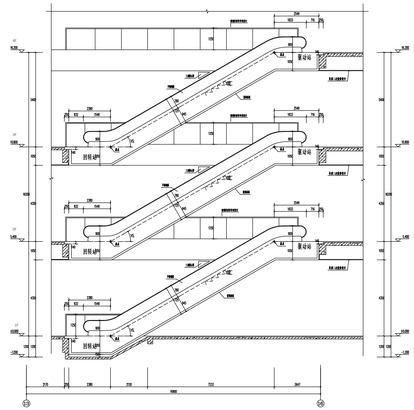

FT-01自动扶梯剖面图 1:50

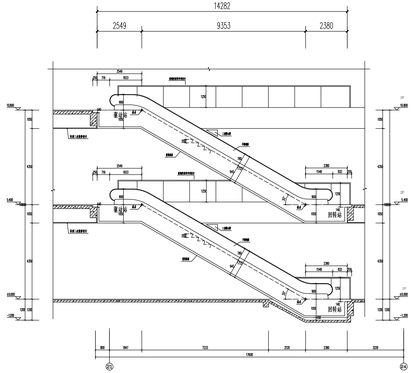

FT-02自动扶梯剖面图 1:50

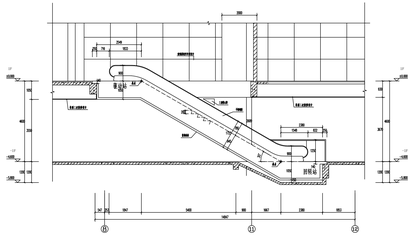

FT-03自动扶梯剖面图 1:50

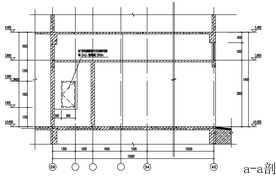

a-a剖面图 1:100

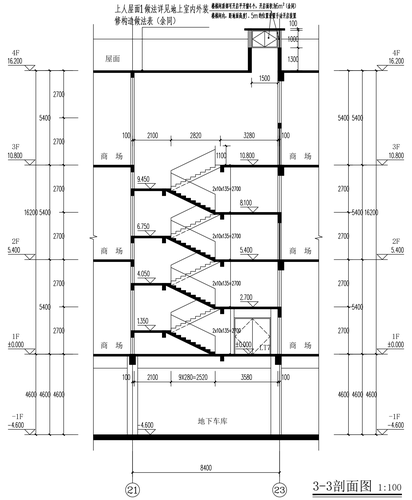

3-3剖面图 1:100

注：LT7剖面图

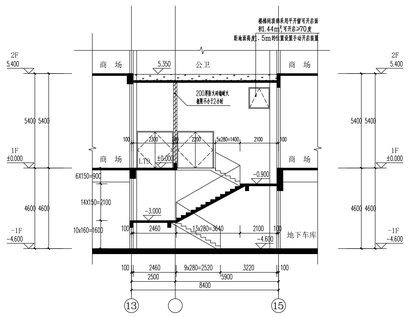

5-5剖面图 1:100

注：LT9剖面图

1.本工程楼梯踏步高、宽、步数及平台宽度等详楼梯大样。楼梯栏杆采用不锈钢栏杆Φ00高，详11ZJ401-13-W扶手详11ZJ401-37-16，（注：当扶手水平长度大于0.5m时，栏杆净高不低于1100）。
2.起步详11ZJ40138-6；扶手与填充墙连接详11ZJ401-42-5，防滑详05ZJ401-39-6
3.佛井大于110，均做防盗网处理。

建设单位/CLIENT:
麻阳苗族自治县远桥房地产开发有限公司

项目名称/PROJECT:
远程国际

子项目名称/SUB-PROJECT:
远程国际

区位图/REGIONAL LOCATION MAP :

广东建筑艺术设计院有限公司
GUANGDONG ARCHITECTURAL ARTISTIC DESIGN INSTITUTE CO.,LTD

图纸名称/TITLE:
车道1-1剖面
自动扶梯剖面图、a-a剖面图
3-3剖面图、5-5剖面图

项目名称/PROJECT:
远程国际

设计 DESIGNED	古新辉	
校对 CHECKED	吴新红	
专业负责人 CHIEF	吴志刚	
项目负责人 PROJECT CHIEF	吴志刚	
审核 IDENTIFIED	黄观优	
审定 APPROVED	李 坚	

业务号/JOB NO.

设计阶段/STATUS: 施工图

专业/DISCIPLINE: 建施

比例/SCALE: 1：100 规格/SIZE: A1

出图日期/DATE: 2021.06

图号/DRAWING NO. JS-25

版次 NO.	修改内容 DESCRIPTION	日期 DATE

条形码/BARCODE:

版权所有，不得复制、套用。
ALL RIGHTS RESERVED, DON'T COPIED, REPRODUCED.