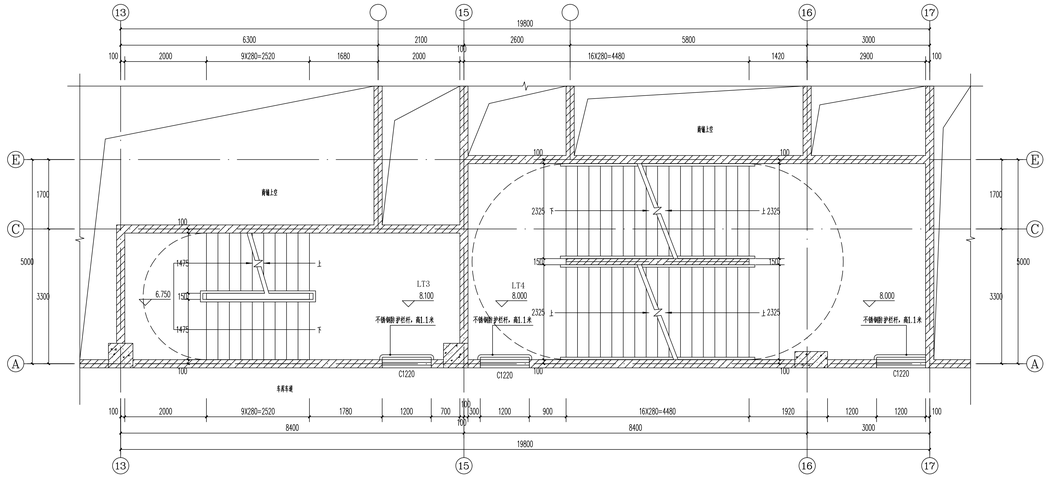

LT3、LT4楼梯间H=8.100处平面图 1:50

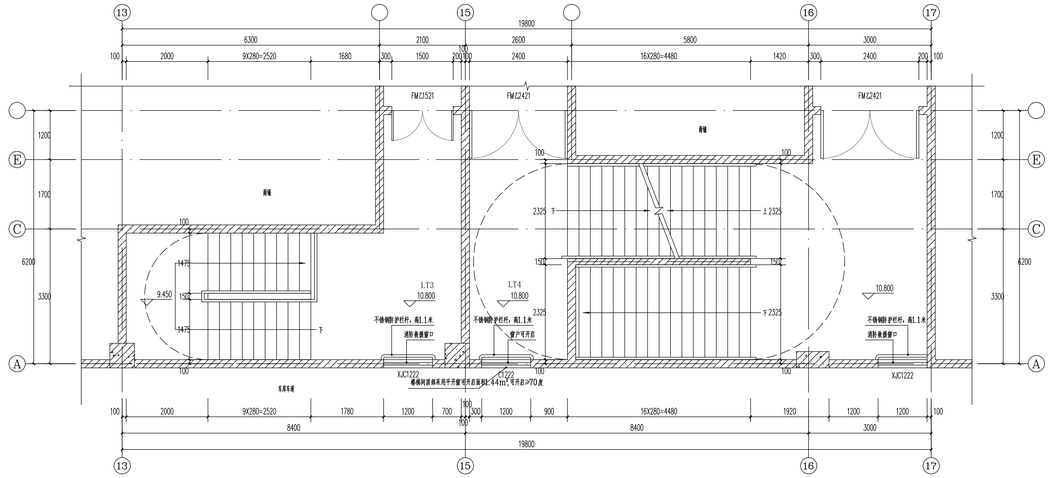

LT3、LT4楼梯间三层平面图 1:50

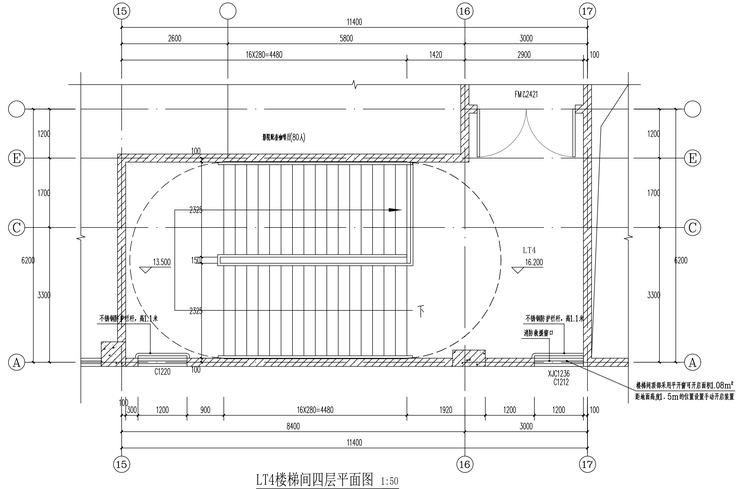

LT4楼梯间四层平面图 1:50

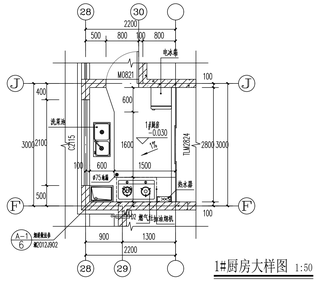

1#厨房大样图 1:50

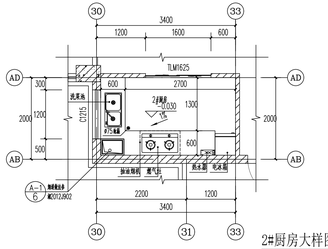

2#厨房大样图 1:50

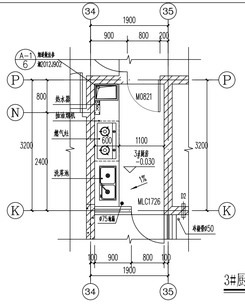

3#厨房大样图 1:50

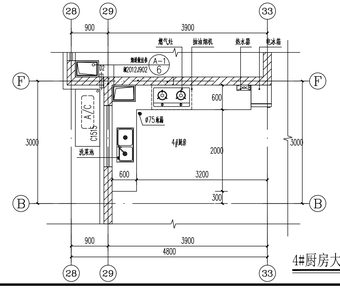

4#厨房大样图 1:50

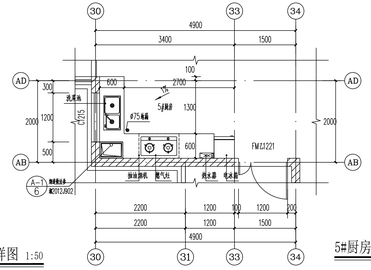

5#厨房大样图 1:50

建设单位/CLIENT:

麻阳苗族自治县远桥房地产开发有限公司

项目名称/PROJECT:

远程国际

子项目名称/SUB-PROJECT:

远程国际

区位图/REGIONAL LOCATION MAP :

广东建筑艺术设计院有限公司
GUANGDONG ARCHITECTURAL ARTISTIC DESIGN INSTITUTE CO.,LTD
■ 建筑工程设计，甲级 ■ 风景园林设计，乙级
■ 城乡规划设计，乙级 ■ 市政设计，乙级

图纸名称/TITLE:

LT3、LT4楼梯间大样图二
厨房大样图

项目名称/PROJECT:

远程国际

设计 DESIGNED	古新辉	
校对 CHECKED	吴新红	
专业负责人 CHIEF	吴志刚	
项目负责人 PROJECT CHIEF	吴志刚	
审核 IDENTIFIED	黄视优	
审定 APPROVED	李 坚	

业务号/JOB NO.

设计阶段/STATUS: 施工图

专业/DISCIPLINE: 建施

比例/SCALE:	1：100	规格/SIZE:	A1

出图日期/DATE: 2021.06

图号/DRAWING NO. JS-31

版次 NO.	修改内容 DESCRIPTION	日期 DATE

条形码/BARCODE:

版权所有，不得复制、抄用。
ALL RIGHTS RESERVED, DON'T COPIED, REPRODUCED.