


①墙身大样四 1:25

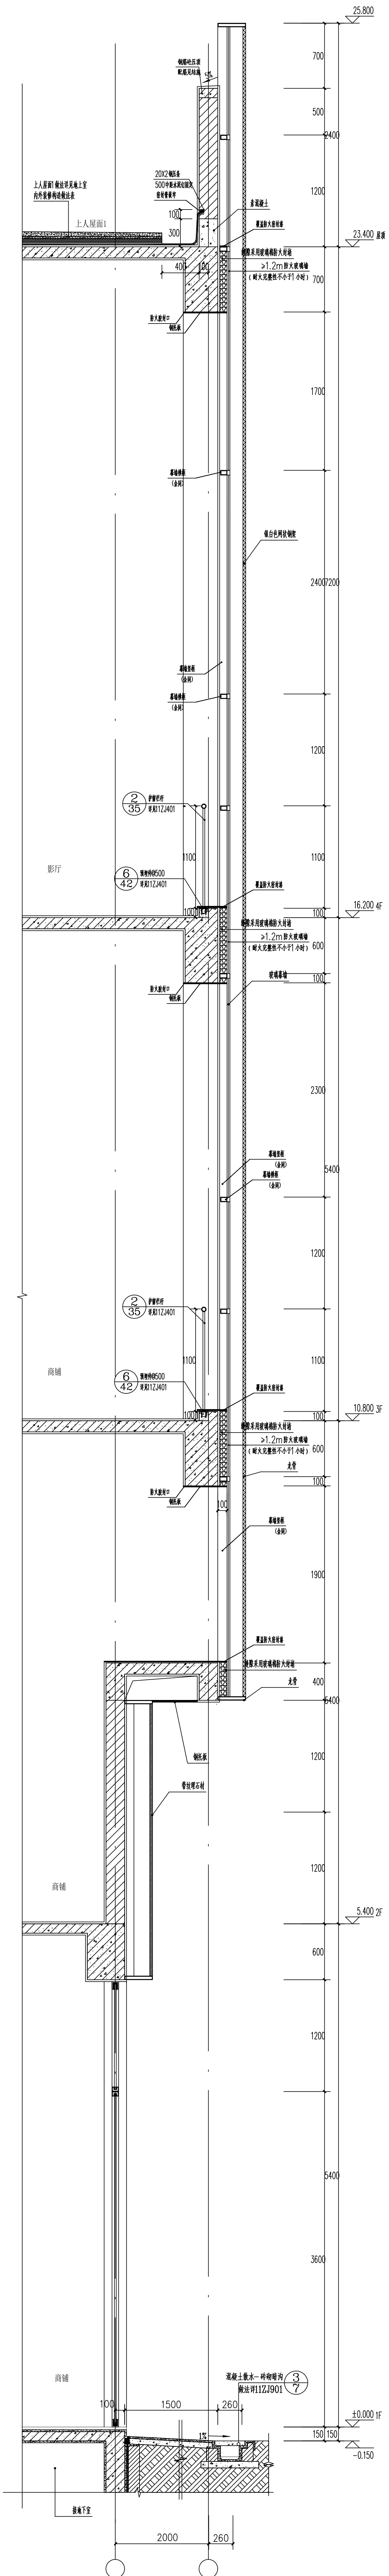

②墙身大样五 1:25

建设单位/CLIENT:		廉阳苗族自治县远拓房地产开发有限公司	
项目名称/PROJECT:		远拓国际	
子项目名称/SUB-PROJECT:		远拓国际	
区域图/REGIONAL LOCATION MAP:			
图例/LEGEND:			
图名/TITLE:		墙身大样图四 墙身大样图五 墙身大样图六	
项目名称/PROJECT:		远拓国际	
设计/DESIGNED:		古新辉	
校对/CHECKED:		吴新红	
专业负责人/PROF.:		吴志刚	
审核/REVIEWED:		黄耀光	
审定/APPROVED:		李坚	
业务号/JOB NO.:		2021.06	
专业/DISCIPLINE:		建筑	
比例/SCALE:		1:100	
出图日期/DATE:		2021.06	
图号/DRAWING NO.:		JS-37	
修改内容/REVISION:		日期	
NO.:		DATE	
条形码/BARCODE:			
版权所有, 不得复制或再行使用。		ALL RIGHTS RESERVED. DON'T COPY, REPRODUCE.	