



①墙身大样六 1:25

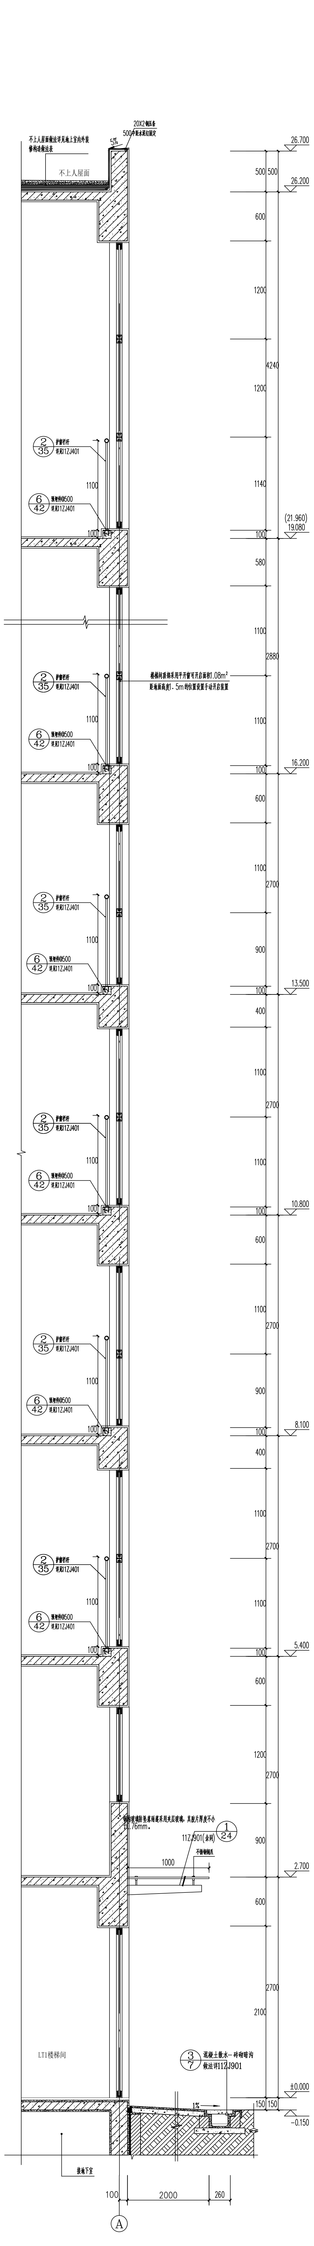

②墙身大样七 1:25

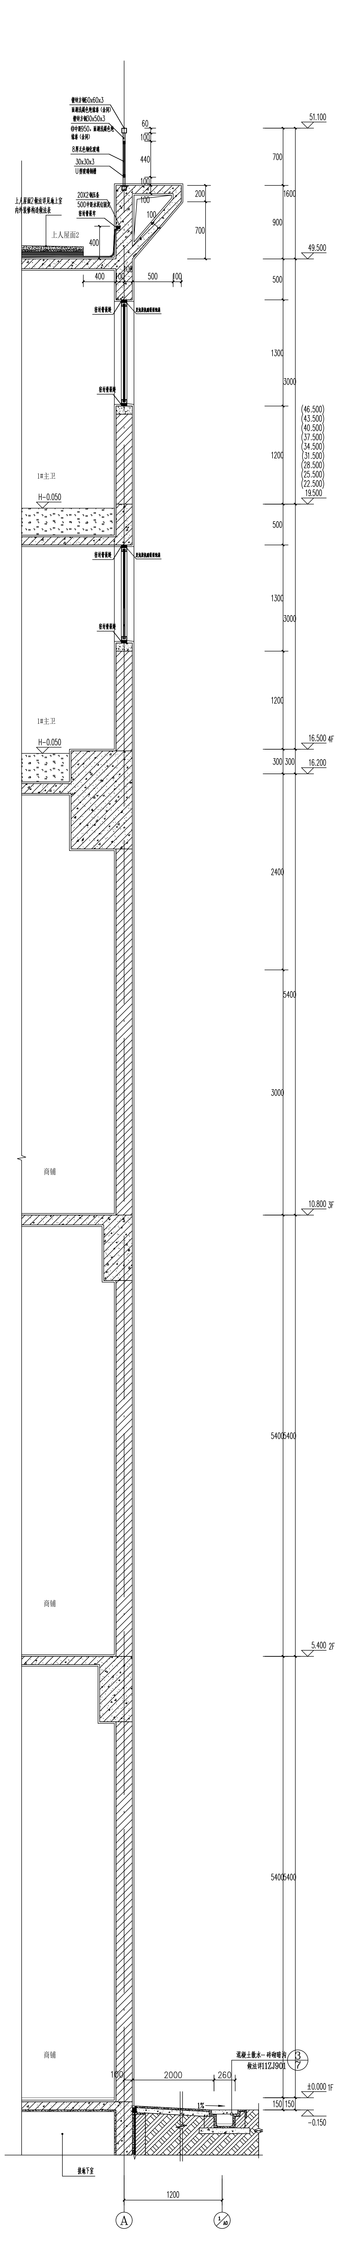

③墙身大样八 1:25

建设单位/CLIENT:	麻阳苗族自治县运怀房地产开发有限公司
项目名称/PROJECT:	远程国际
子项目名称/SUB-PROJECT:	远程国际
区位图/REGIONAL LOCATION MAP:	
墙身大样图六、七、八 图纸名称/DRAWING TITLE: 墙身大样图六、七、八	
项目名称/PROJECT: 远程国际	

广东建筑艺术设计院有限公司
GUANGDONG ARCHITECTURAL ART DESIGN INSTITUTE CO.,LTD.

设计/DESIGNED	古振辉	
校对/CHECKED	吴丽红	
专业负责人/CHIEF	吴志刚	
项目负责人/PROJECT CHIEF	吴志刚	
审核/DIRECTIFIED	黄佩伦	
审定/APPROVED	李 军	

业务号/JOB NO.	
设计阶段/STATUS:	施工图
专业/DISCIPLINE:	建施
比例/SCALE:	1: 100
规格/SIZE:	A1
图号/DRAWING NO.	JS-38
出图日期/DATE:	2021.06

NO.	DESCRIPTION	DATE
	修改内容	日期

条形码/BARCODE:

ALL RIGHTS RESERVED. COPYRIGHT © 版权所有，未经书面许可，不得以任何方式使用。