
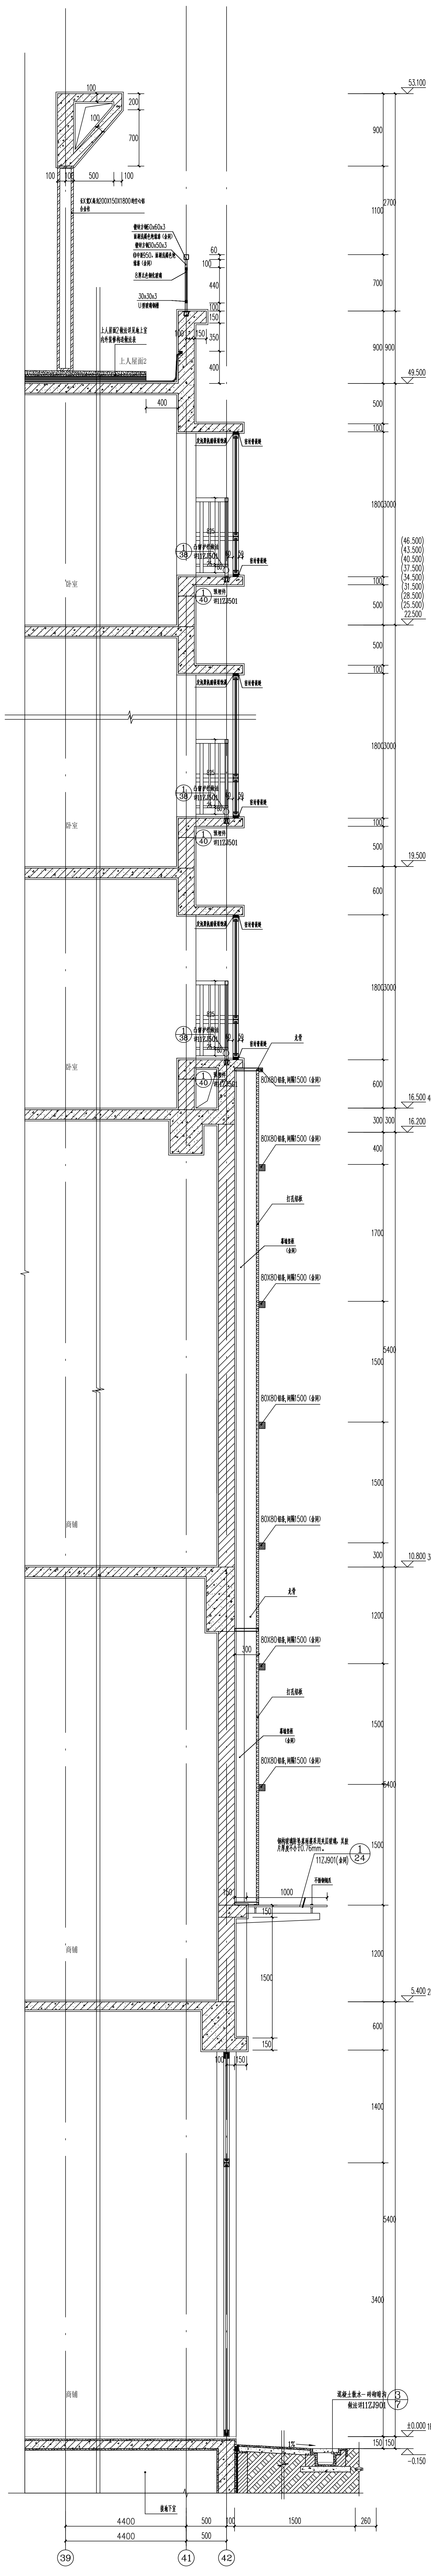


① 墙身大样九 1:25

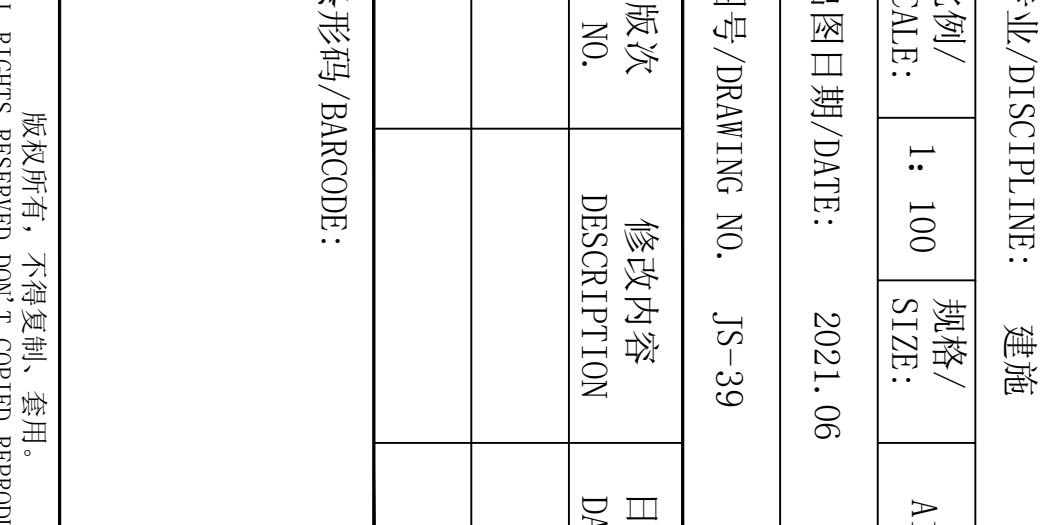

② 墙身大样十 1:25

建设单位/CLIENT:		建设地点/CLIENT:	
南京浦口南京浦口远拓房地产开发有限公司		南京浦口南京浦口远拓房地产开发有限公司	
项目名称/PROJECT:		项目名称/PROJECT:	
远拓国际		远拓国际	
子项目名称/SUB-PROJECT:		子项目名称/SUB-PROJECT:	
远拓国际		远拓国际	
区位图/REGIONAL LOCATION MAP:		区位图/REGIONAL LOCATION MAP:	
			
设计/DESIGNED:		设计/DESIGNED:	
校核/CHECKED:		校核/CHECKED:	
项目负责人/PROJECT CHIEF:		项目负责人/PROJECT CHIEF:	
审核/REVIEWED:		审核/REVIEWED:	
审定/CONFIRMED:		审定/CONFIRMED:	
业务号/JOB NO.:		业务号/JOB NO.:	
设计阶段/STATUS:		设计阶段/STATUS:	
专业/DISCIPLINE:		专业/DISCIPLINE:	
比例/SCALE:		比例/SCALE:	
1:100		1:100	
图号/DRAWING NO.:		图号/DRAWING NO.:	
JS-39		JS-39	
版次/NO.:		版次/NO.:	
修改内容/DESCRIPTION:		修改内容/DESCRIPTION:	
日期/DATE:		日期/DATE:	
条形码/BARCODE:		条形码/BARCODE:	
版权所有, 不得复制或商用。		版权所有, 不得复制或商用。	
ALL RIGHTS RESERVED. ANY COPIES, REPRODUCTION,		ALL RIGHTS RESERVED. ANY COPIES, REPRODUCTION,	