
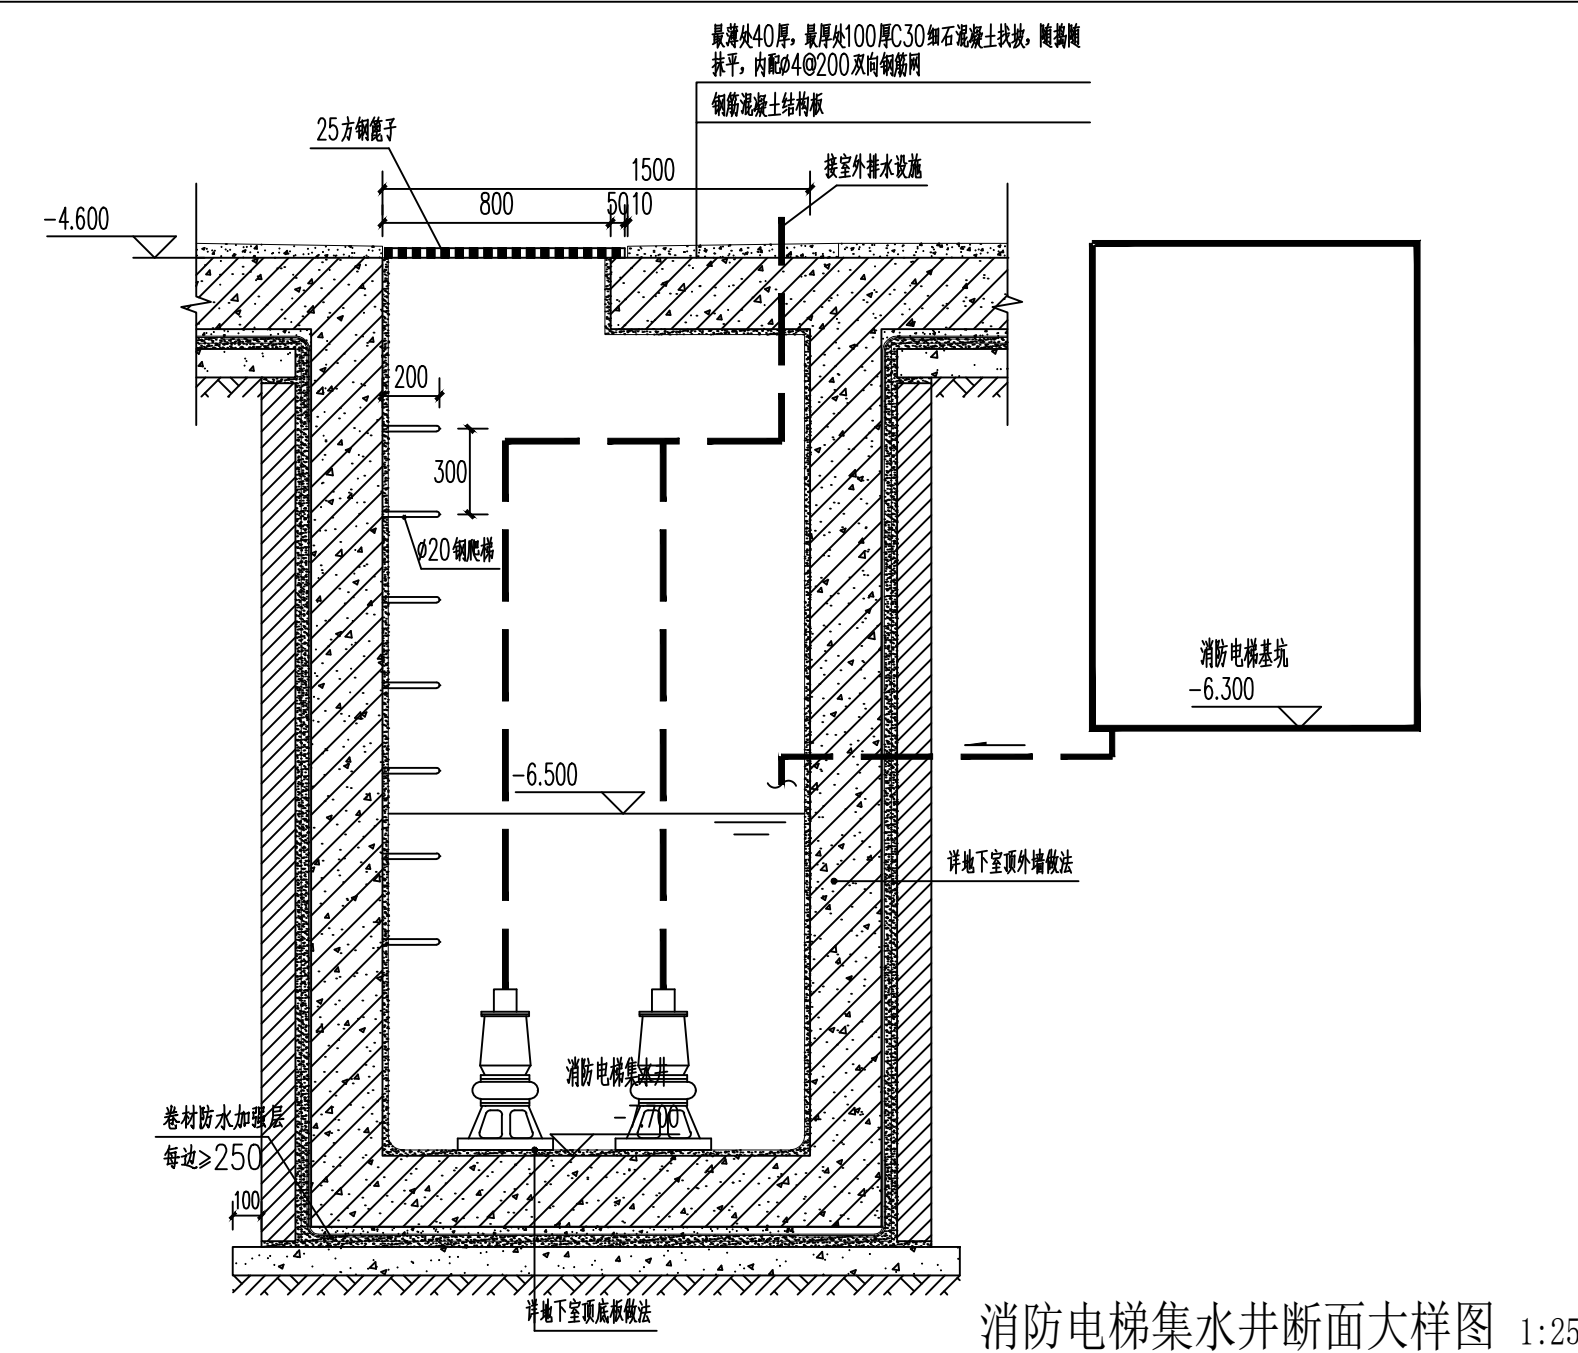
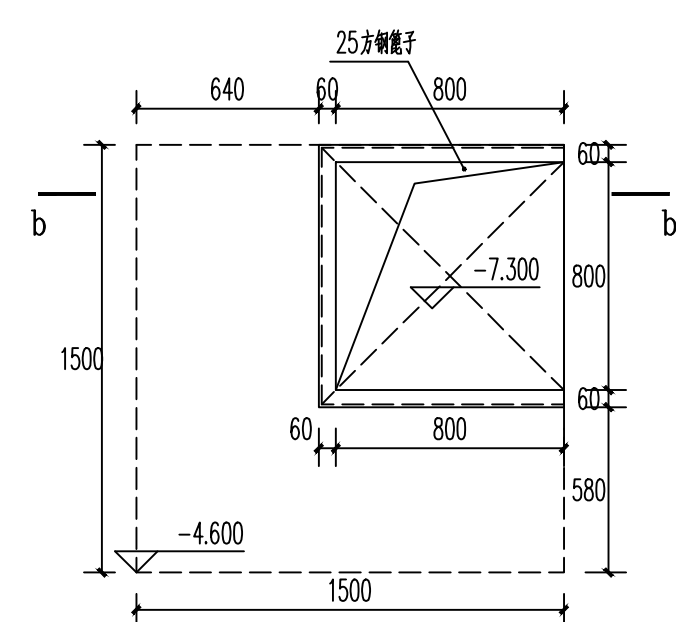
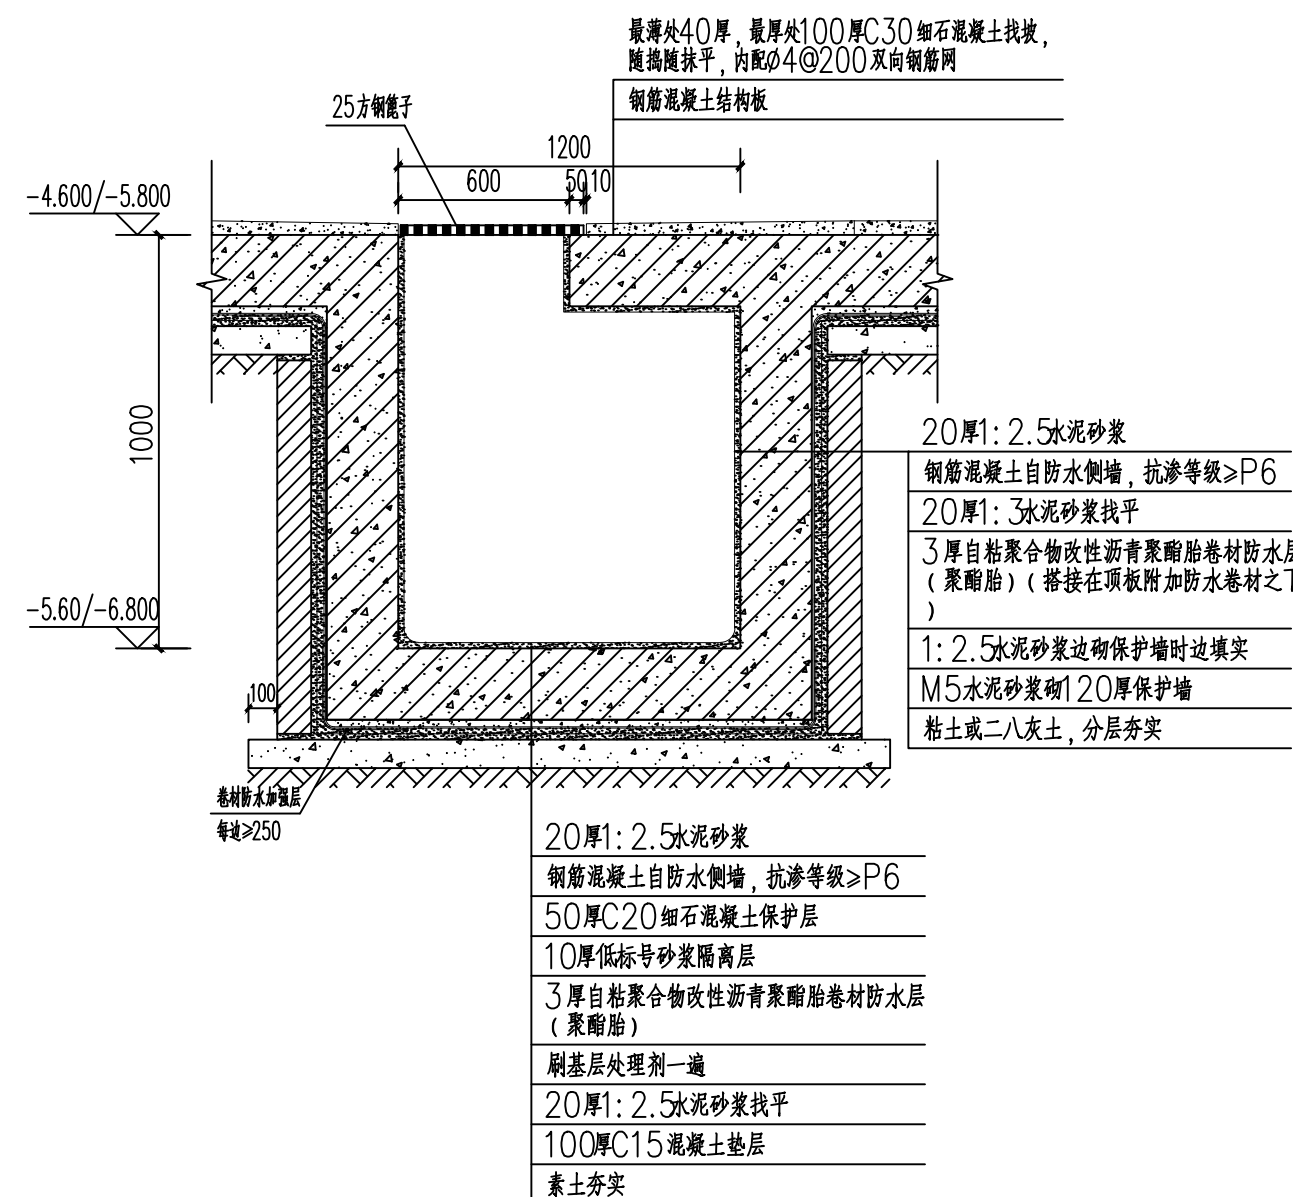
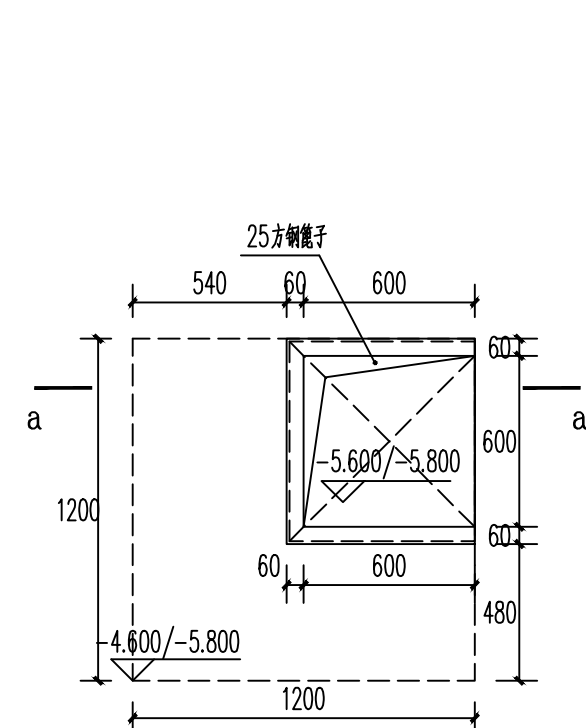
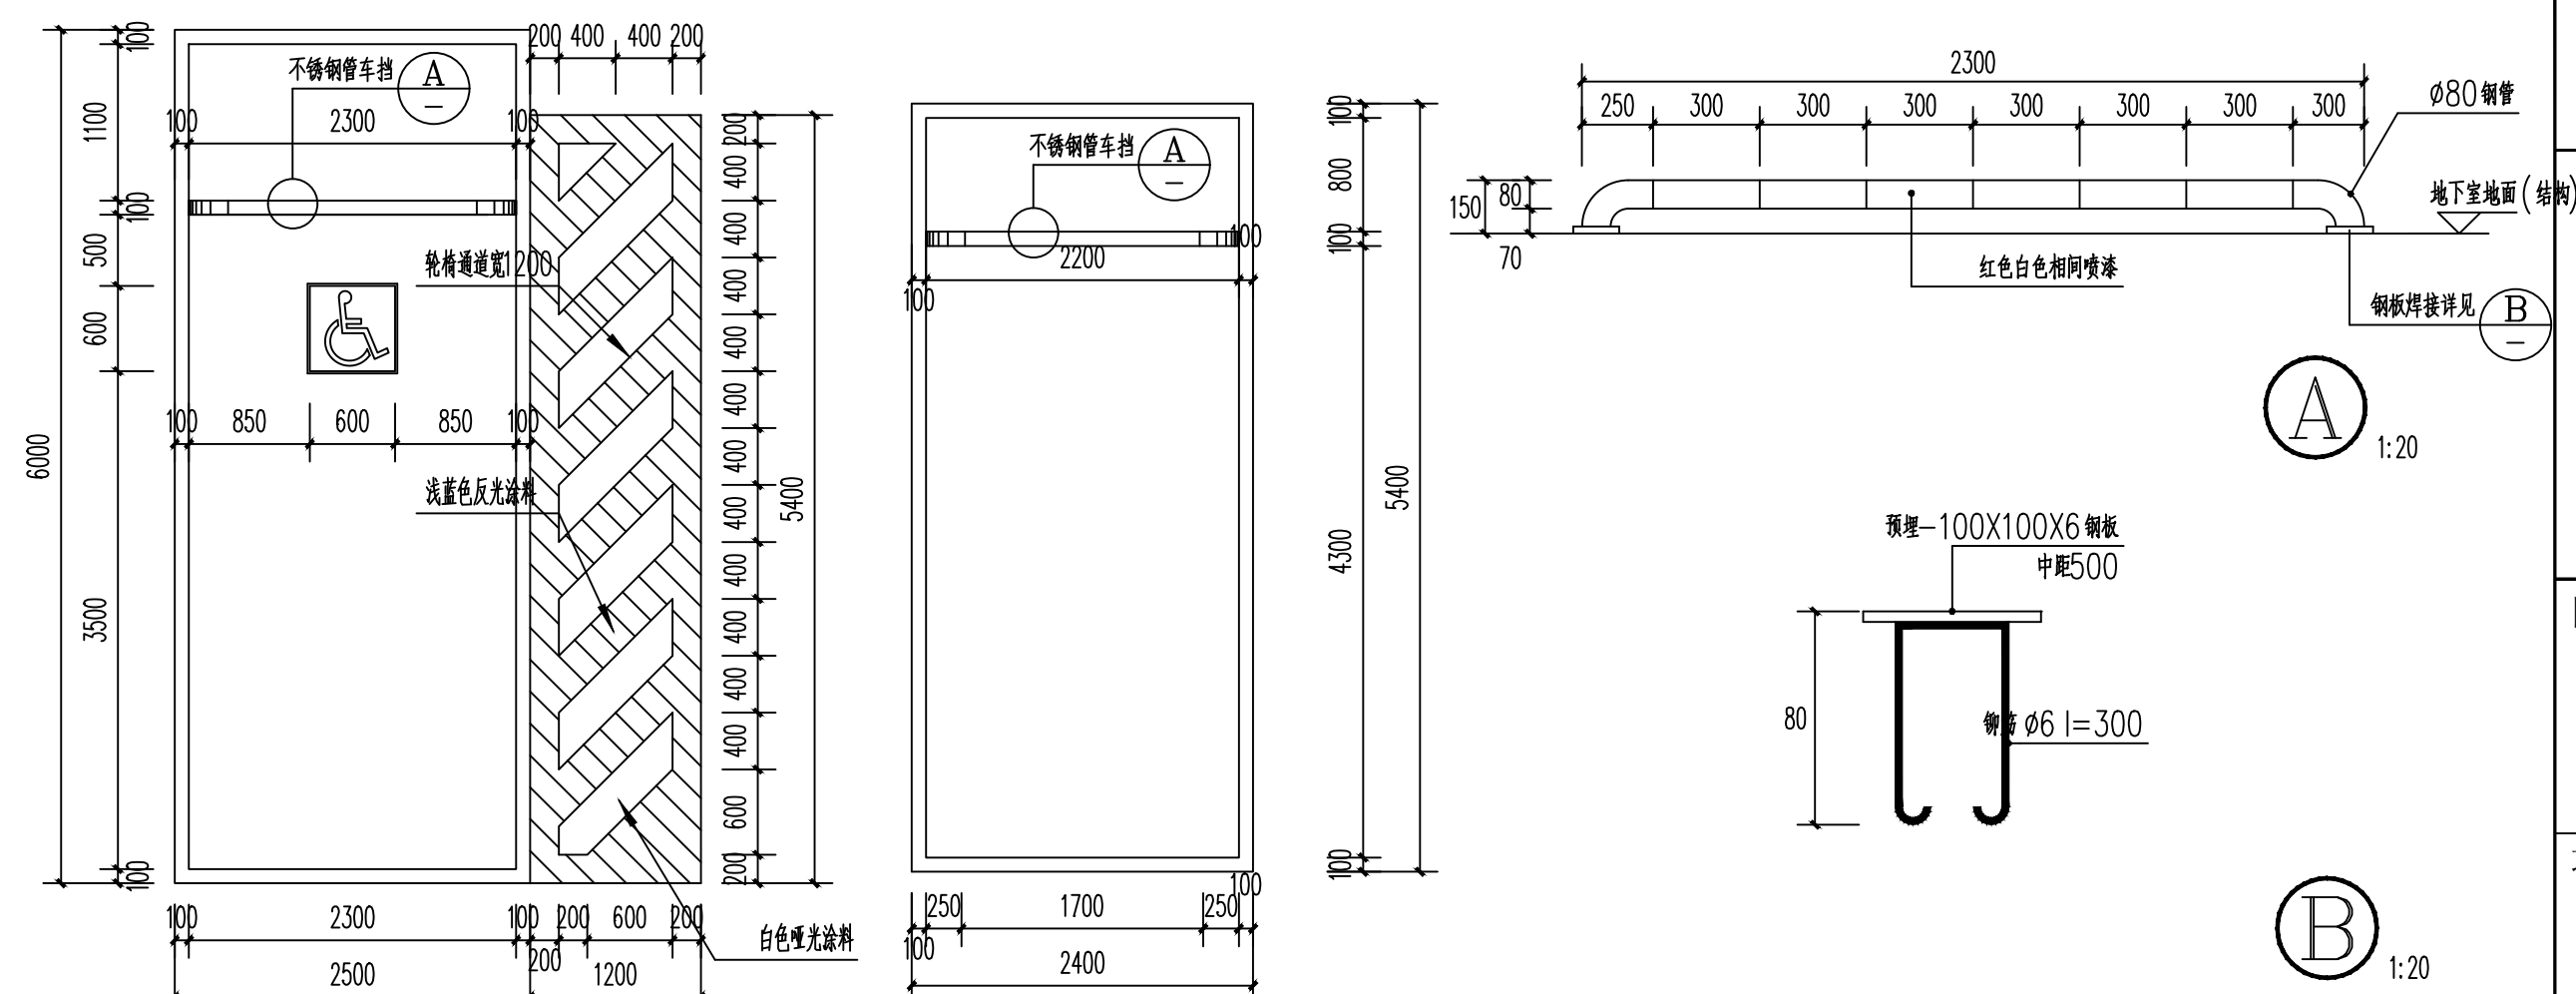
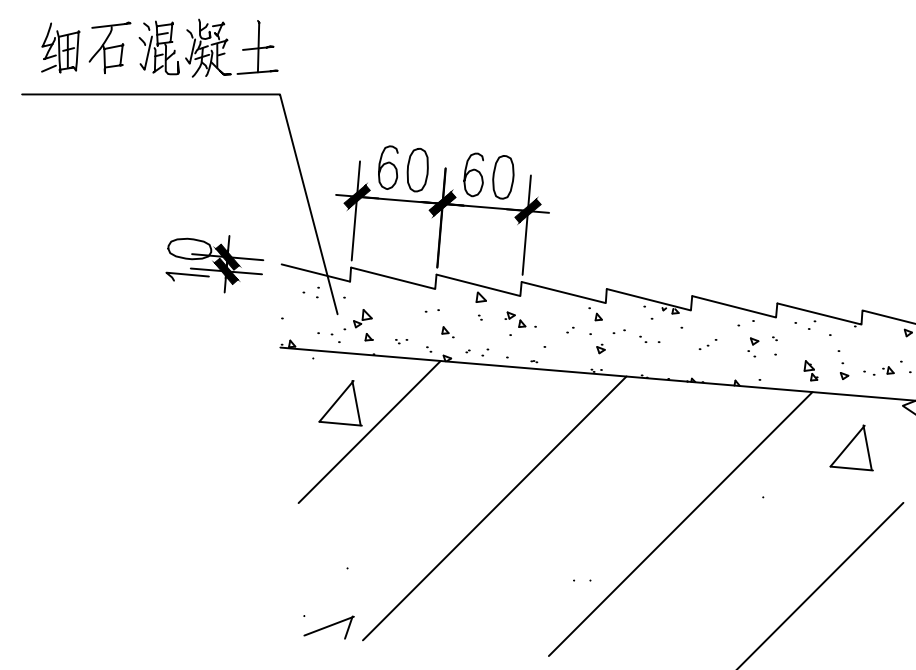
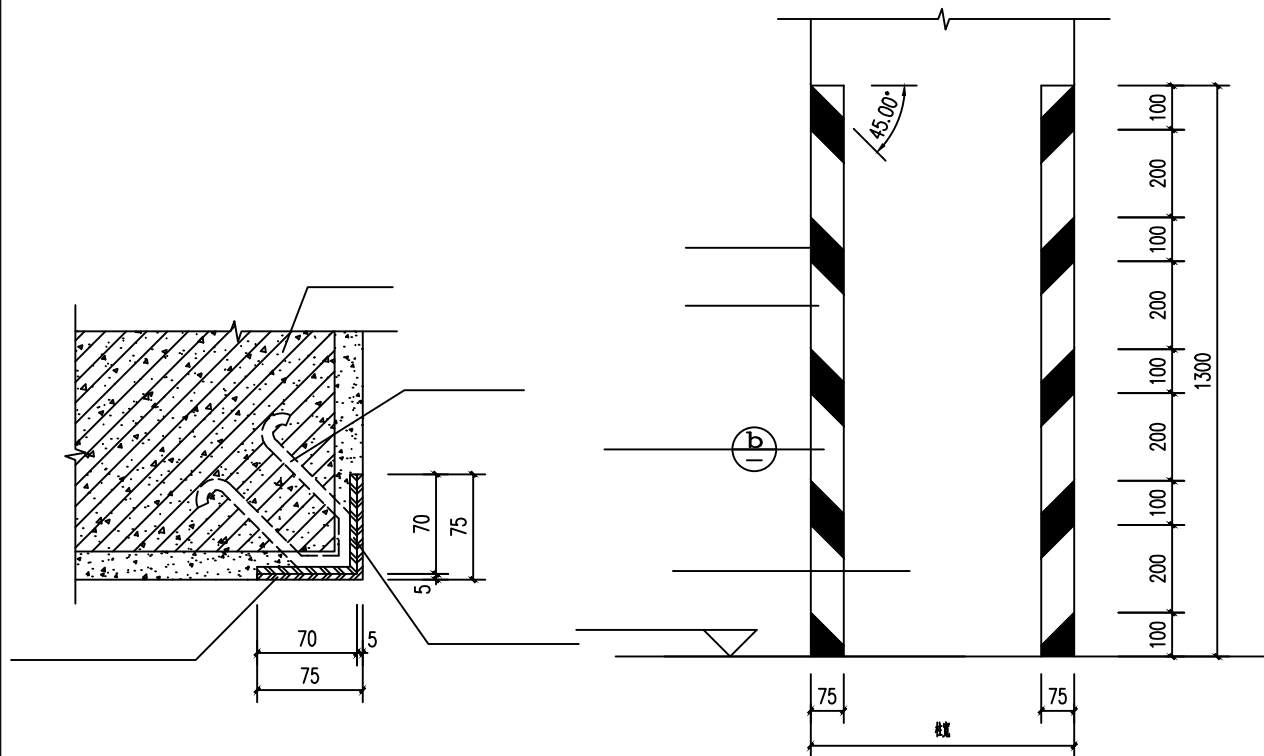
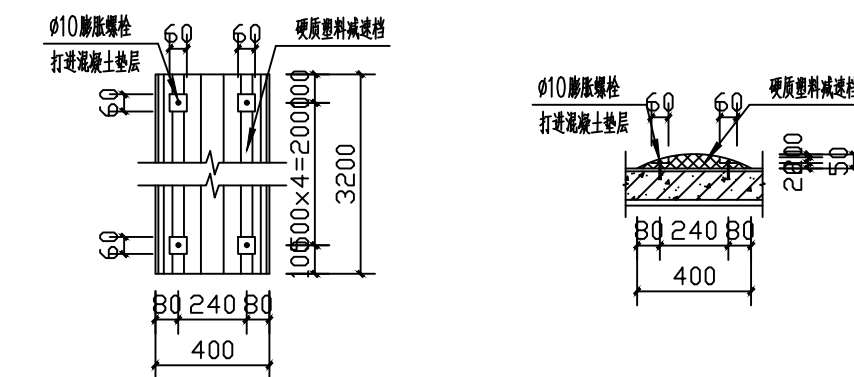
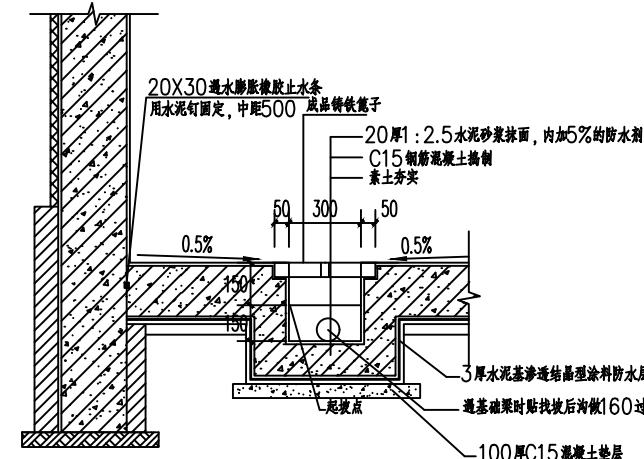
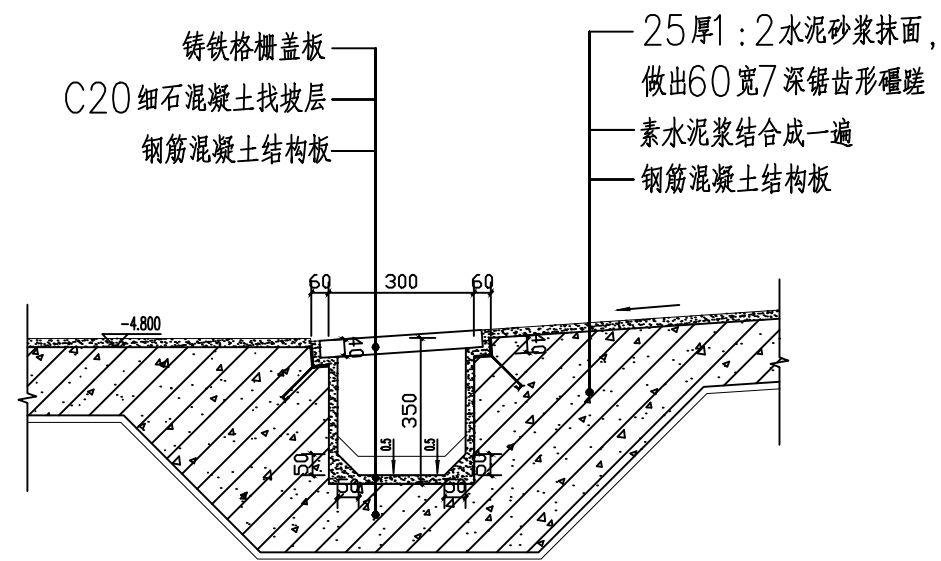


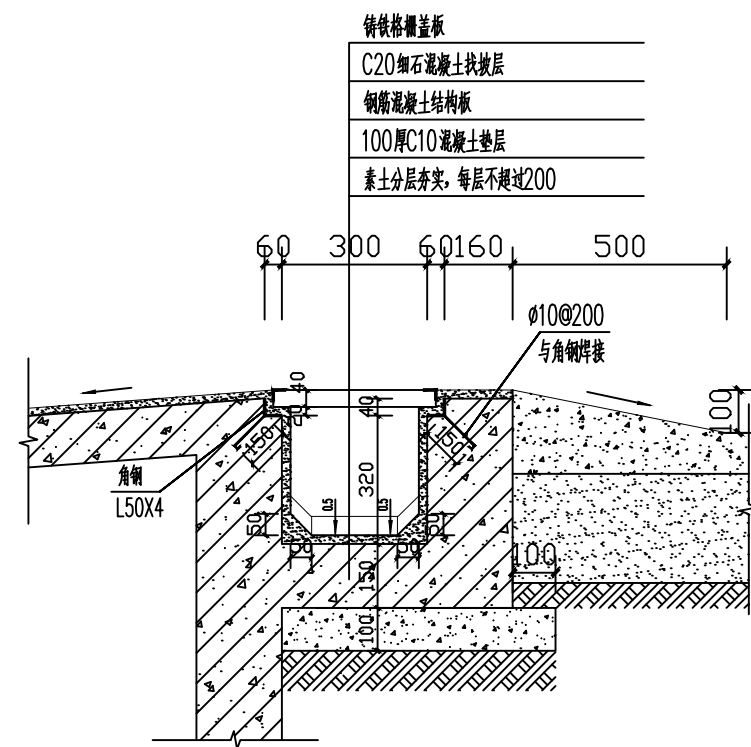

建设单位/CLIENT:	麻阳苗族自治县远桥房地产开发有限公司
项目名称/PROJECT:	远程国际

子项目名称/SUB-PROJECT:
远程国际

区位图/REGIONAL LOCATION MAP :

广东建筑艺术设计院有限公司


GUANGDONG ARCHITECTURAL ARTISTIC DESIGN INSTITUTE CO.,LTD

- 建筑方案设计：甲级
- 风景园林设计：乙级
- 城乡规划设计：乙级
- 市政设计：乙级

图纸名称/TITLE: 节点大样图二
--

项目名称/PROJECT:

远程国际

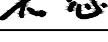设计 DESIGNED	古新辉	
校对 CHECKED	吴新红	
专业负责人 CHIEF	吴志刚	
项目负责人 PROJECT CHIEF	吴志刚	
审核 IDENTIFIED	黄履优	
审定 APPROVED	李 坚	

任务号/JOB NO.			
设计阶段/STATUS: 施工图			
专业/DISCIPLINE: 建筑			
比例/ SCALE:	1: 100	规格/ SIZE:	A1
出图日期/DATE:		2021. 06	
图号/DRAWING NO. JS-41			
版次 NO.	修改内容 DESCRIPTION		日期 DATE

条形码/BARCODE:

版权所有，不得复制、套用。
ALL RIGHTS RESERVED, DON'T COPIED, REPRODUCED.