
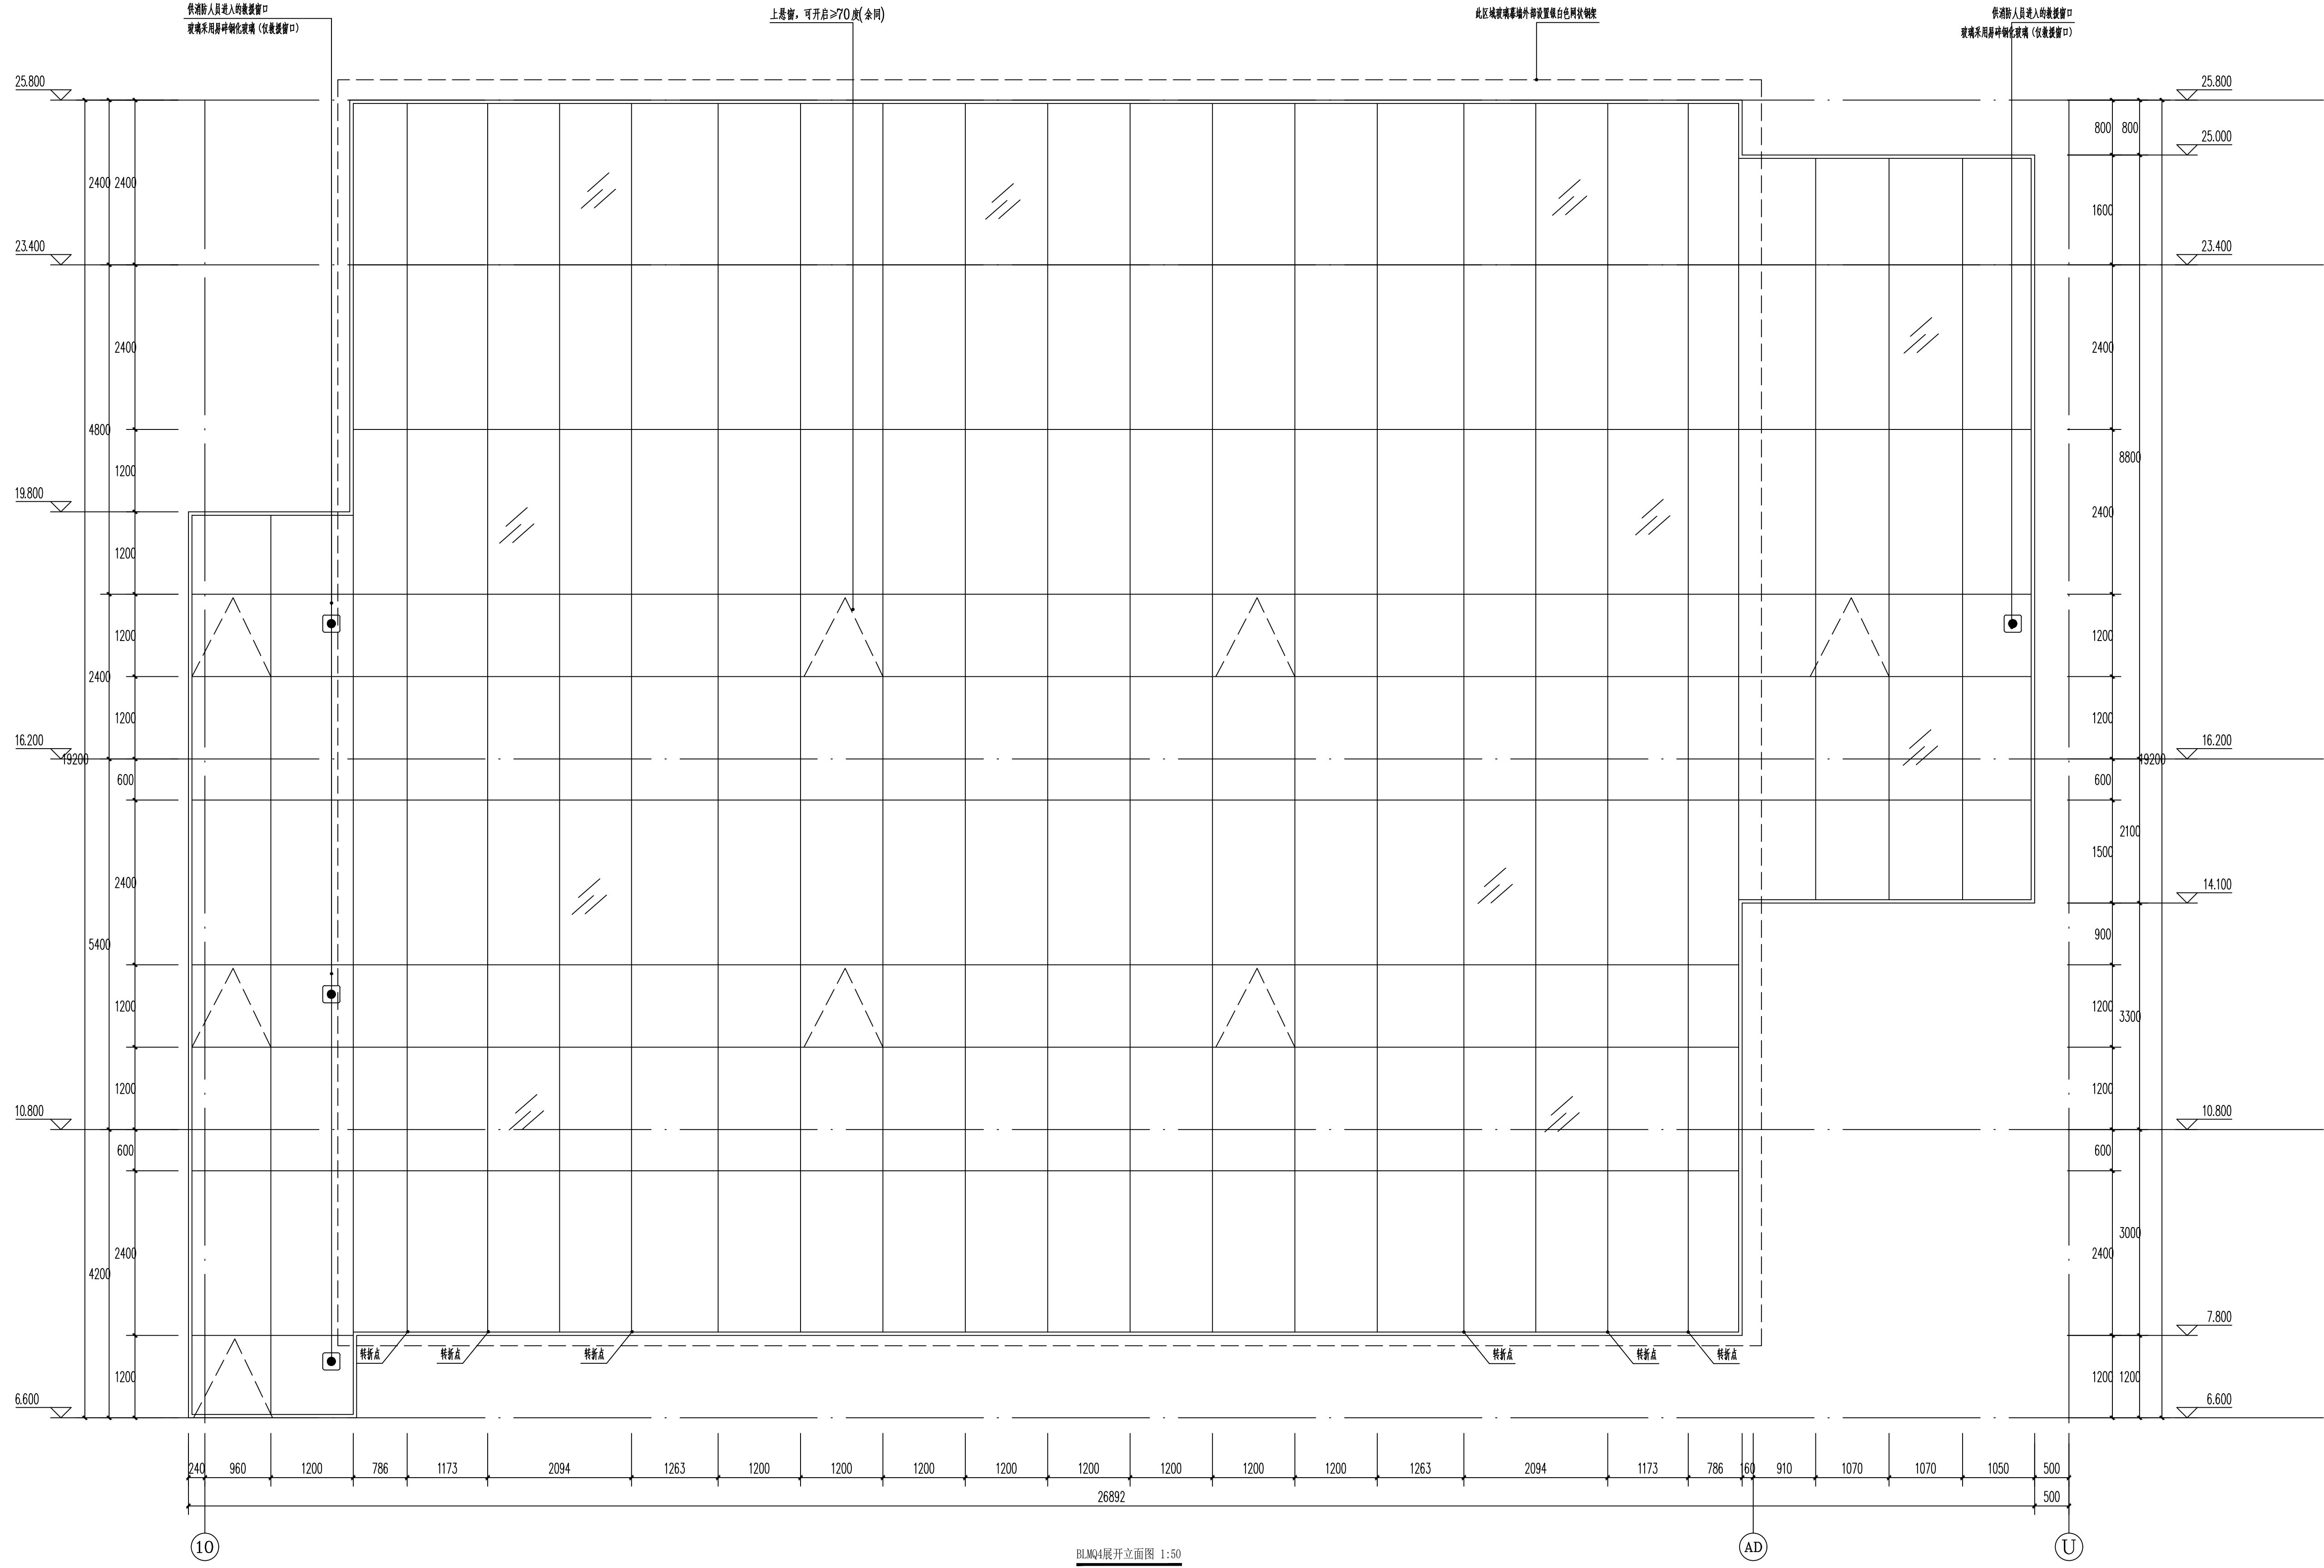


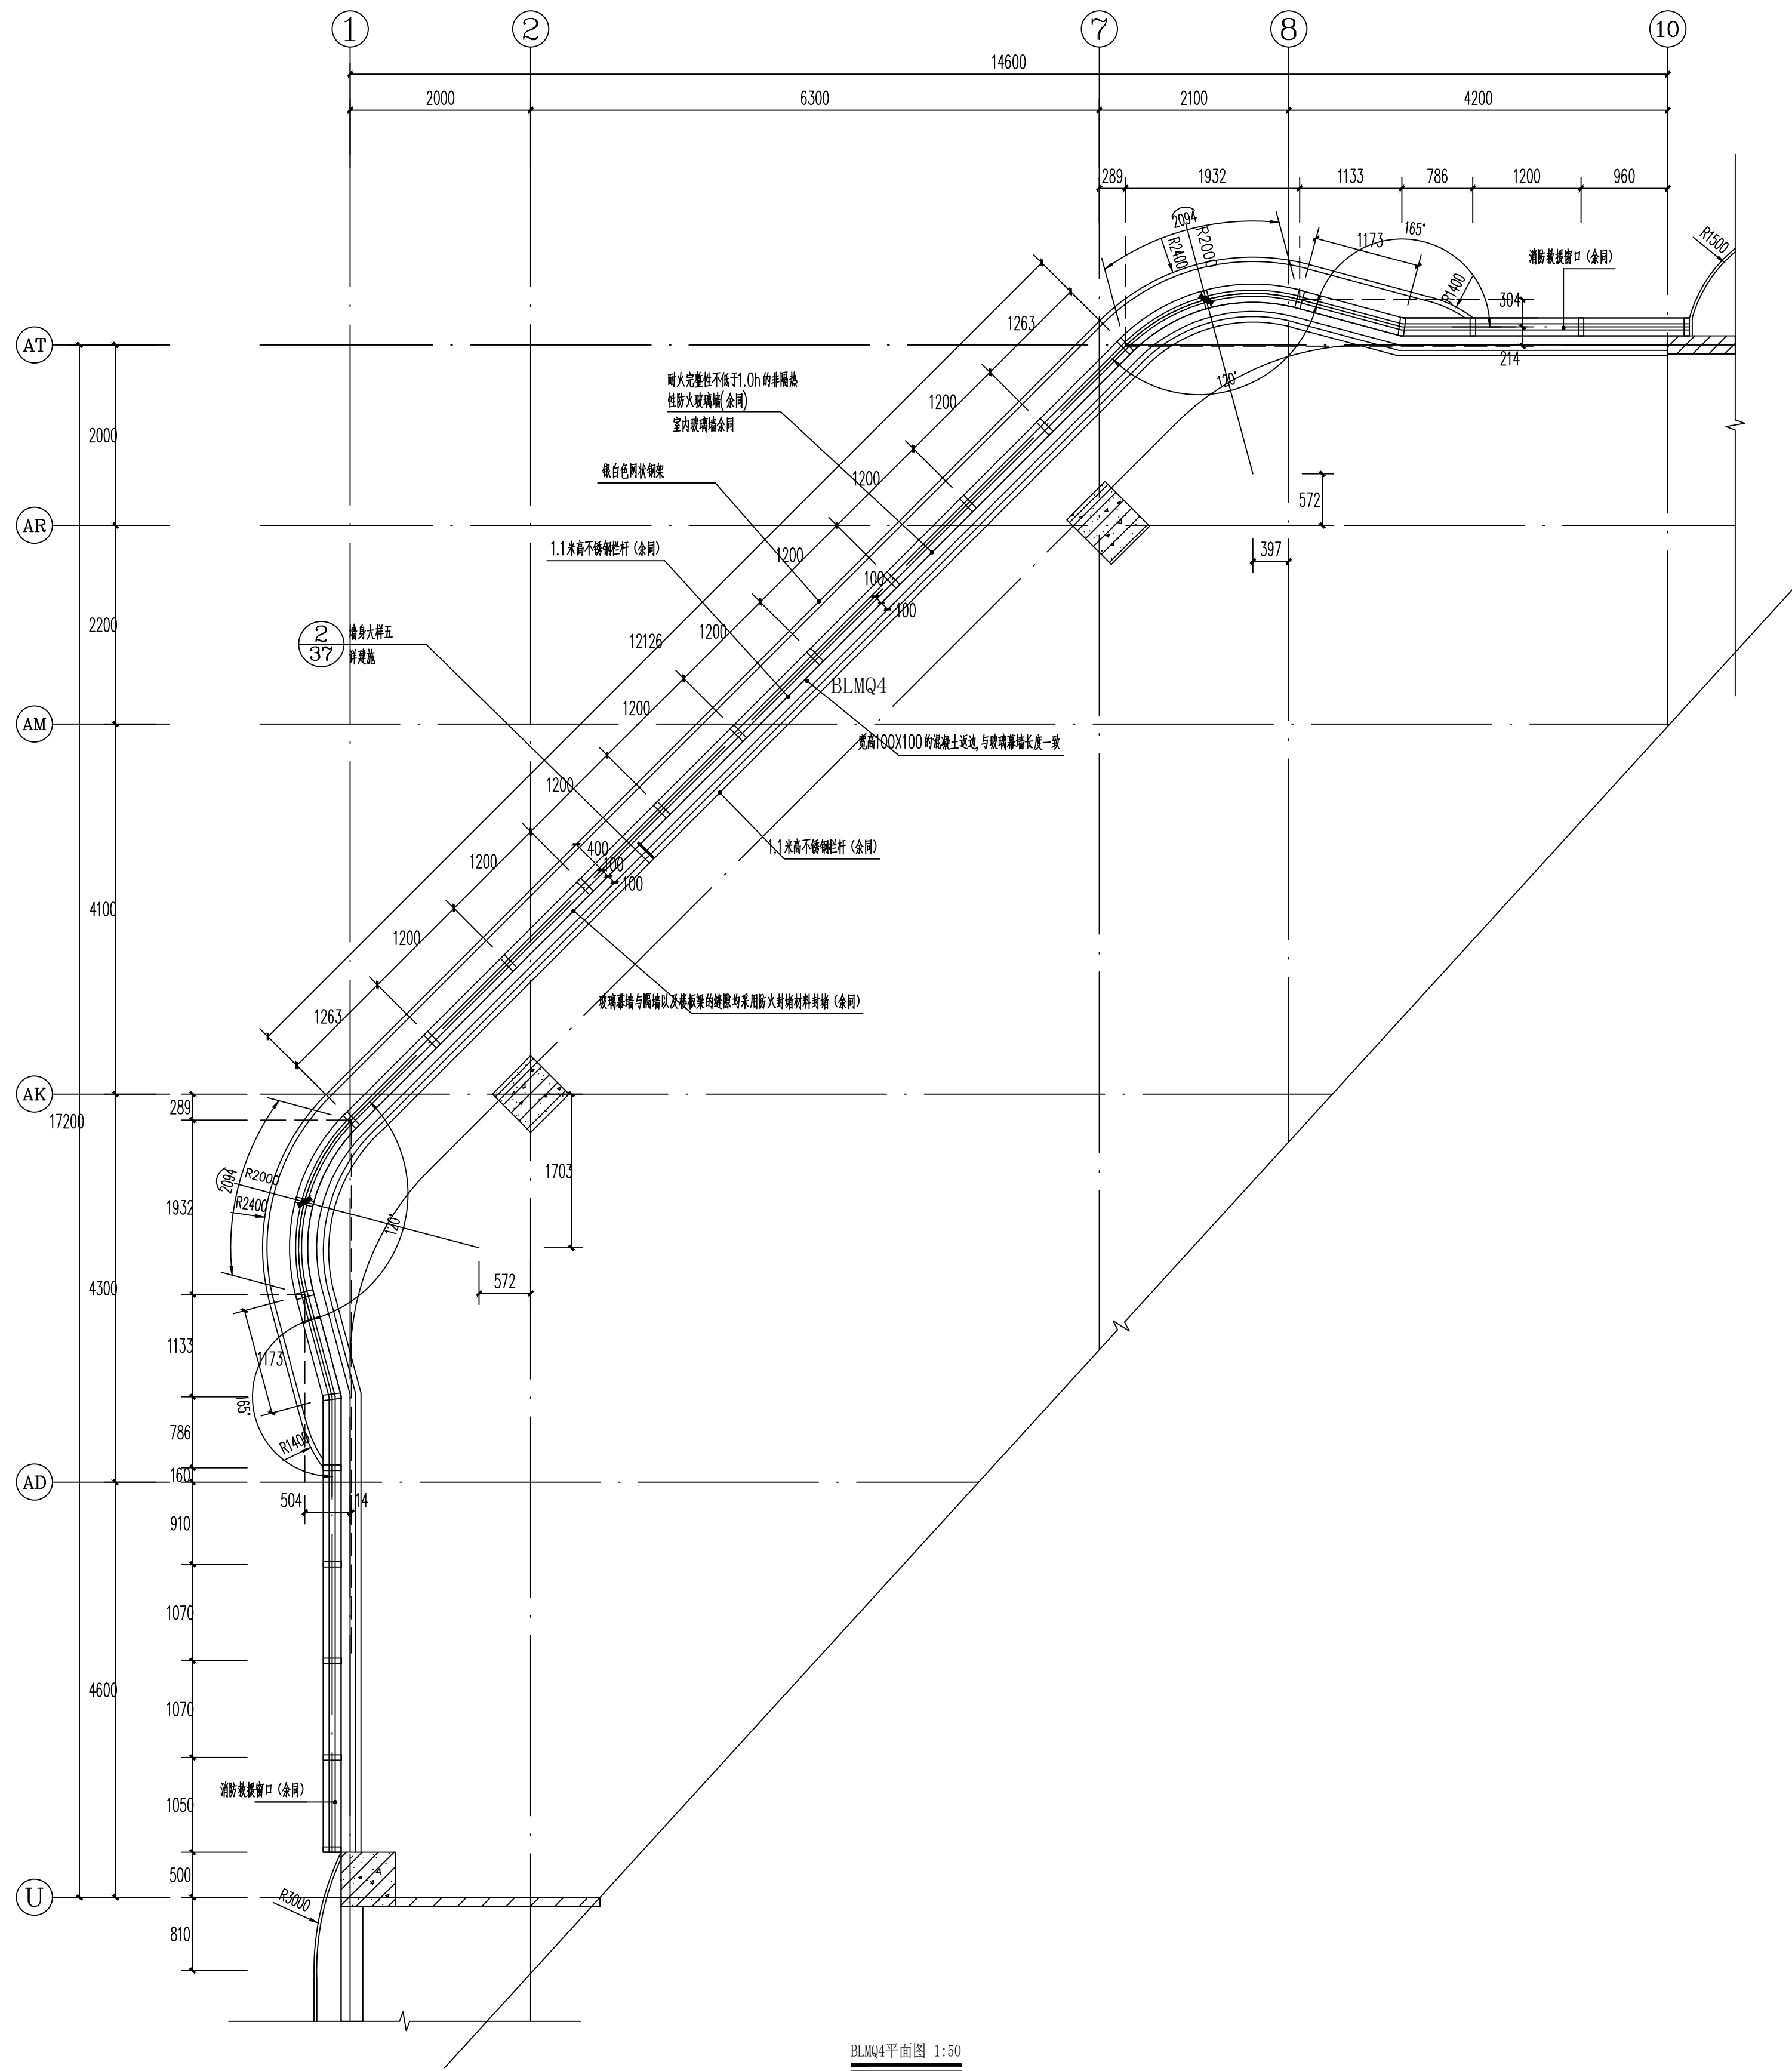

建设单位/CLIENT:

麻阳苗族自治县远桥房地产开发有限公司

项目名称/PROJECT:

远程国际

子项目名称/SUB-PROJECT:

远程国际

区位图/REGIONAL LOCATION MAP :



图纸名称/TITLE:

玻璃幕墙大样图二

项目名称/PROJECT:

远程国际

设计
DESIGNED

古新辉

校对
CHECKED

吴新红

专业负责人
CHIEF

吴志刚

项目负责人
PROJECT CHIEF

吴志刚

审核
IDENTIFIED

黄展优

审定
APPROVED

李 坚

业务号/JOB NO.

设计阶段/STATUS: 施工图

专业/DISCIPLINE: 建筑

比例/
SCALE: 1: 100

规格/
SIZE: A1

出图日期/DATE: 2021. 06

图号/DRAWING NO. JS-44

版次
NO.

修改内容
DESCRIPTION

日期
DATE

条形码/BARCODE:

版权所有，不得复制、套用。
ALL RIGHTS RESERVED, DON'T COPIED, REPRODUCED.