


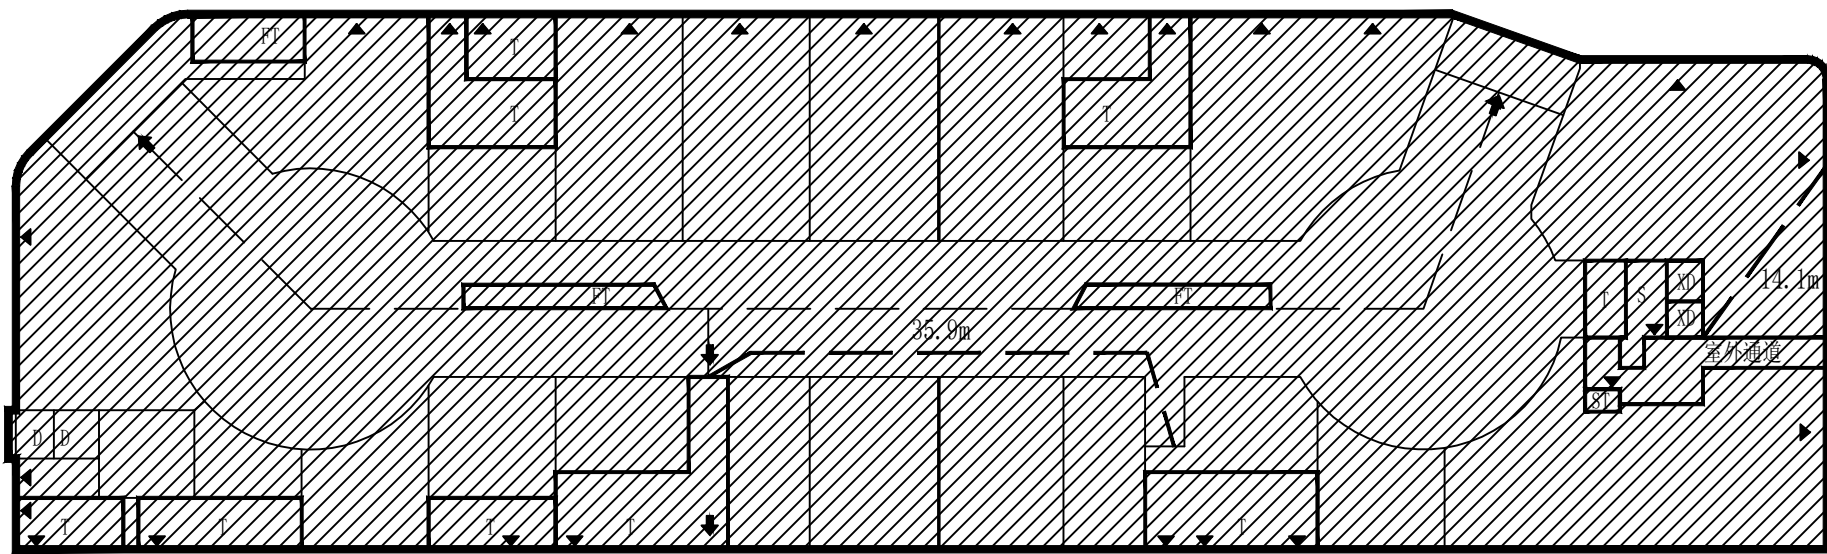

一层防火分区示意图 1:500


注：一层商场设置自动喷淋灭火系统
 本层为一个防火分区，防火分区面积为4129.28㎡，共有3个安全出口。
 房间内最远点至最近安全出口的距离为14.1m≤27.5m，最远疏散门至最近安全出口的距离为35.9m(≤37.5m)，满足规范要求。
 本层需要的疏散宽度为3692.11X0.43X1/100=15.87m(计算疏散宽度的面积是减掉一层所有楼梯间面积后的净面积)
 本层设计的疏散宽度为7.2X2+2.4=16.80m，满足规范要求。

一层平面图 1:150

本层建筑面积: 4129.28m²
总建筑面积: 22985.06m²
计容总建筑面积: 18157.36m²
不计容总建筑面积: 4827.70m²

图例

 灰砂加气混凝土砌块 (商铺隔墙)
 消火栓

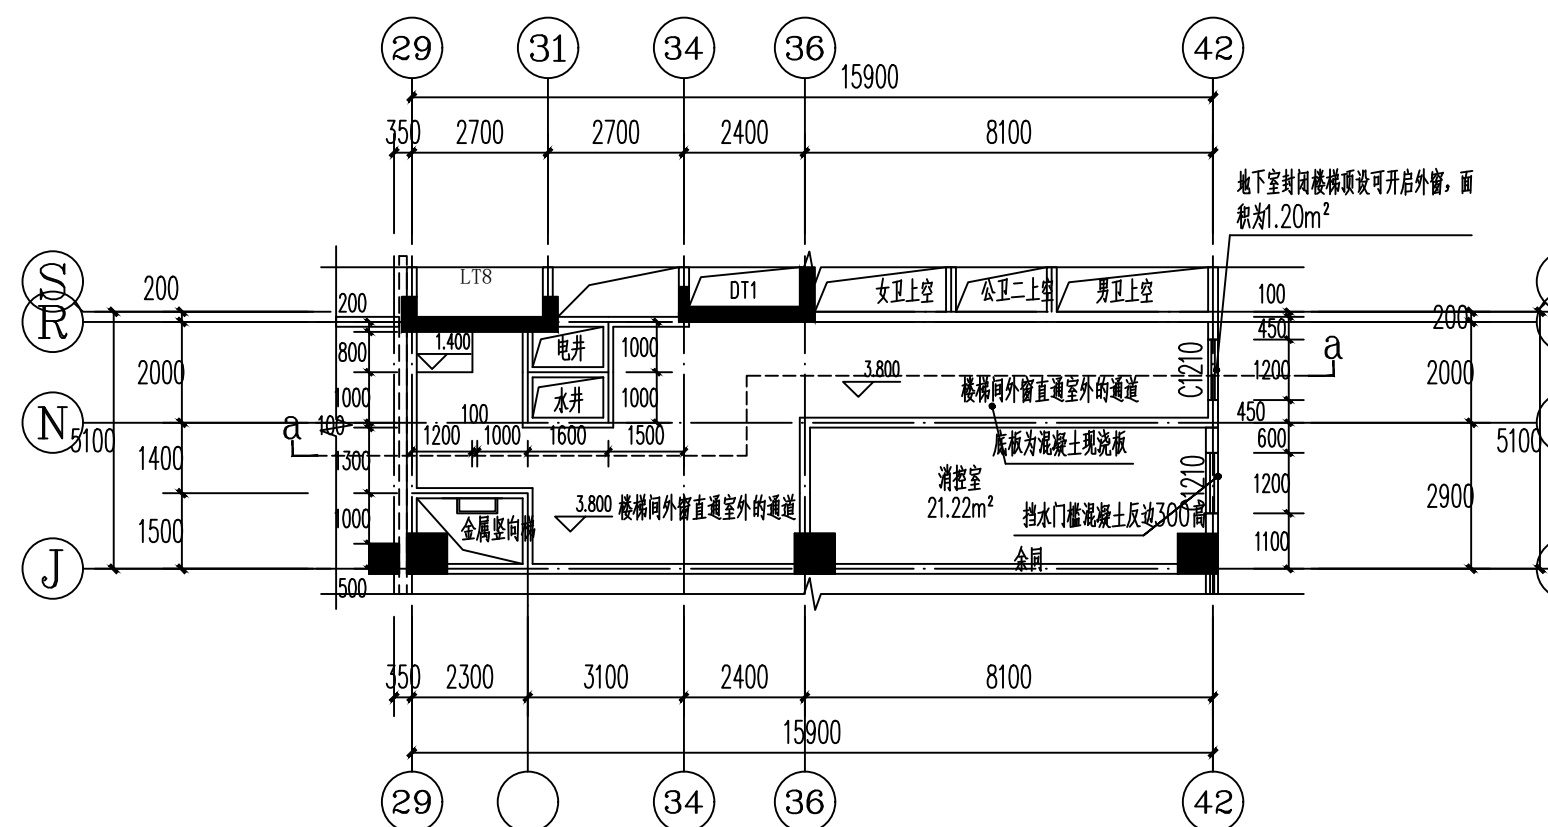

室外通道夹层平面图 1:150 注: a-a剖面图详IS-25

注明：

1. 柱布置于评估范围内。
2. 除图中注明者外,门窗前测定的墙垛均为100mm或平柱、墙垛、墙中安装。
3. 本工程以外墙厚度均为240厚钢筋混凝土加加气混凝土砌块,墙垛外墙厚度为100厚,内墙为40厚。
4. 钢筋混凝土墙垛除特殊注明外均为100厚灰加气混凝土砌块,其他墙垛均为240厚烧页岩多孔砖。
5. 窗台标高小于900mm时,作防护栏杆具体做法详见17J401  安全防护要符合安全防护要求,以防止人员坠落。
6. 各种设备布置、管架、管进及埋件等具体做法同时参照专业标准、规范实施。
7. 本建筑设自动喷淋灭火系统,消防栓位置见水施。
8. 管架进及设备间或隔火墙进道的房间,门下方设300高200宽混凝土门槛,宽度同门宽。
9. 除注外,卫生间、厕所地面标高均±1-0.05;卫生间前室走廊地面标高均±1-0.03。以±1.2为地漏高,(H为楼面标高),详见卫生专业大图。
10. 所有外墙外窗、门更宜设置玻璃门玻璃幕墙。
11. 无端窗洞口宽应小于相应墙面宽(面宽)±5mm,并应有坡度设置,具体详见卫生专业大图。
12. 外墙窗洞宽为J1111-(A-7)-2m,外墙门洞宽为J1111-(A-4)-9,地面变形缝为J1111-(A-7)-2,楼面变形缝为J1111-(A-8)-1。
13. 人行步道上口宽为72±mm上的洞口做结构板面,其他地方洞口宽为21±mm做结构板面,0.76mm厚双层钢化夹胶玻璃。
14. 玻璃幕墙洞口宽度不宜大于1.0mX1.0m,下沿窗台距地不大于1.2m,门宽不大于2.0m,采取单扇玻璃,并应设置可安全拆卸的限位块,详见平面、立面图。
15. 4.玻璃门洞口宽为100X2200,窗宽100X700X2200的防火玻璃不应低于1.00h,幕墙、窗框按±1.700。D3观光电梯梯内设防护栏杆。
16. 玻璃自吸通风扇,每台风扇可开启百叶窗面积不大于1.0㎡,开启面积不大于三层。
17. 楼层与室外露台门洞口宽为800mm,门洞宽不得,在玻璃窗内设置通风扇,通风高度为800,减小噪音。
18. 公共楼梯,当楼梯净宽为4.2m时,必须采取防止人员坠落的安全措施;住宅楼梯,楼梯净宽为4.11m时,必须采取防止人员坠落的安全措施。
19. 儿童游乐区顶棚尺寸及位置与设备专业图纸冲突时以专业图纸为准。

[illegible]