

麻阳苗族自治县远桥房地产开发有限公司

远程国际

远程国际

律苑國際

GUANGDONG ARCHITECTURAL ARTISTIC DESIGN INSTITUTE CO.,LTD

二层平面图

设计
DESIGNED

专业负责人 CHIEF	吴志刚	吴志刚
----------------	-----	-----

审核 IDENTIFIED	黄履优	
------------------	-----	---

业务号/JOB NO.

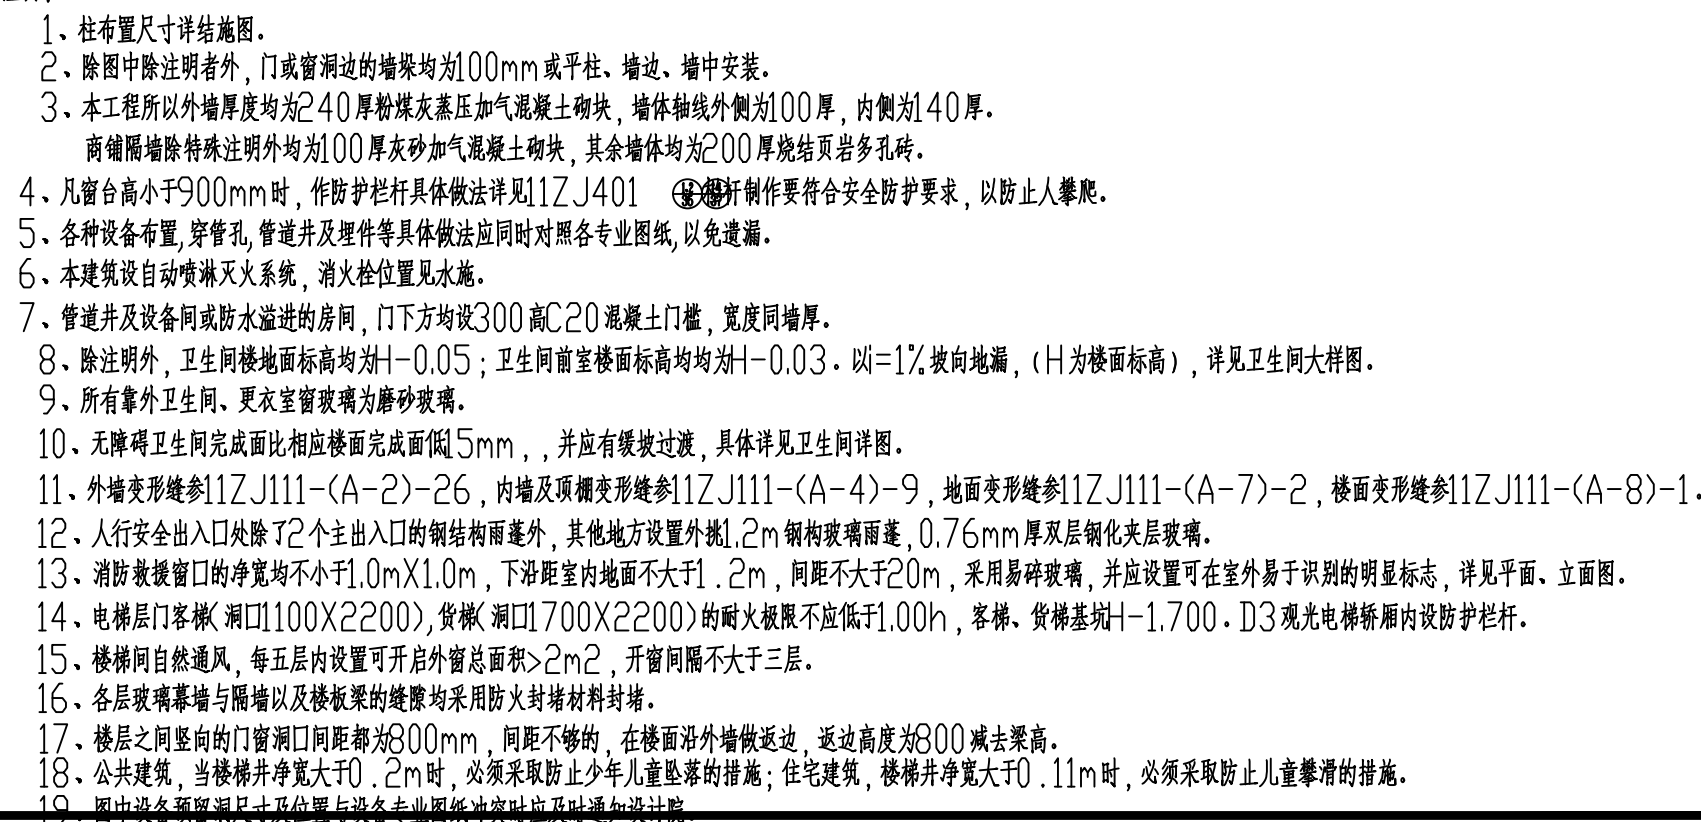
专业/DISCIPLINE: 建施

出图日期/DATE: 2021.06

版次	修改内容	日期
----	------	----

--	--	--

版权所有 不得复制 李田

[illegible]

S	合用前室及前室
T	疏散楼梯
ST	金属竖梯
D	客梯、货梯
FT	自动扶梯
XD	消防电梯
➡	安全出口

本层为一个防火分区，防火分区面积为3767.79m²，共有9个疏散楼梯，9个安全出口，其中LT1楼梯间为影院独有楼梯间。
 房区内最远点至最近安全出口的距离为21.8m(≤27.5m)，最远疏散点至最近安全出口的距离为30.8m(≤37.5m)，满足规范要求
 本层需要的疏散宽度为3739.78X0.43X1.1=1643.34m，计算疏散宽度的面积是减掉本层住宅楼梯间、消防电梯间面积的净面积
 本层设计的疏散宽度为2X1.475+2.325X2+2.34X2+2X2.075=16.43m，满足规范要求。