


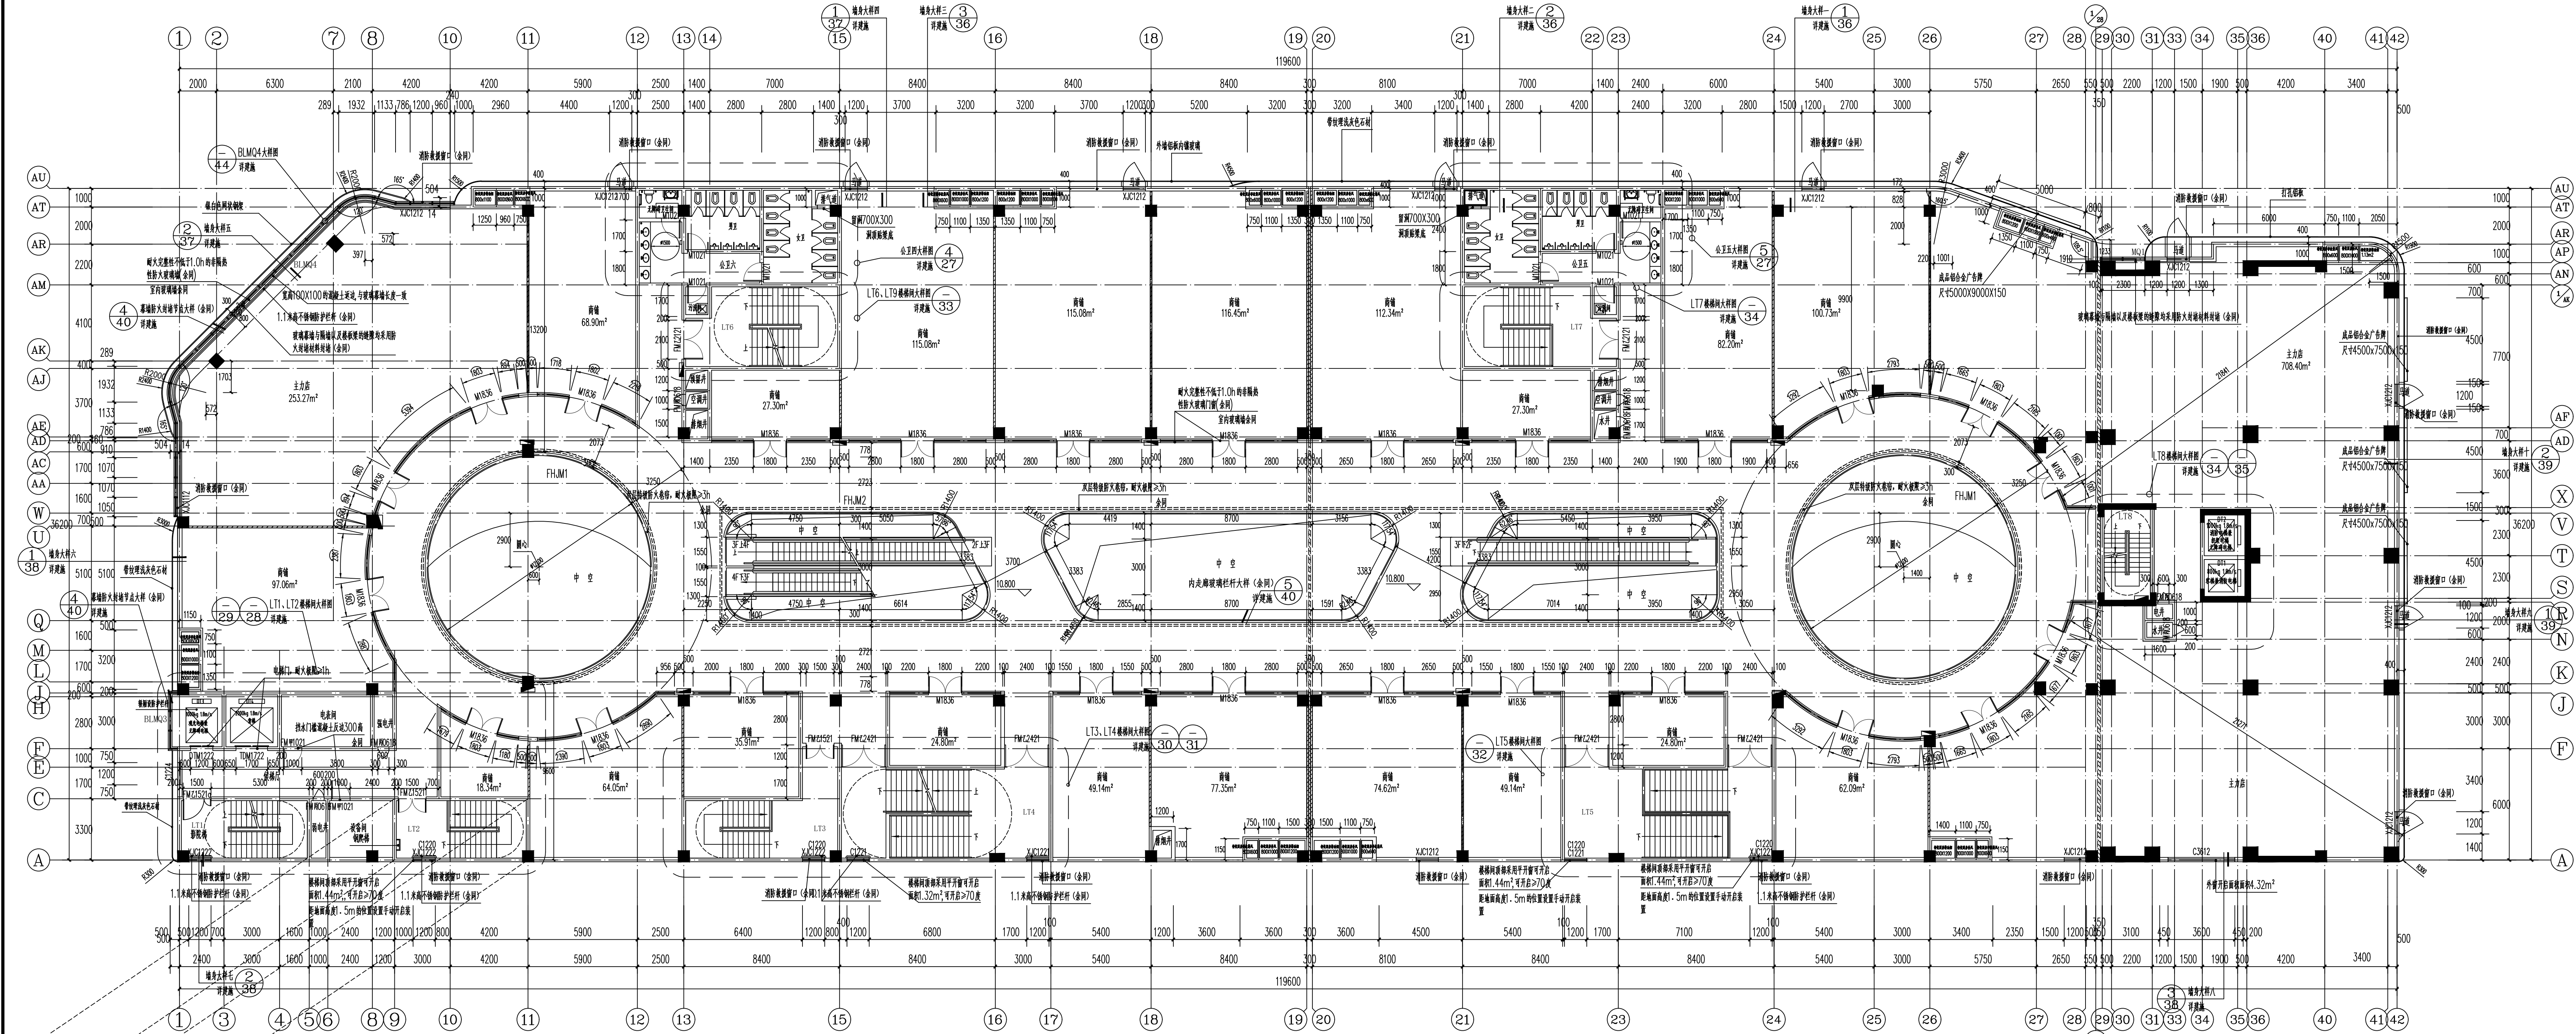

三层平面图 1:150

本层建筑面积: 3837.23m²

图例

灰砂加气混凝土砌块 (商铺隔墙)

消火栓

- 注:
- 柱布置尺寸详结构图。
 - 除图中除注明者外, 门窗洞口的墙体均为100mm厚平柱, 墙中安装。
 - 本工程所有外墙厚度均为240mm厚灰砂加气混凝土砌块, 墙体厚度为100mm, 内墙为40mm。
 - 商铺隔墙除特殊注明外均为100mm厚灰砂加气混凝土砌块, 其余墙体均为200mm厚灰砂加气混凝土砌块。
 - 凡窗台高小于900mm时, 作防护栏杆具体做法详见1Z J401。玻璃幕墙作符合安全防护要求, 以防止人攀爬。
 - 各种设备管道、穿墙孔、管井及附件等具体做法详同时对照各专业图纸, 以免遗漏。
 - 本建筑设自动喷淋灭火系统, 消防栓位置见水池。
 - 管进井及设备间防水溢进房间, 门下设300mm宽C20混凝土门槛, 高度同墙厚。
 - 除注明外, 卫生间楼面标高均为+0.05; 卫生间楼面标高均为+0.03, 以=1%坡度向地漏, (H为楼面标高), 详见卫生间大样图。
 - 所有意外卫生间, 更衣室玻璃门为磨砂玻璃。
 - 无隔间卫生间完成面比相应楼面完成面低5mm, 并应有坡度坡, 具体详见卫生间详图。
 - 外墙变形缝缝1Z J111-(A-2)-26, 内墙及顶棚变形缝缝1Z J111-(A-4)-9, 地面变形缝缝1Z J111-(A-7)-2, 楼面变形缝缝1Z J111-(A-8)-1。
 - 人行安全出入口除T2个出入口的钢化玻璃门外, 其他地方设置外挑2m钢化玻璃雨篷, 0.76mm厚夹层钢化夹层玻璃。
 - 消防疏散出口的净宽均不小于1.0mX1.0m, 下楼梯距地面不大于1.2m, 间距不大于2m, 采用钢化玻璃, 并应设置在室外易于识别的明显标志, 详见平面、立面图。
 - 电梯层门客梯(洞口100X2200), 货梯(洞口700X2200)的耐火极限不应低于1.0h, 客梯、货梯基台-1.700。D3观光电梯轿厢内应设防护栏。
 - 楼梯间自然通风, 每五层内设置可开启外窗总面积>2m², 开窗间隔不大于三层。
 - 各层玻璃幕墙与隔墙以及楼板的墙体均采用防火封堵材料封堵。
 - 楼层之间竖向的门窗洞口间距应≥300mm, 间距不够的, 在楼层外墙做进深, 进深高度为800mm高。
 - 公共建筑, 当楼梯净宽大于0.2m时, 必须采取防止少年儿童攀爬的措施; 住宅建筑, 楼梯净宽大于0.11m时, 必须采取防止少年儿童攀爬的措施。
 - 图中设备预留尺寸及位置与设备专业图纸冲突时及时通知设计院。

消防示意图例

S	合用前室及前室
T	疏散楼梯
ST	金属楼梯
D	客梯、货梯
FT	自动扶梯
XD	消防电梯
➔	安全出口

注: 三层商场设置自动喷淋灭火系统

本层为一个防火分区, 防火分区面积为3837.23m², 共有9个疏散楼梯, 9个安全出口, 其中L11楼梯间为影院独有楼梯间。
房间内最远点至最近安全出口的距离为21.8m(≤27.5m), 最近疏散门至最近安全出口的距离为30.8m(≤37.5m), 满足规范要求。
本层需要的疏散宽度为3809.22X0.39X1/100=14.86m(计算疏散宽度的面积是减掉本层住宅楼梯间、消防电梯间面积的净面积)
本层设计的疏散宽度为2X1.475+2.325X2+2.34X2+2X2.075=16.43m, 满足规范要求。

建设单位/CLIENT:

麻阳苗族自治县远桥房地产开发有限公司


项目名称/PROJECT:

远程国际

子项目名称/SUB-PROJECT:

远程国际

区位图/REGIONAL LOCATION MAP:

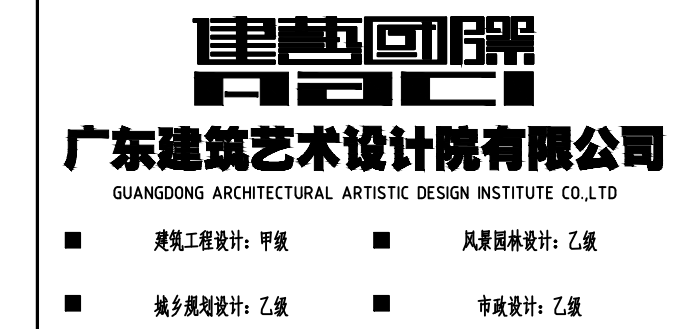

图纸名称/TITLE:

三层平面图

项目名称/PROJECT:

远程国际

设计 DESIGNED	古新辉	设计人
校对 CHECKED	吴新红	校对
专业负责人 CHIEF	吴志刚	专业负责人
项目负责人 PROJECT CHIEF	吴志刚	项目负责人
审核 IDENTIFIED	黄履优	审核
审定 APPROVED	李 坚	审定

业务号/JOB NO.

设计阶段/STATUS: 施工图

专业/DISCIPLINE: 建筑

比例/SCALE: 1: 100 规格/SIZE: A1

出图日期/DATE: 2021. 06

图号/DRAWING NO. JS-16

版次 NO.	修改内容 DESCRIPTION	日期 DATE

条形码/BARCODE:

版权所有, 不得复制或套用。
ALL RIGHTS RESERVED, DON'T COPIED, REPRODUCED.