


建设单位/CLIENT:
麻阳苗族自治县远桥房地产开发有限公司

项目名称/PROJECT:
远程国际

子项目名称/SUB-PROJECT:
远程国际

区位图/REGIONAL LOCATION MAP :

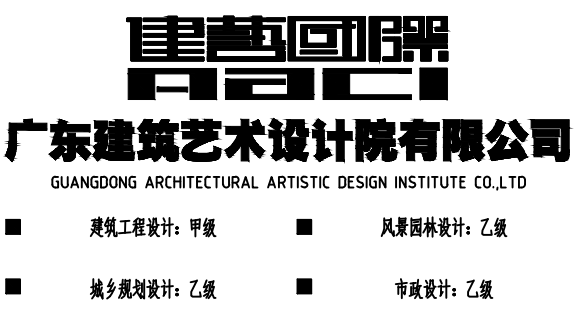

图纸名称/TITLE:
五~十三层平面图
十四层平面图

项目名称/PROJECT:
远程国际

设计 DESIGNED	古新辉	
校对 CHECKED	吴新红	
专业负责人 CHIEF	吴志刚	
项目负责人 PROJECT CHIEF	吴志刚	
审核 IDENTIFIED	黄履优	
审定 APPROVED	李 坚	

业务号/JOB NO.

设计阶段/STATUS: 施工图

专业/DISCIPLINE: 建筑

比例/
SCALE: 1: 100 规格/
SIZE: A1


出图日期/DATE: 2021. 06

图号/DRAWING NO. JS-19

版次 NO.	修改内容 DESCRIPTION	日期 DATE


条形码/BARCODE:

版权所有，不得复制、套用。
ALL RIGHTS RESERVED, DON'T COPIED, REPRODUCED.

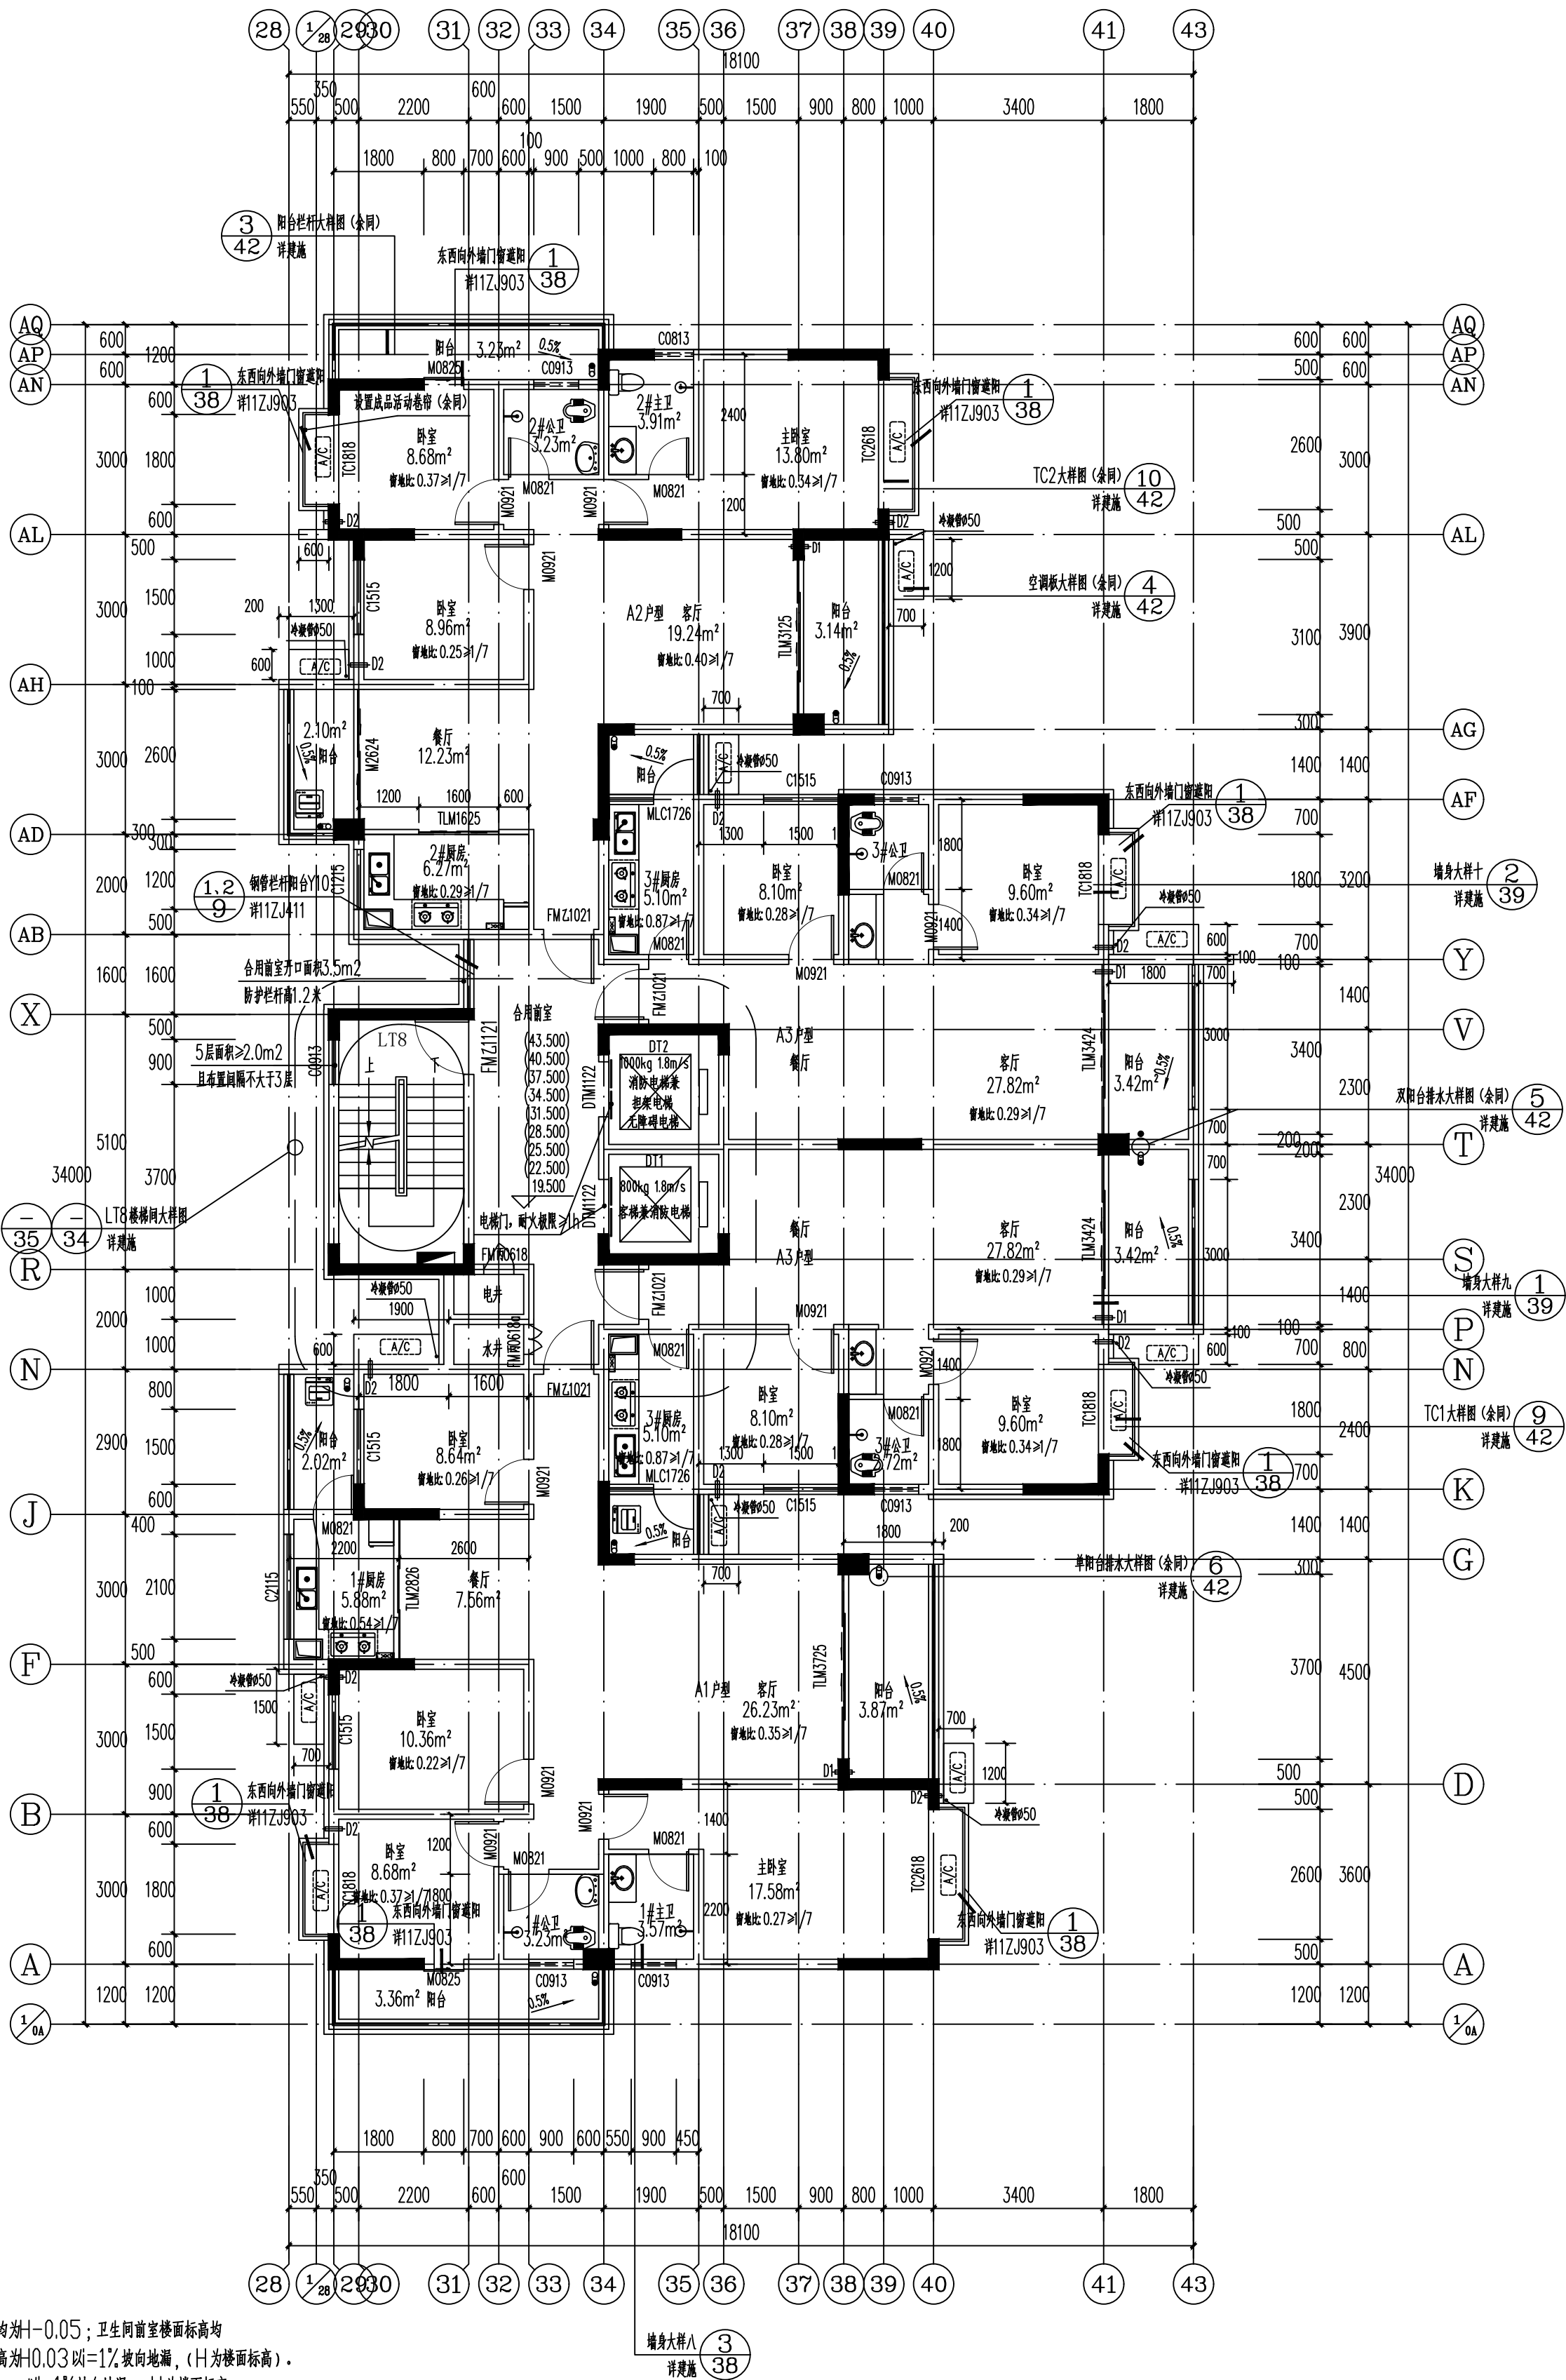

- 说明:
- 除注明者外，卫生间楼面标高均 ± 0.05 ；卫生间首层楼面标高均 ± 0.03 。厨房楼面标高为 ± 0.03 或 $\pm 1\%$ 坡向地漏，(H为楼面标高)。
 - 阳台楼面标高均 ± 0.05 ， $\text{H}=\pm 1\%$ 坡向地漏，(H为楼面标高)。
 - ②为80空调穿线管预留洞，管向室外倾斜 10% ，距中心距地漏 2200 高，中心距地漏 150 或平挂。
 - ③为80空调穿线管预留洞，管向室外倾斜 10% ，距中心距地漏 300 高，中心距地漏 150 或平挂。
 - 凡露台高小 $\geq 900\text{mm}$ 时，作防护栏杆具体做法详见11ZJ401 ③防护栏杆要符合安全设计要求，以防止人坠落。
 - 所有凸窗均设 900mm 高防护栏杆。
 - 通风处预留洞(位置见上图) 700×800 (H)，距底距顶层面 950 (H)。
 - 图中未注尺寸位置已在同一户型相应位置标注。
 - 图中设备预留洞尺寸及位置与设备专业图纸冲突时及时通知设计院。

五~十三层平面图 1:100
本层建筑面积: 420.60m²

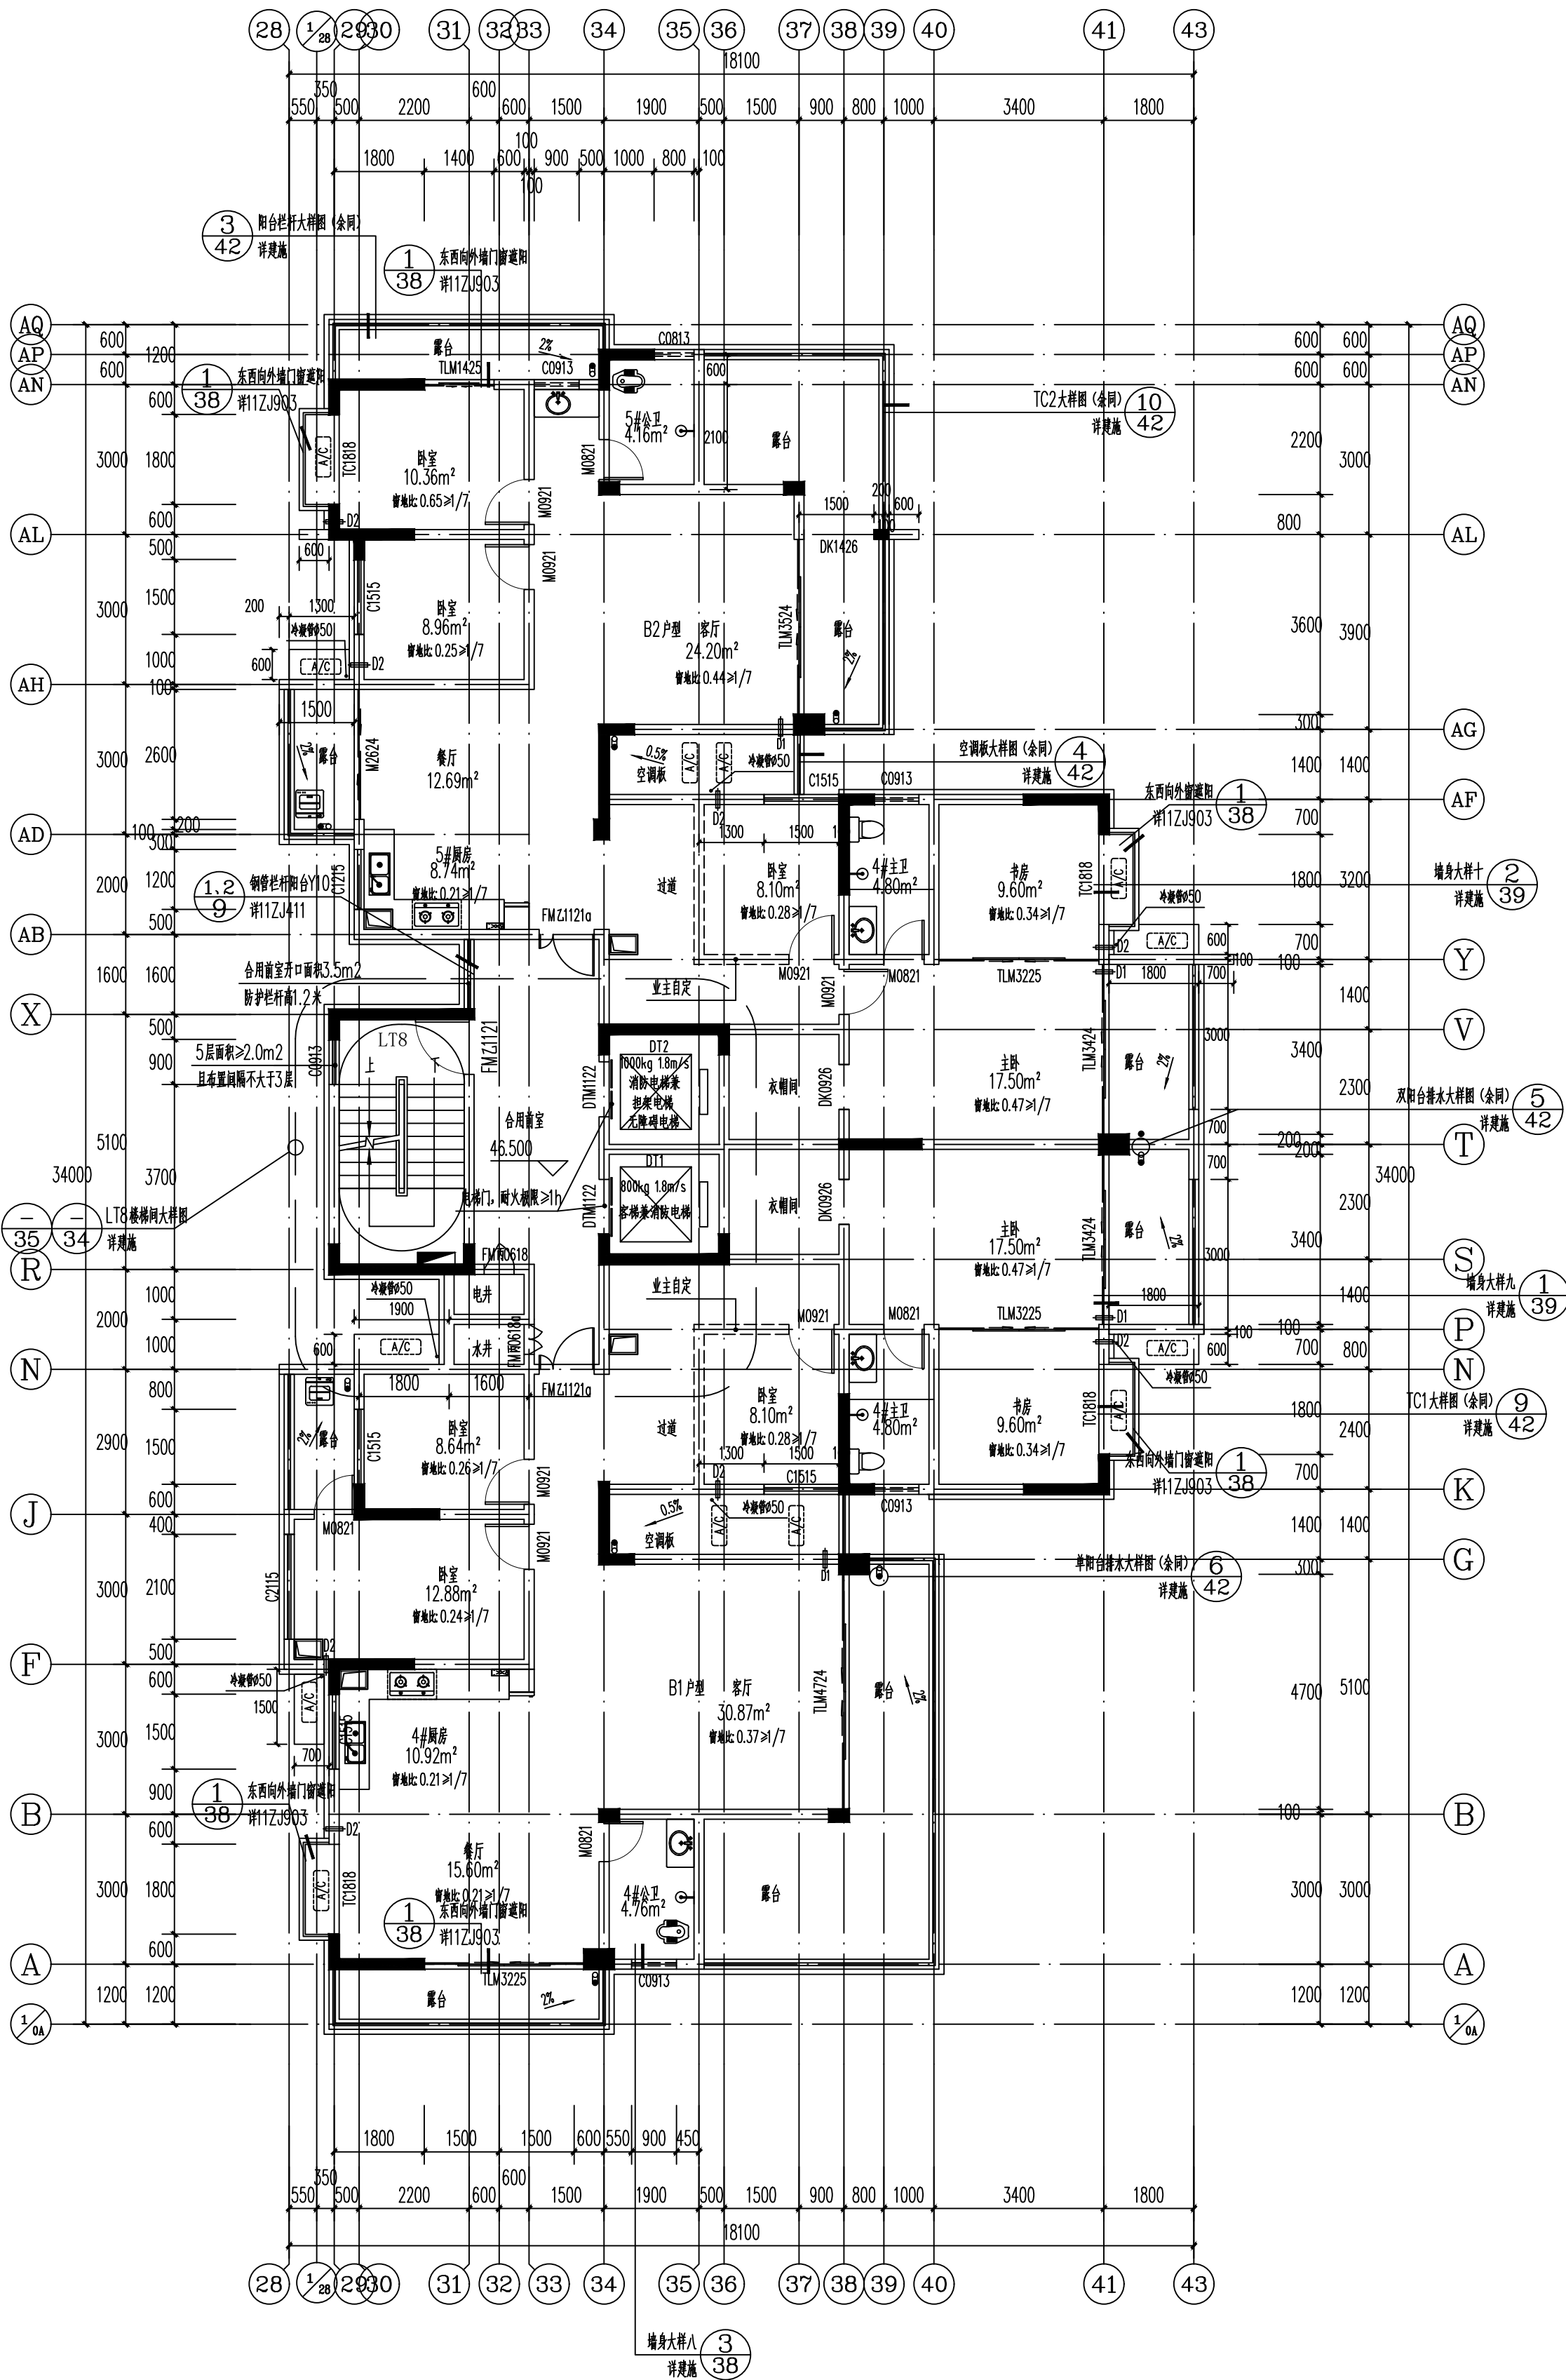

十四层平面图 1:100
本层建筑面积: 363.48m²