





建设单位/CLIENT:
麻阳苗族自治县远桥房地产开发有限公司

项目名称/PROJECT:
远程国际

子项目名称/SUB-PROJECT:
远程国际

区位图/REGIONAL LOCATION MAP:

广东建筑艺术设计院有限公司
GUANGDONG ARCHITECTURAL DESIGN INSTITUTE CO., LTD.
■ 建筑方案设计: 甲级 ■ 风景园林设计: 乙级
■ 城乡规划编制: 乙级 ■ 专业设计: 乙级

图纸名称/TITLE:
LT1、LT2楼梯间大样图一

项目名称/PROJECT:
远程国际

设计
DESIGNED
校对
CHECKED
专业负责人
CHIEF
项目负责人
PROJECT CHIEF
审核
IDENTIFIED
审定
APPROVED
业务号/JOB NO.
设计阶段/STATUS: 施工图
专业/DISCIPLINE: 建筑
比例/
SCALE: 1: 100 规格/
SIZE: A1
出图日期/DATE: 2021.06
图号/DRAWING NO. JS- 28
版次
NO. 修改内容
DESCRIPTION 日期
DATE
条形码/BARCODE:

版权所有，不得复制、套用。
ALL RIGHTS RESERVED, DON'T COPIED, REPRODUCED.