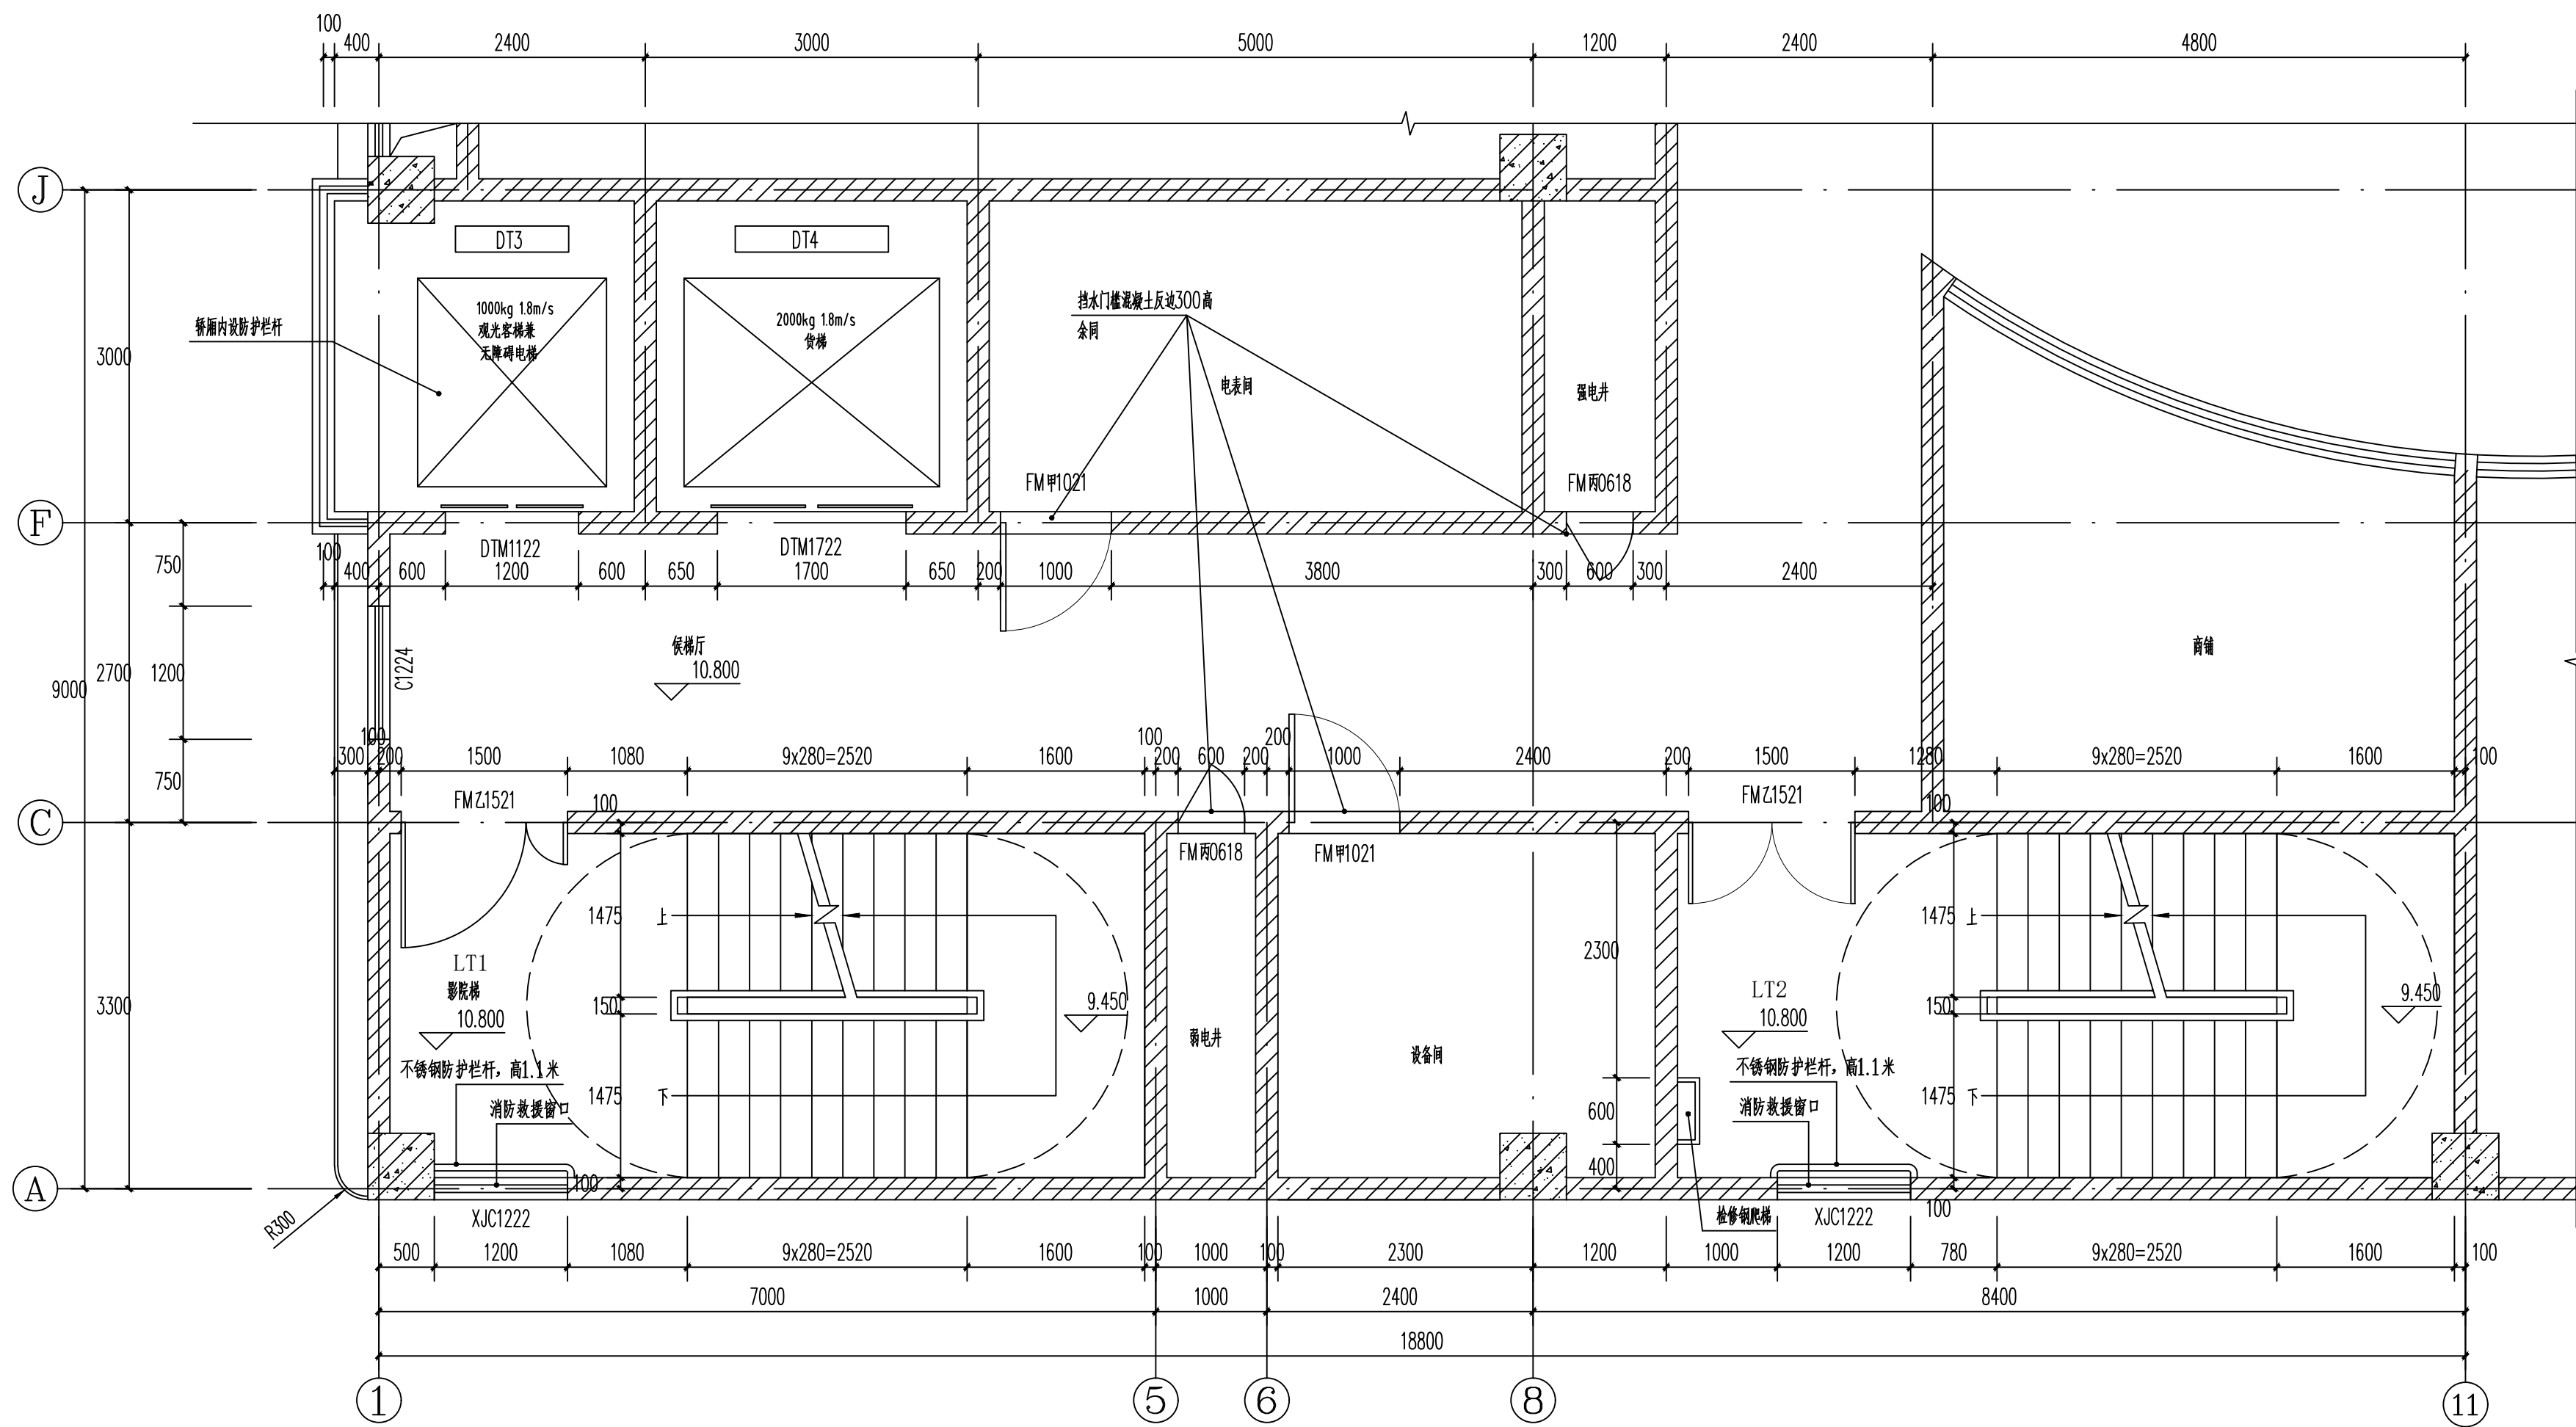
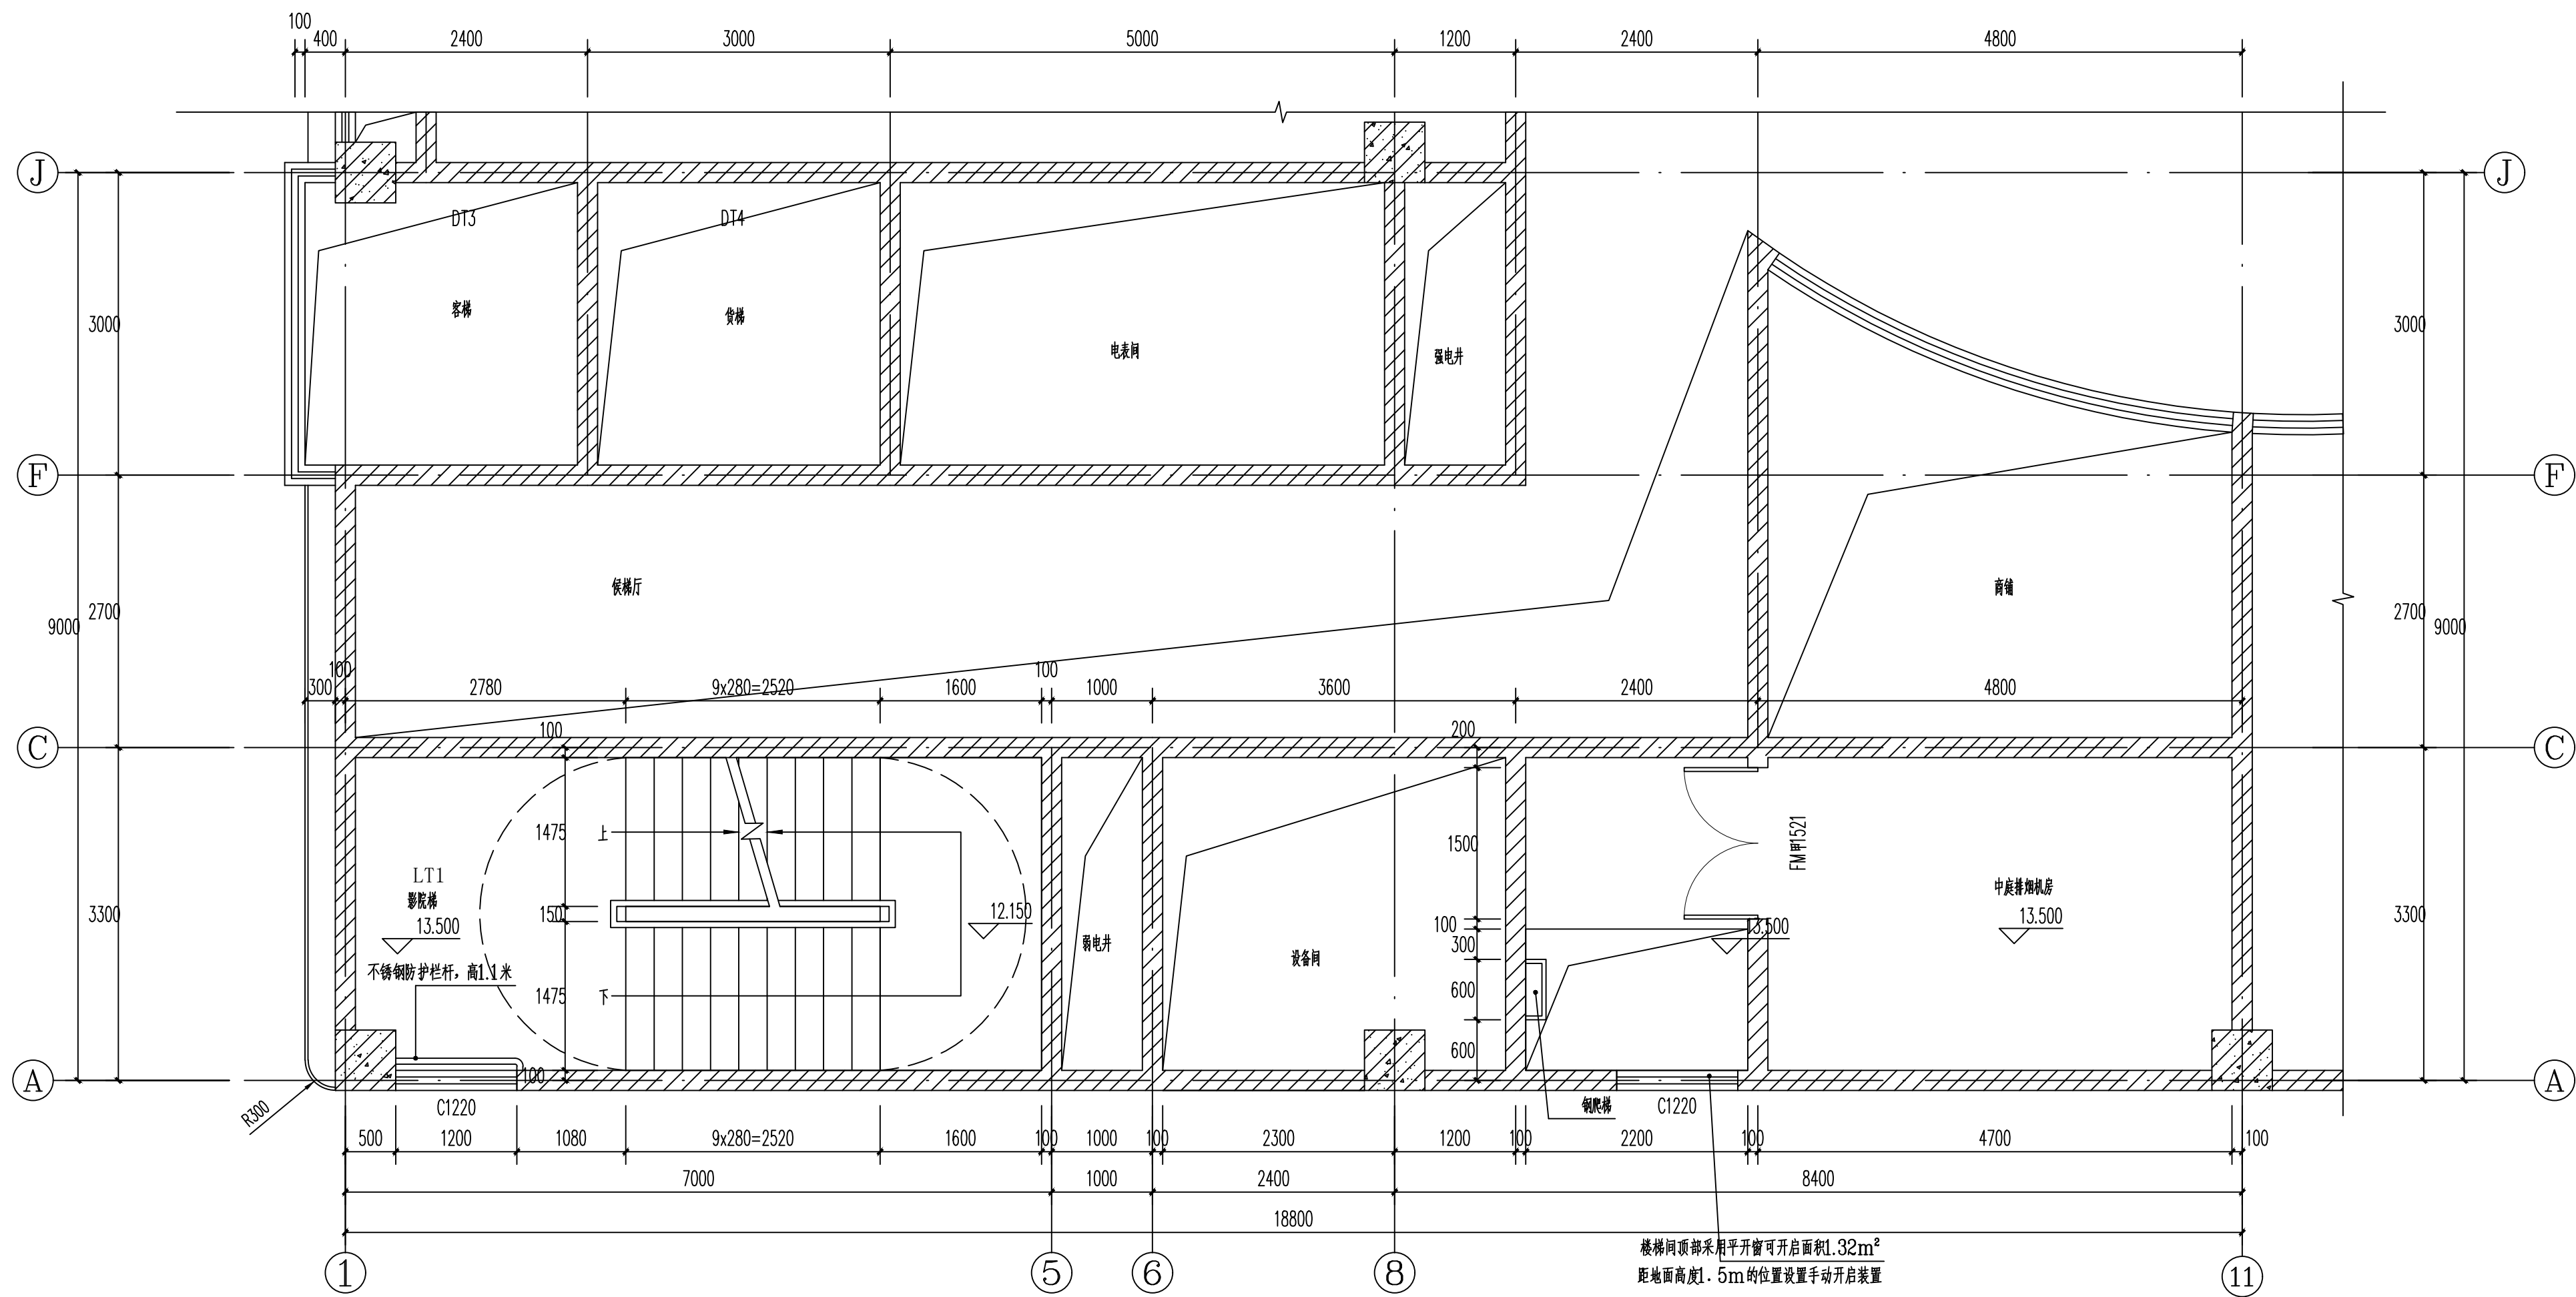
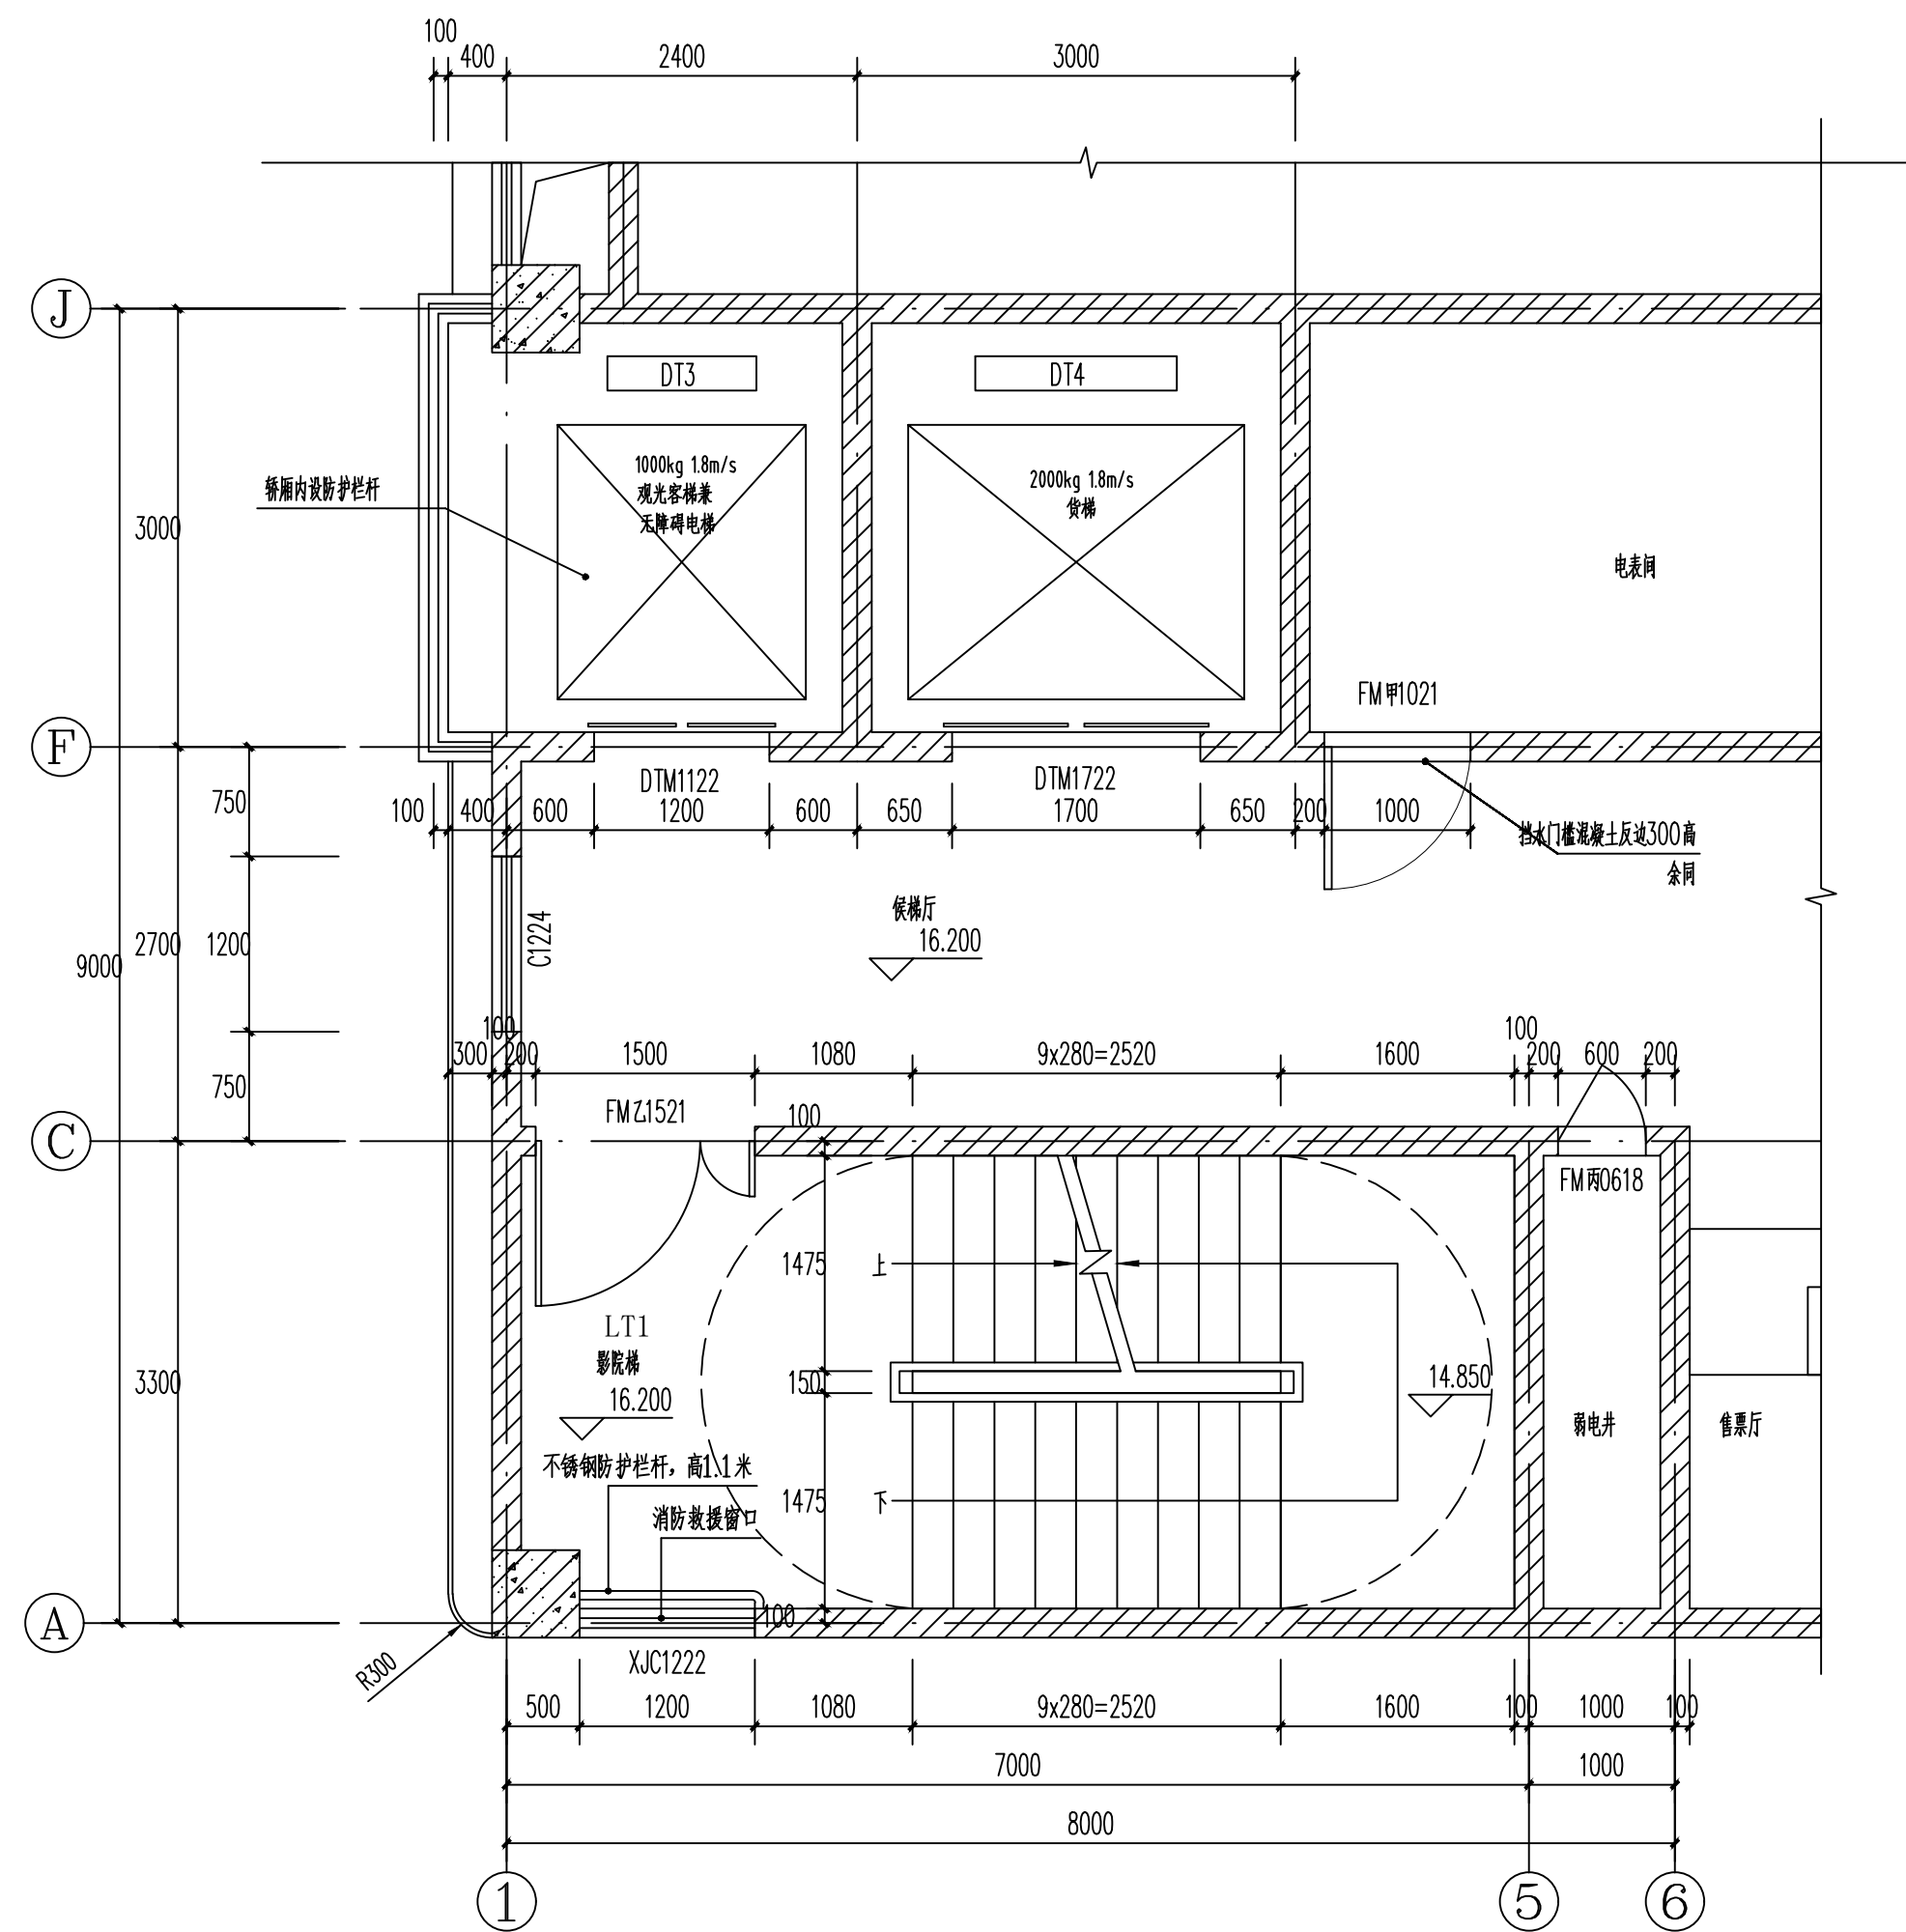





LT1、LT2楼梯间三层平面图 1:50




LT1、LT2楼梯间H=13.500处平面图 1:50



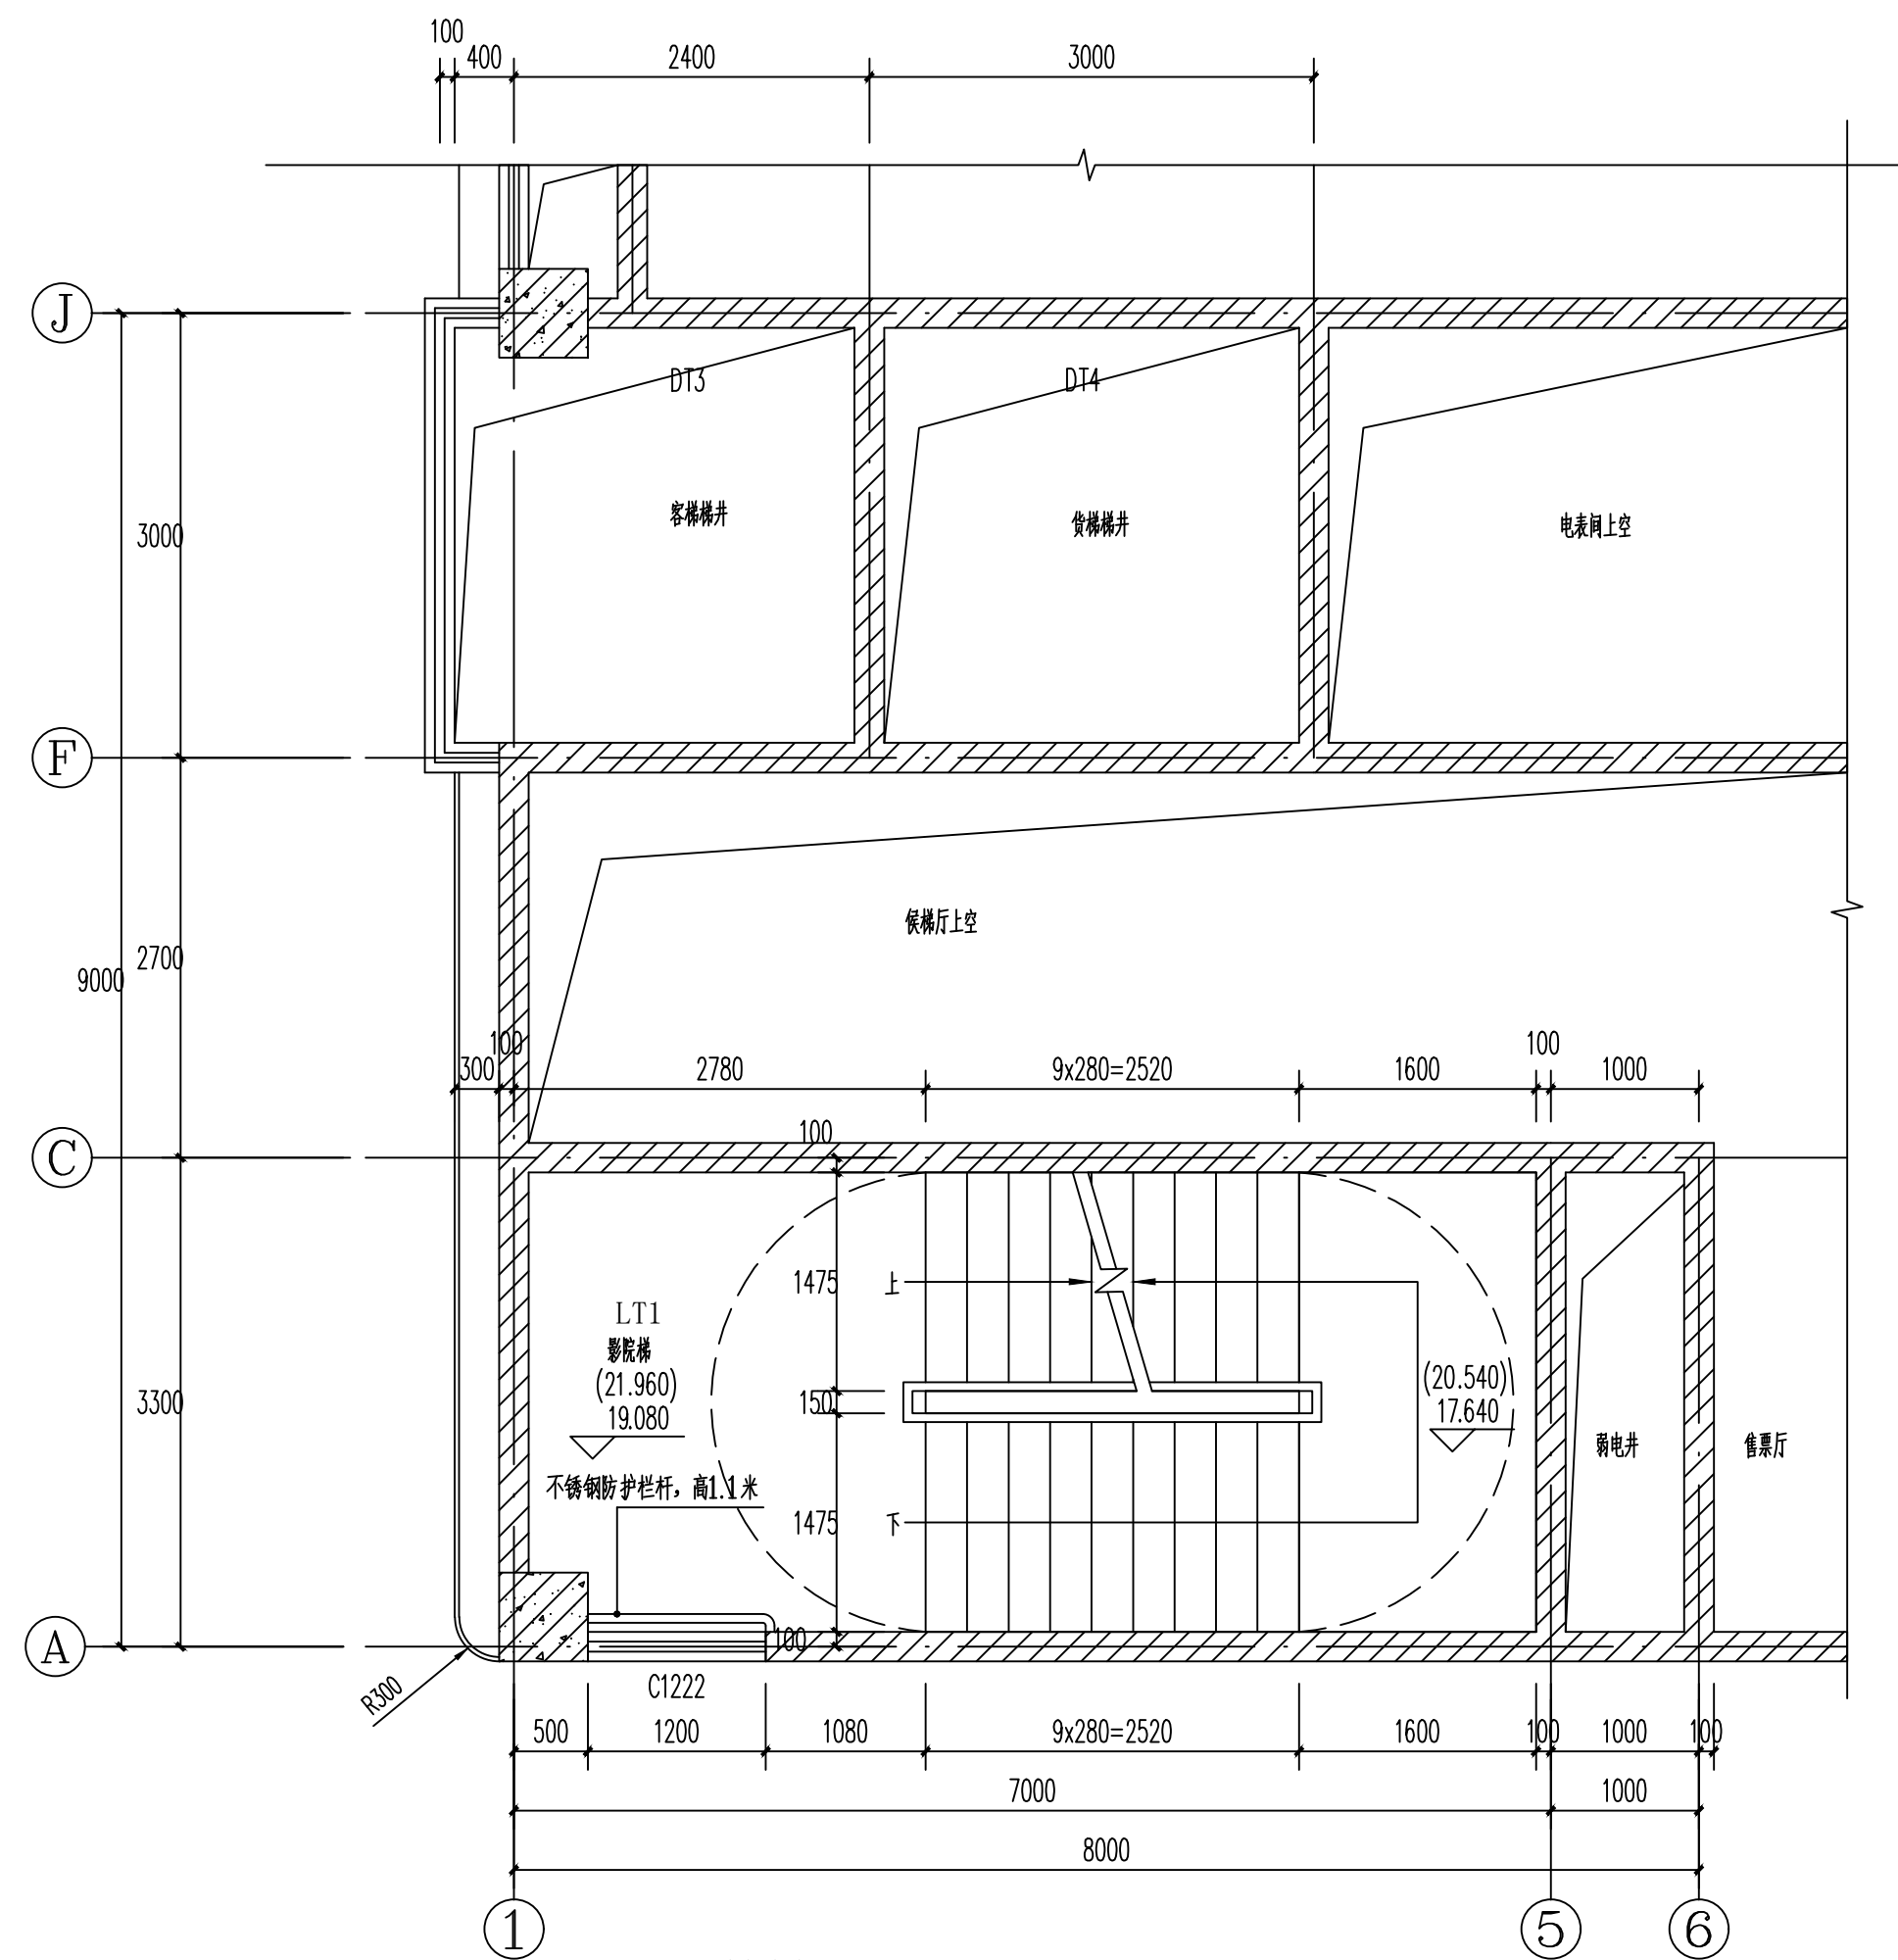LT1、LT2楼梯间三层平面图 1:50









LT1楼梯间H=19.08 (21.96)处平面图 1:50

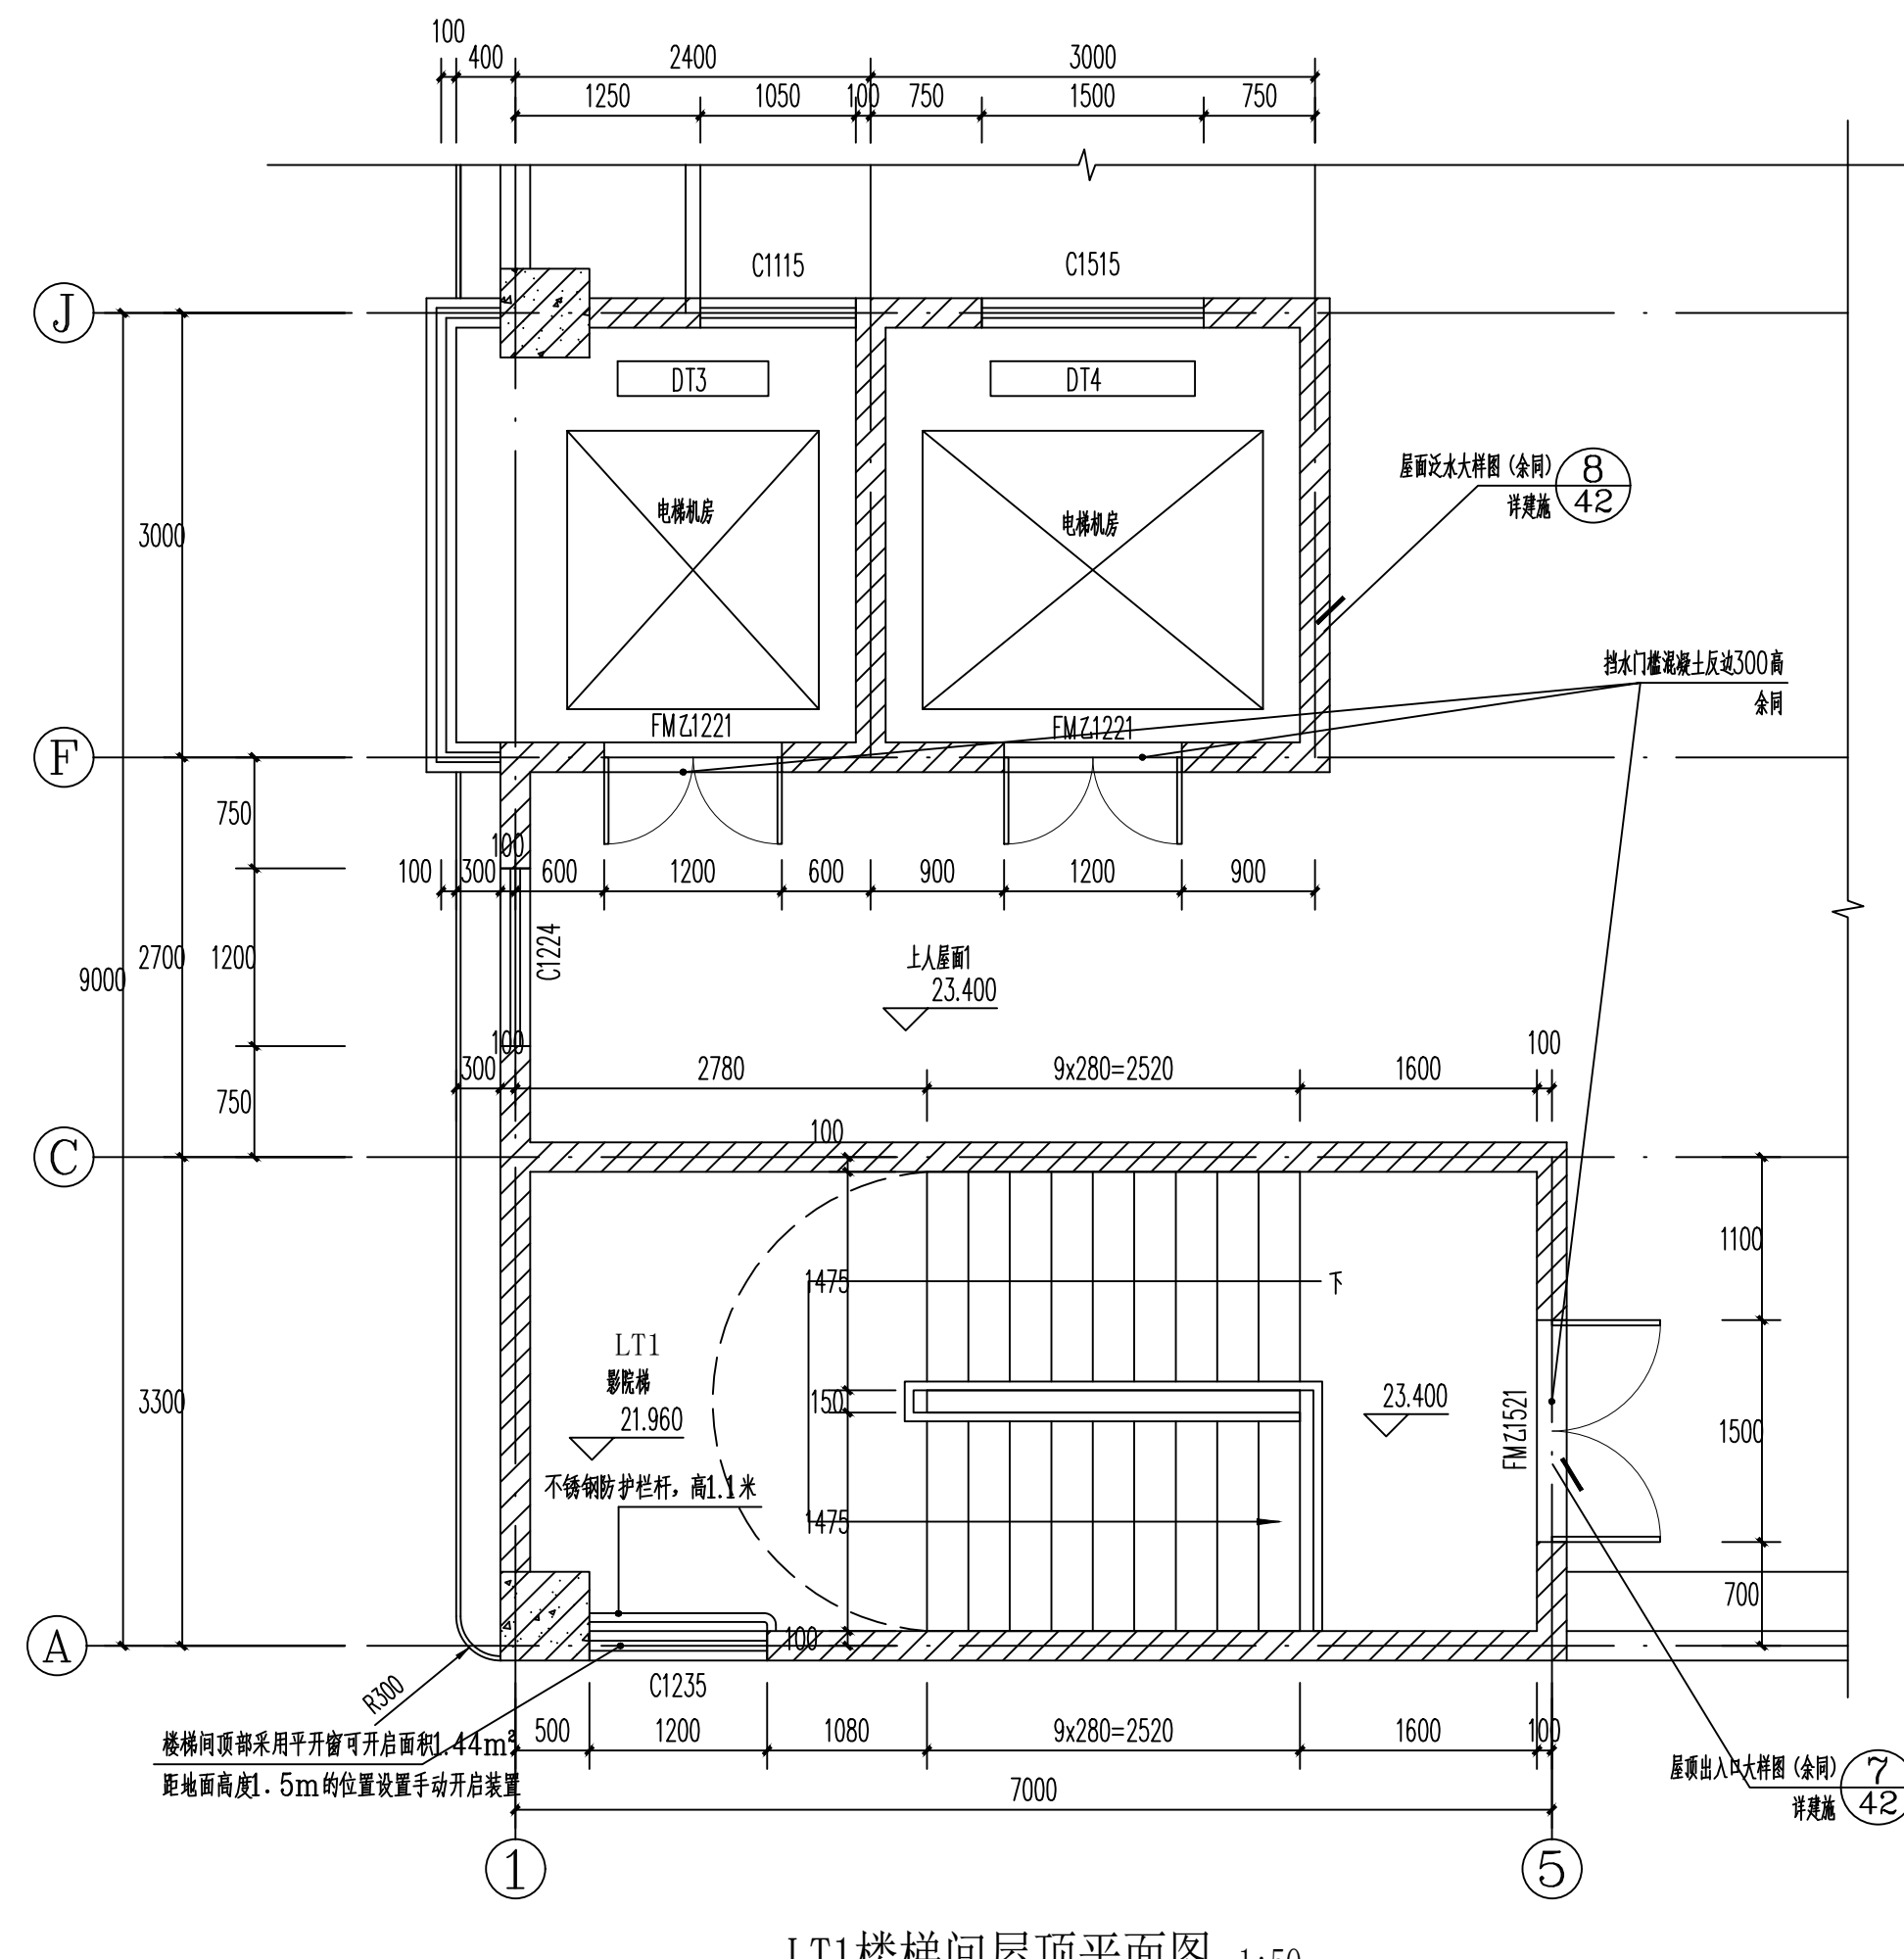

LT1楼梯间屋顶平面图 1:50

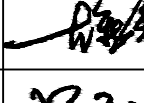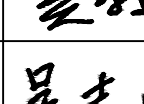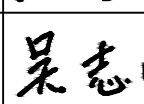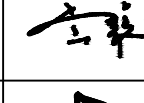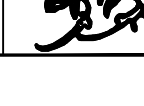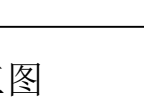建设单位/CLIENT:
麻阳苗族自治县远桥房地产开发有限公司
项目名称/PROJECT:
远程国际
子项目名称/SUB-PROJECT:
远程国际
区位图/REGIONAL LOCATION MAP :
售售 广东建筑艺术设计院有限公司 GUANGDONG ARCHITECTURAL ARTISTIC DESIGN INSTITUTE CO.,LTD ■ 建筑方案设计: 甲级 ■ 风景园林设计: 乙级 ■ 城乡规划设计: 乙级 ■ 市政工程设计: 乙级
图纸名称/TITLE:
LT1、LT2楼梯间大样图二

项目名称/PROJECT:			
远程国际			
设计 DESIGNED	古新辉		
校对 CHECKED	吴新红		
专业负责人 CHIEF	吴志刚		
项目负责人 PROJECT CHIEF	吴志刚		
审核 IDENTIFIED	黄履优		
审定 APPROVED	李 坚		
业务号/JOB NO.			
设计阶段/STATUS: 施工图			
专业/DISCIPLINE: 建筑			
比例/ SCALE:	1: 100	规格/ SIZE:	A1
出图日期/DATE:		2021.06	
图号/DRAWING NO. JS-29			
版次 NO.	修改内容 DESCRIPTION	日期 DATE	
条形码/BARCODE:			
版权所有，不得复制、套用。 ALL RIGHTS RESERVED, DON'T COPIED, REPRODUCED.			