




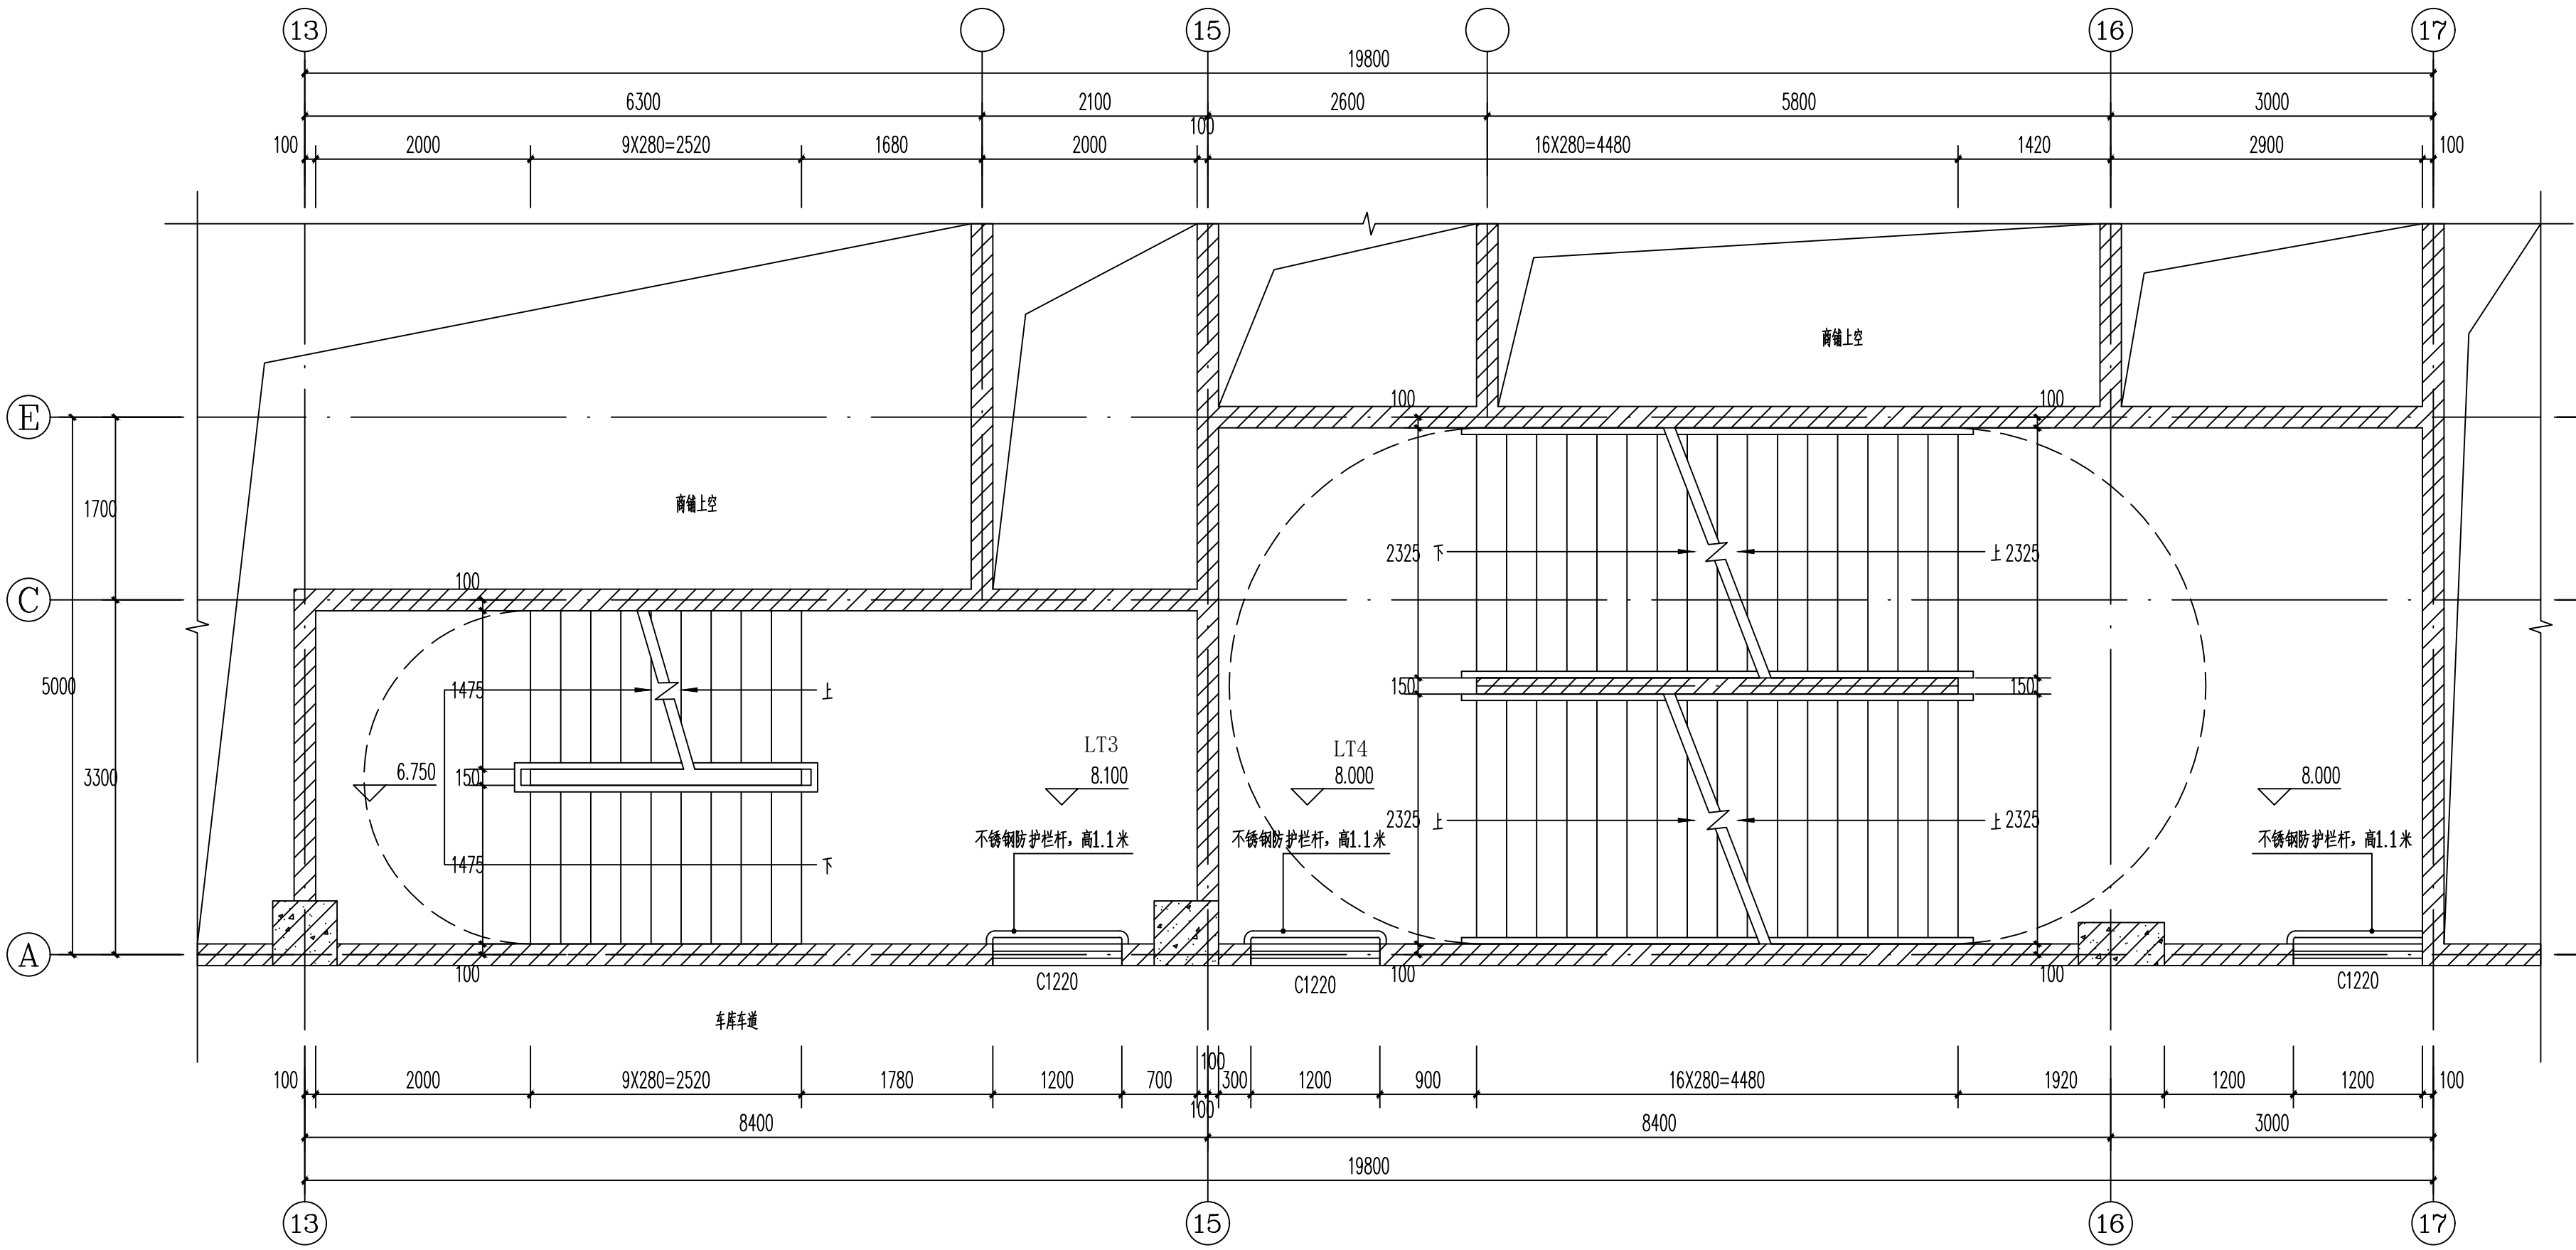


LT3、LT4楼梯间H=8.100处平面图 1:50

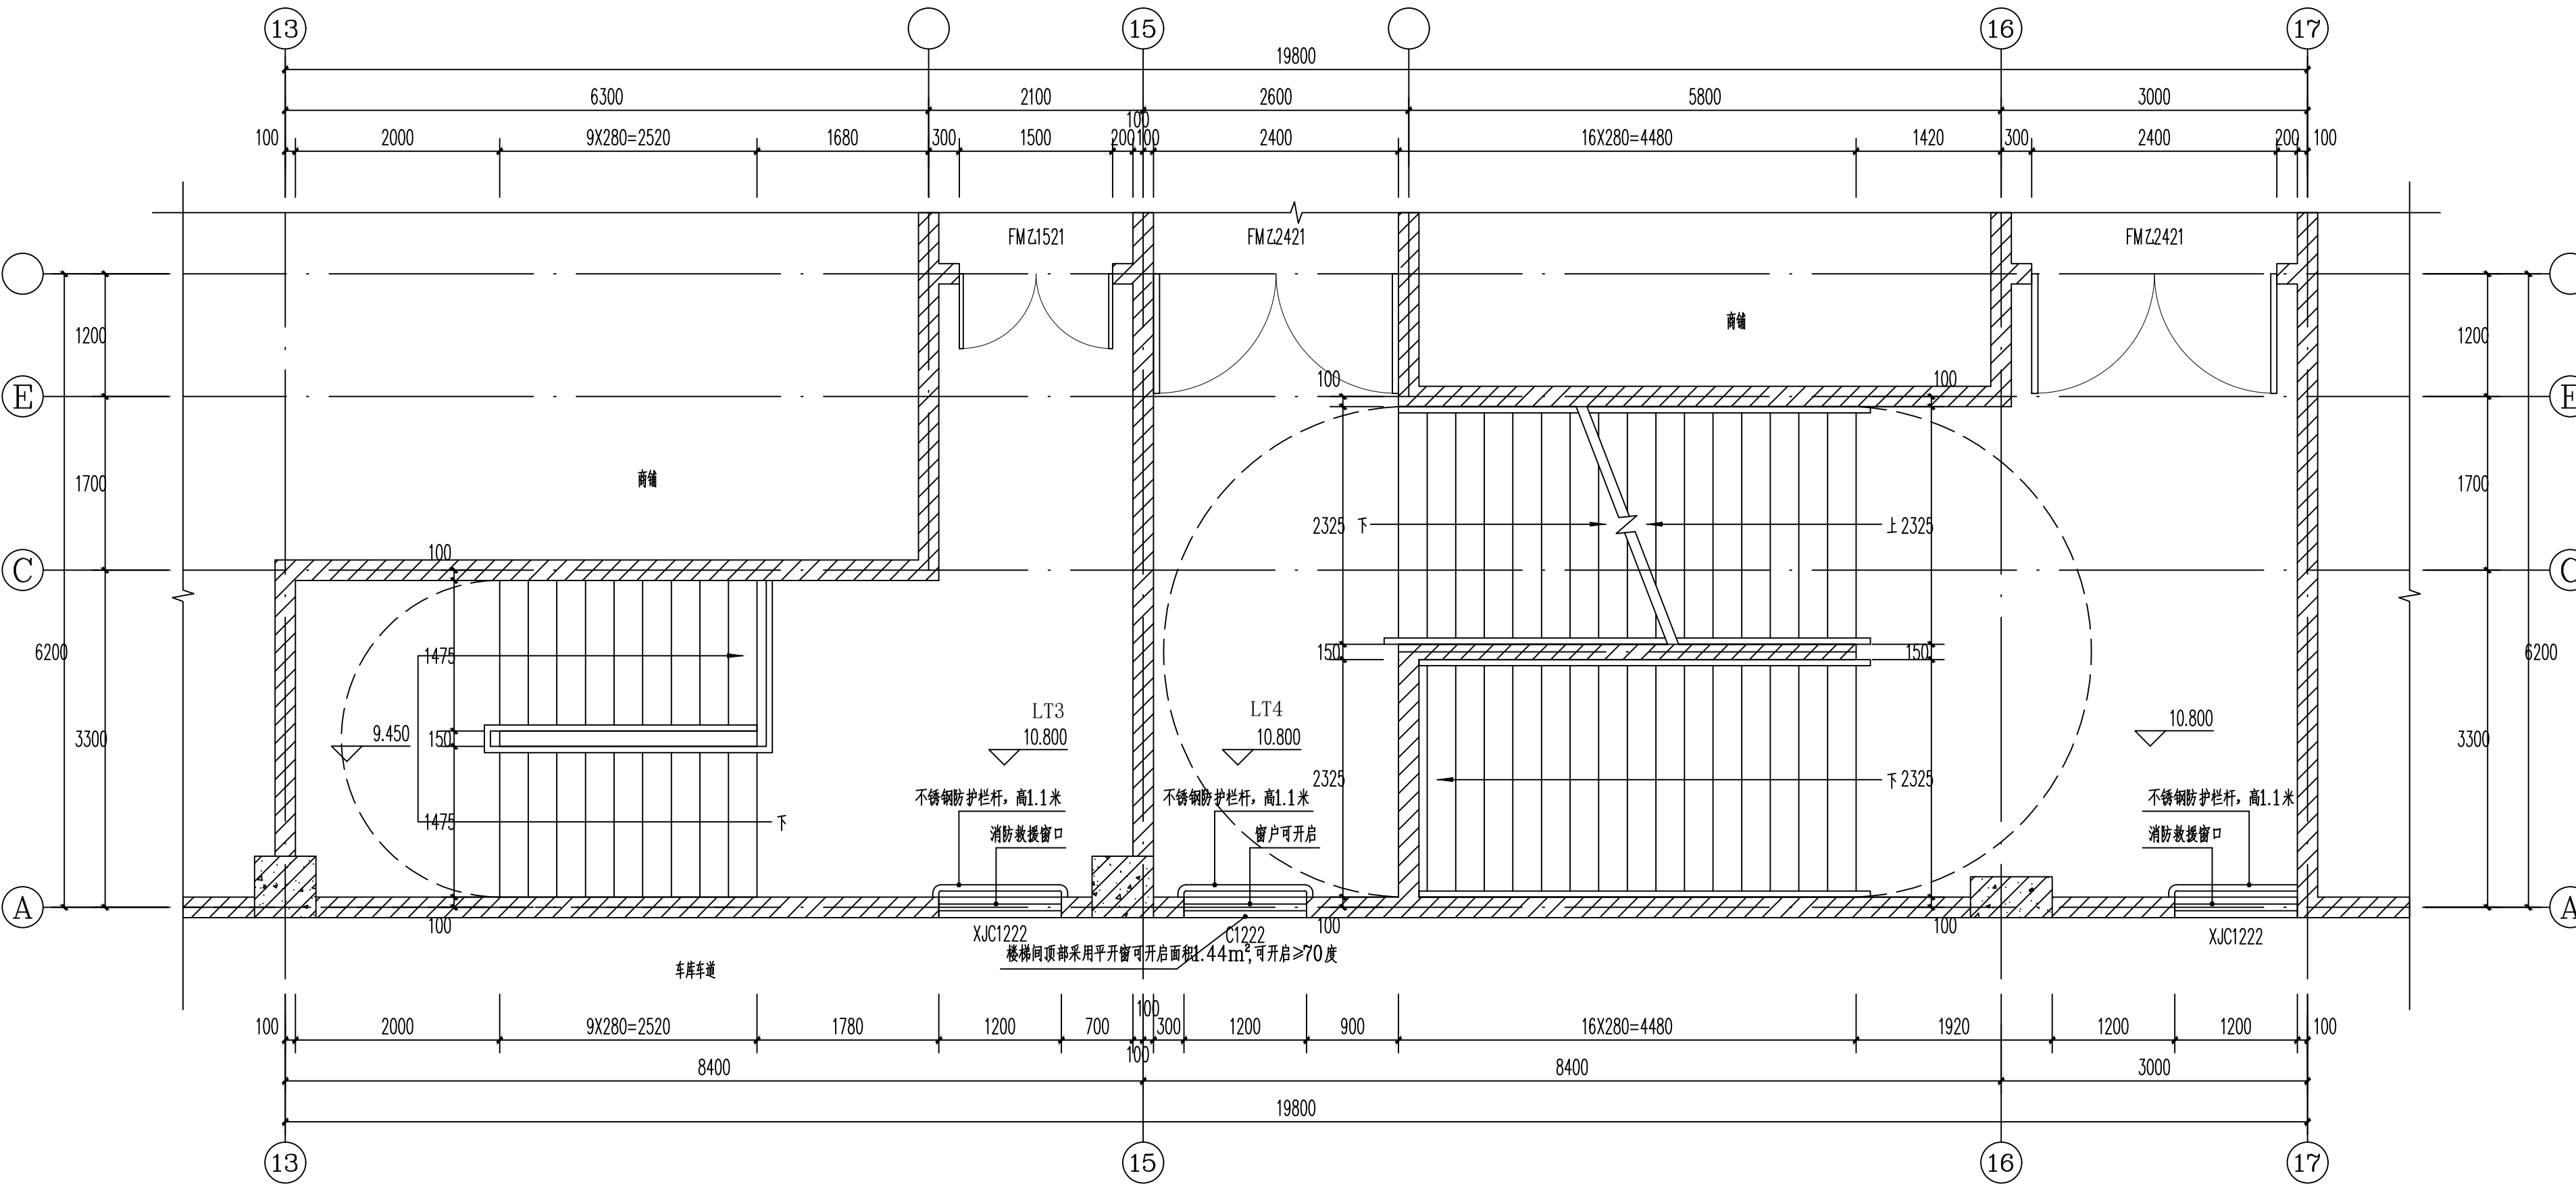


LT3、LT4楼梯间三层平面图 1:50

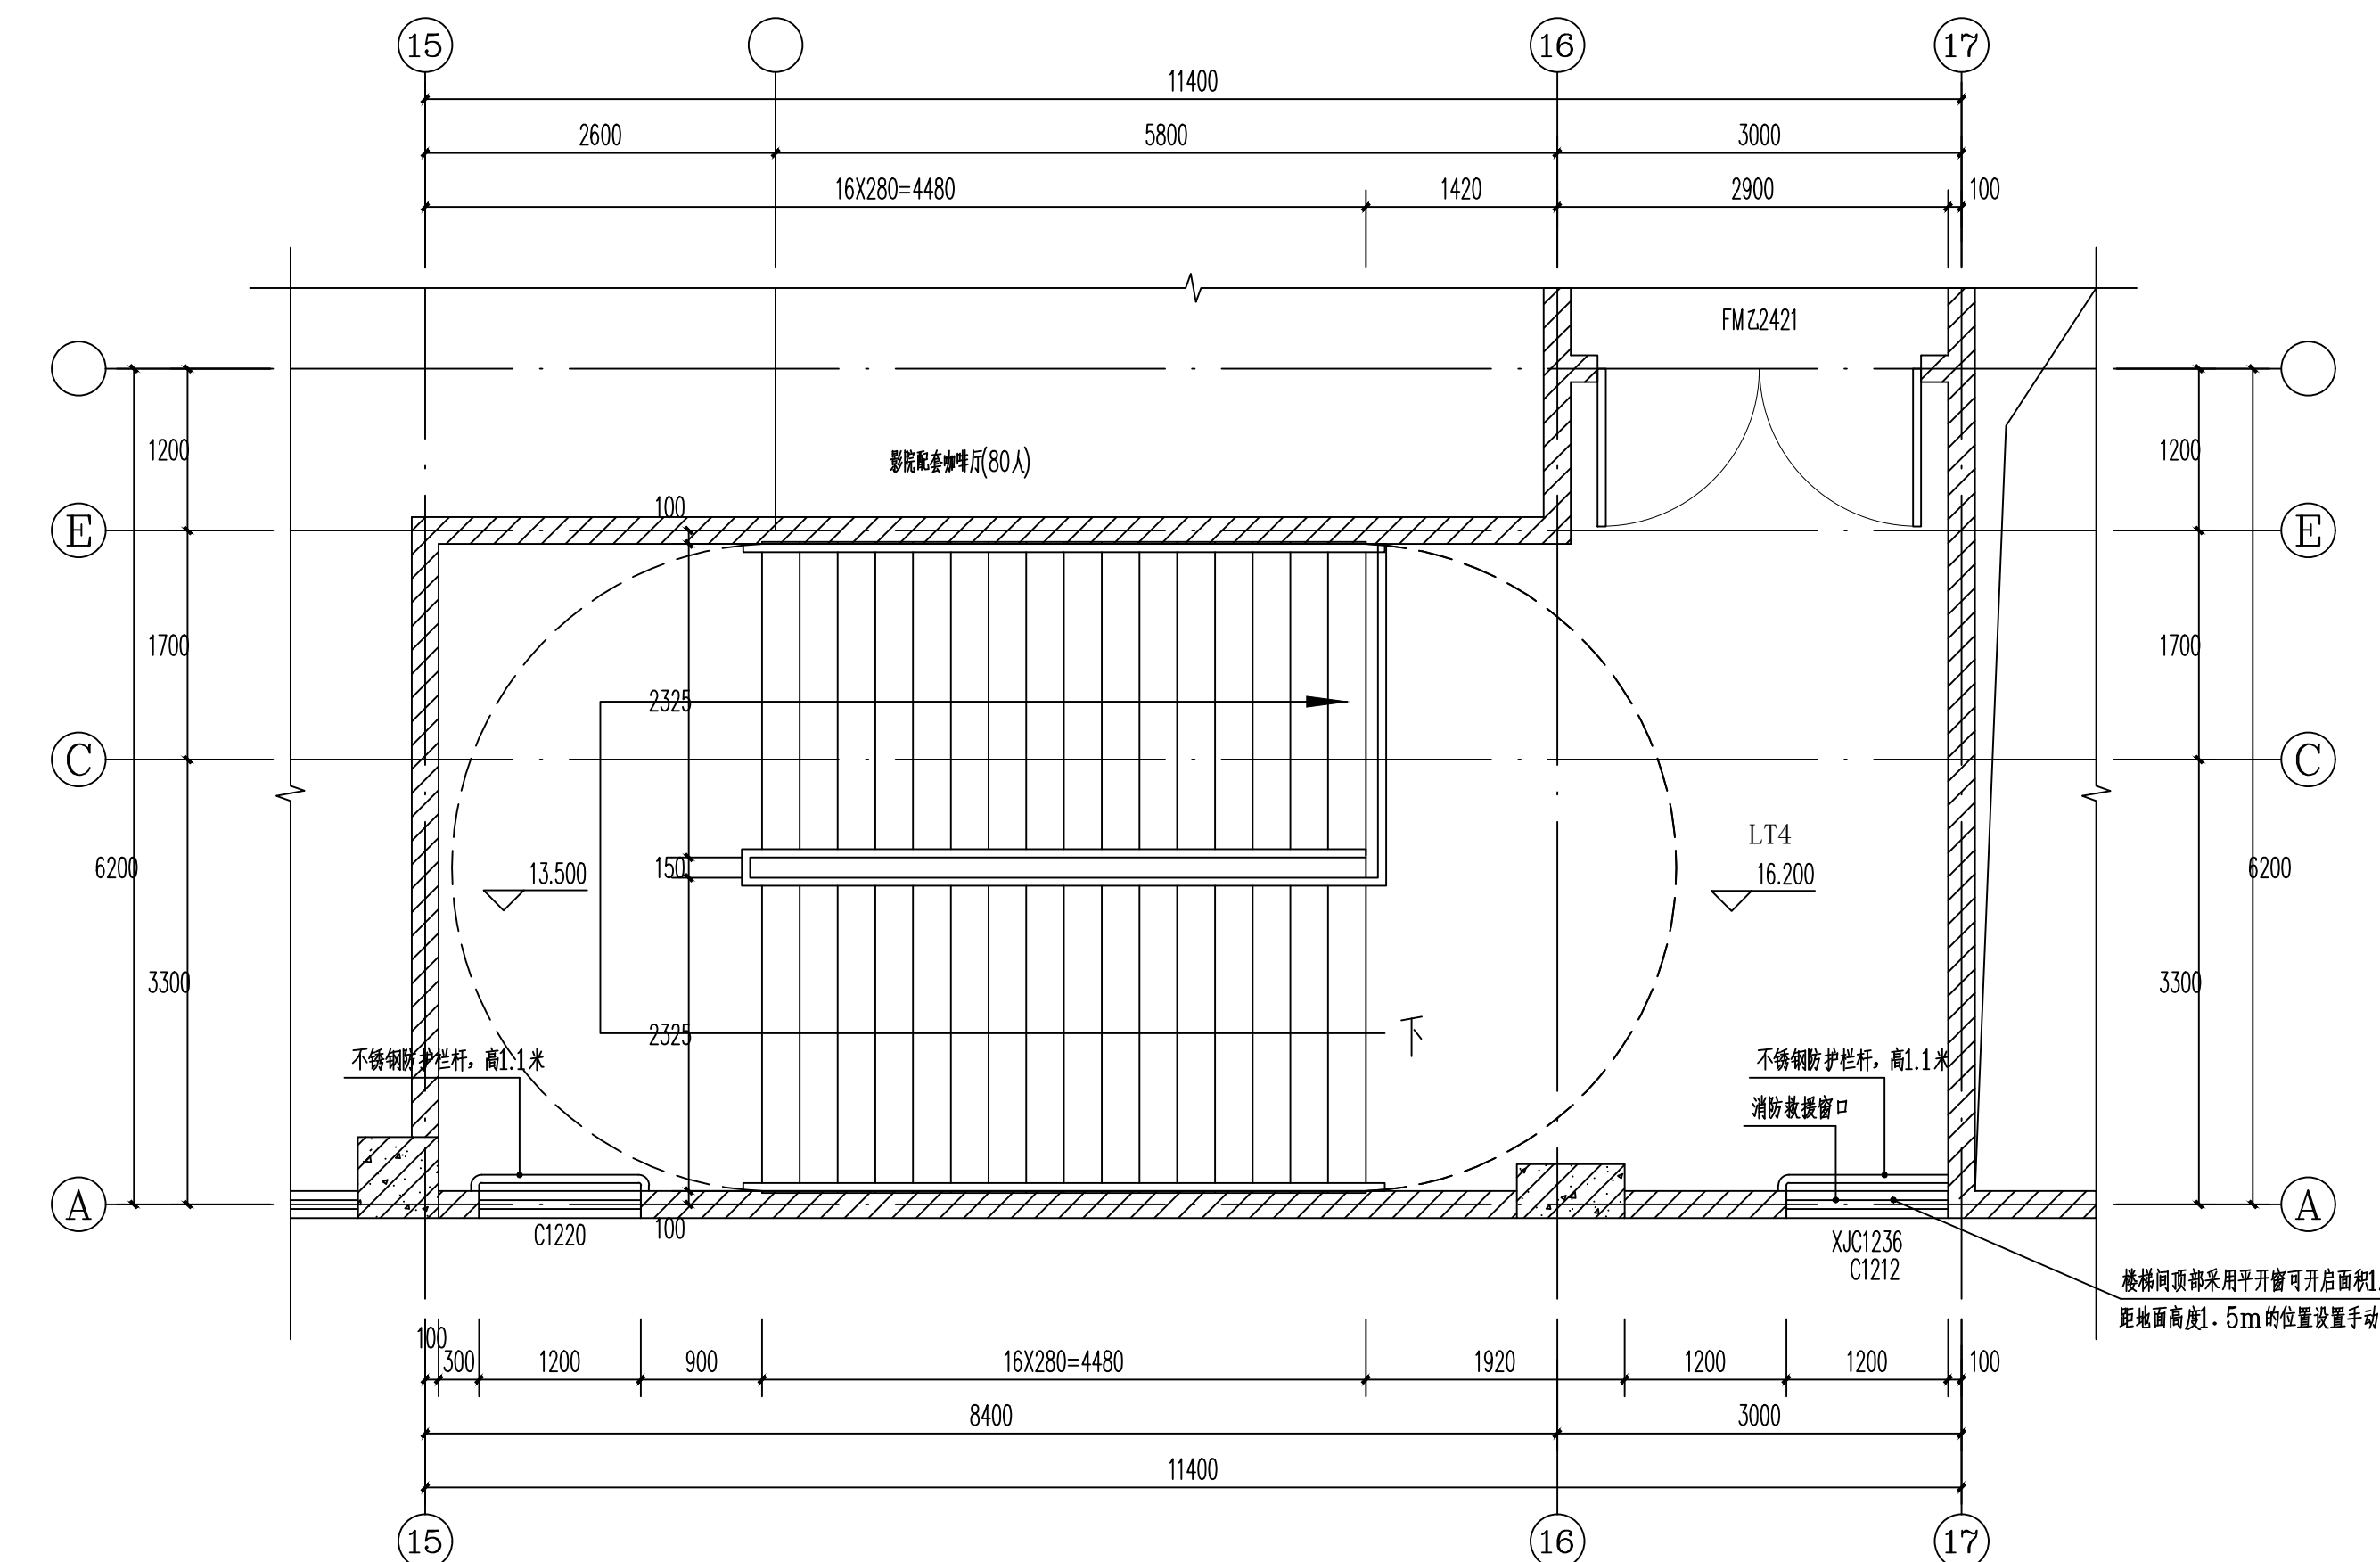


LT4楼梯间四层平面图 1:50

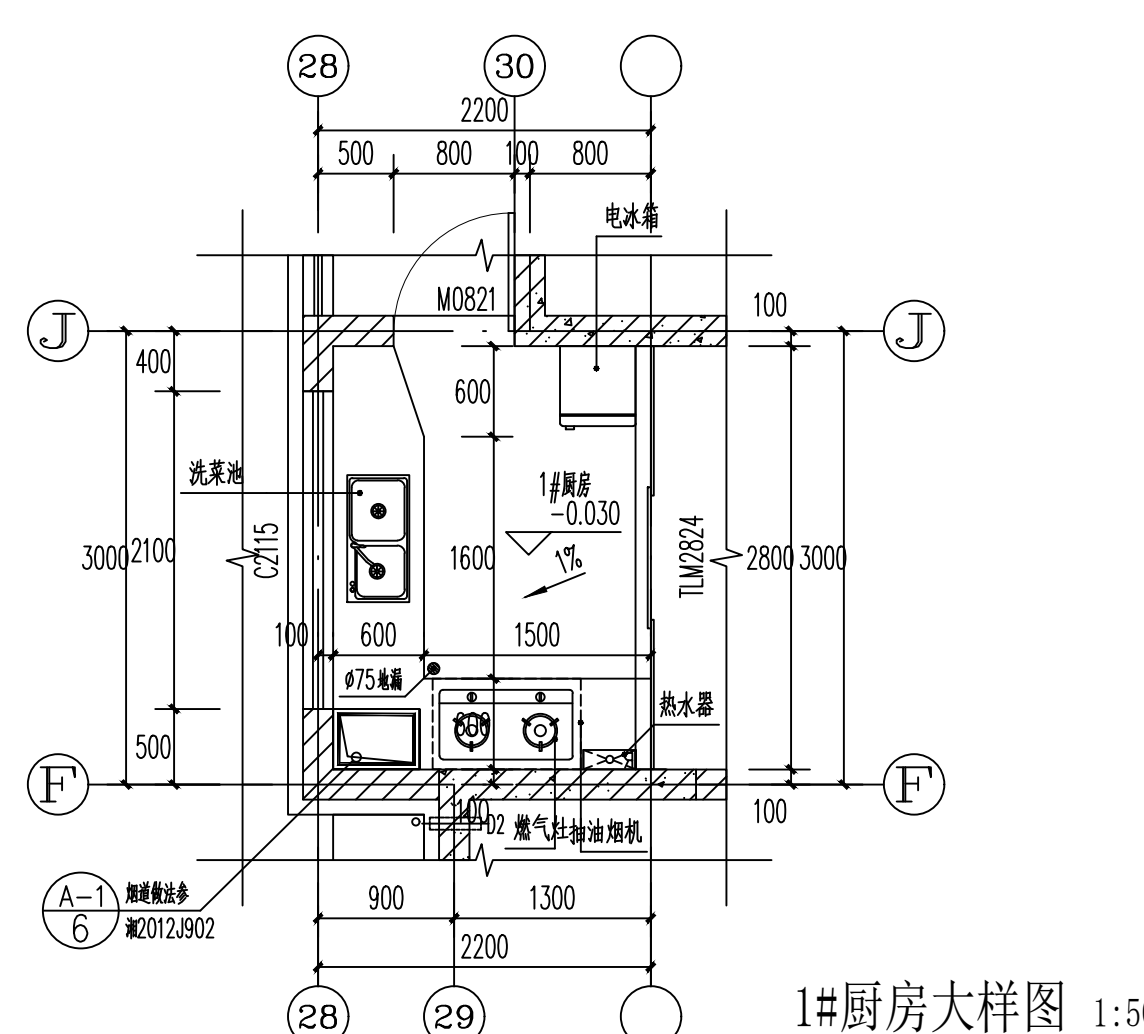


1#厨房大样图 1:50

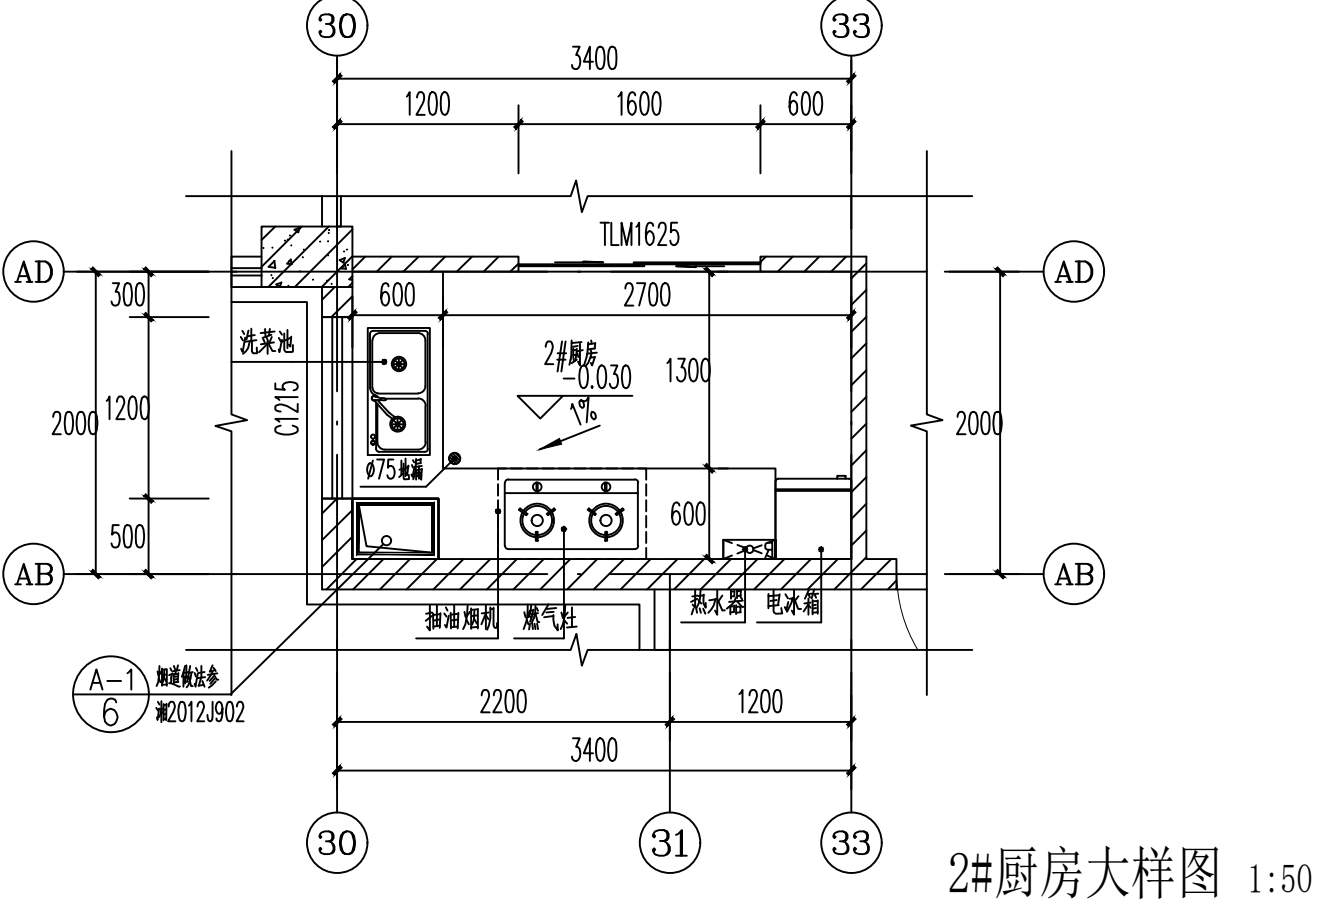


2#厨房大样图 1:50

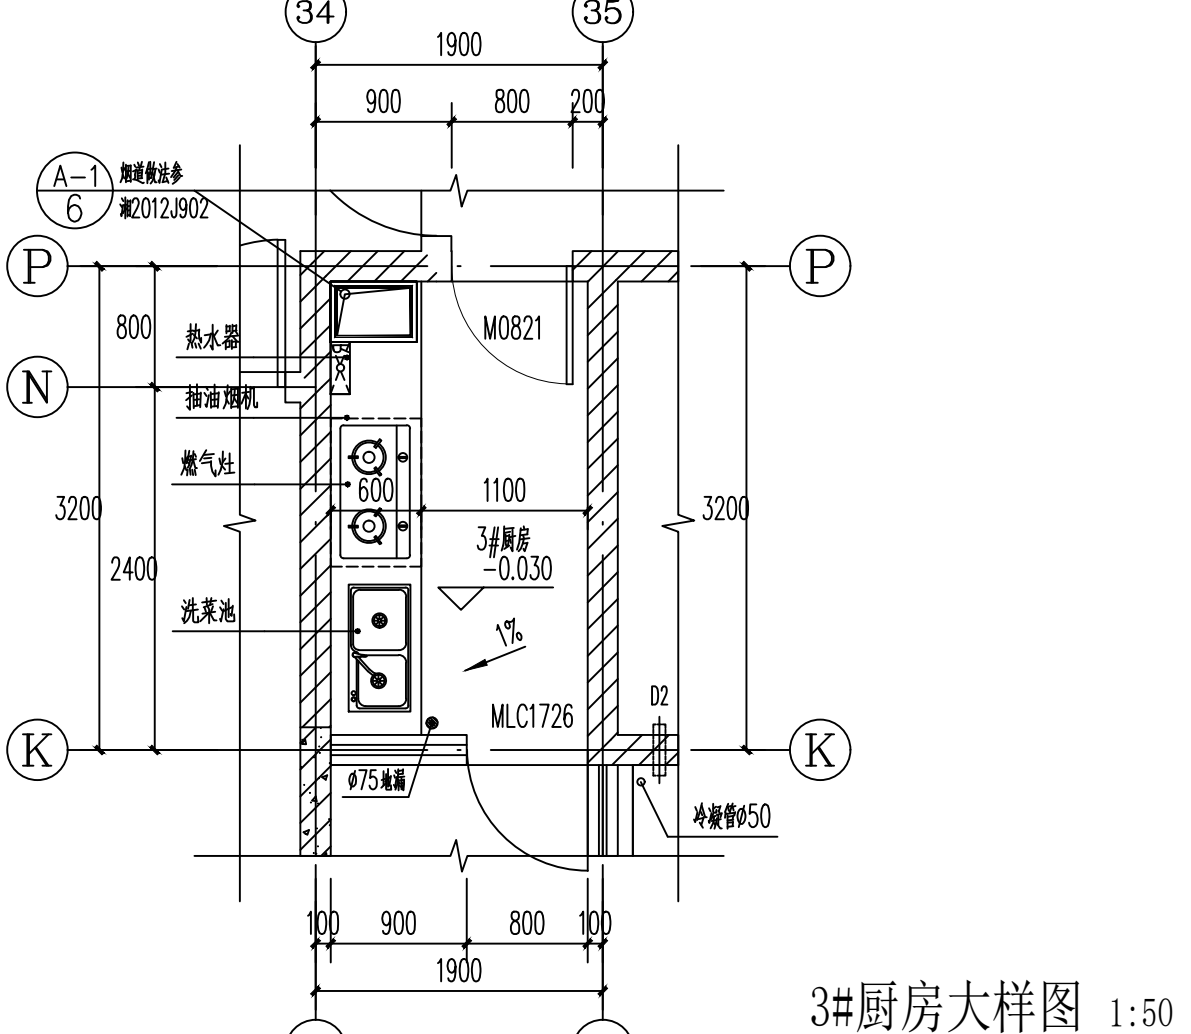

3#厨房大样图 1:50

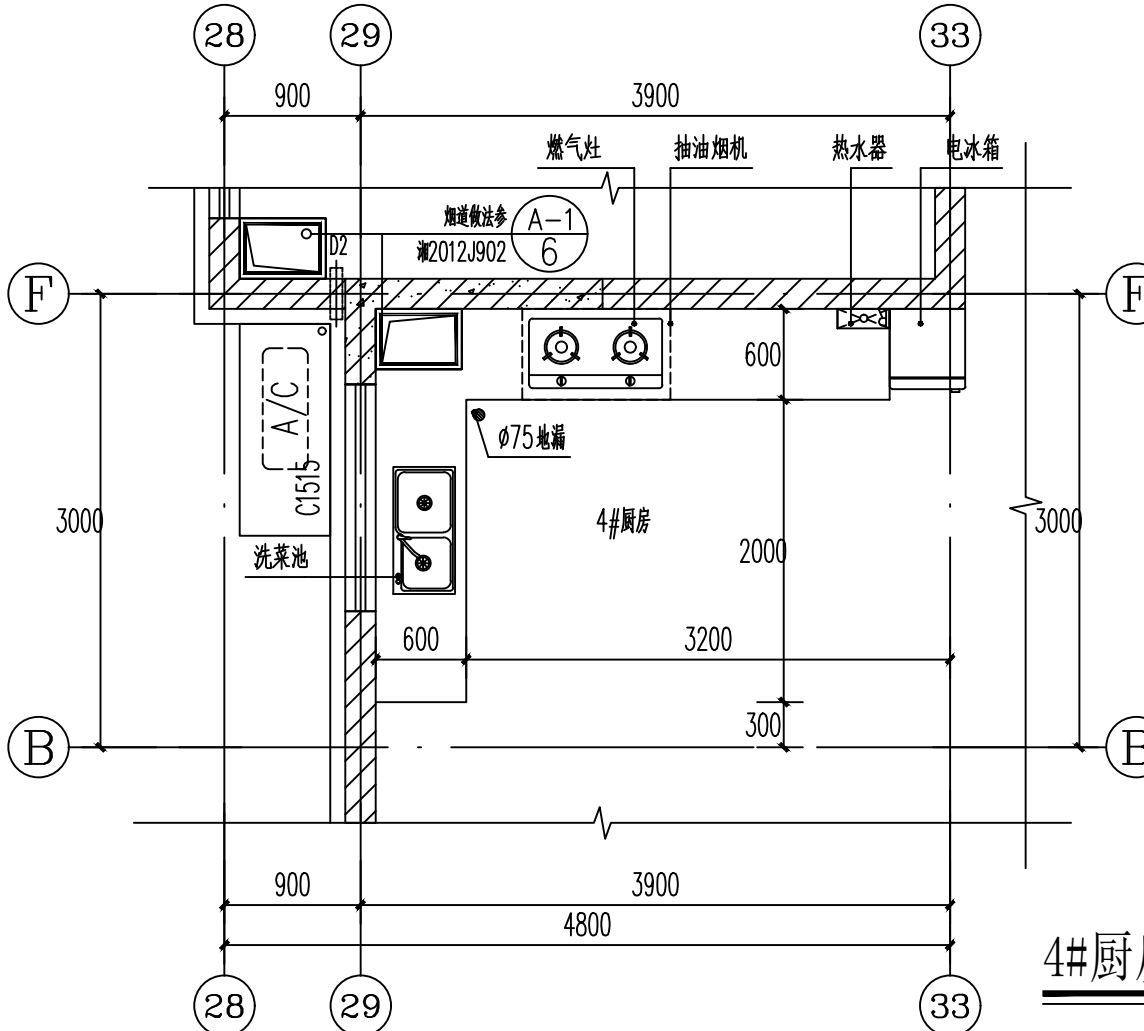

4#厨房大样图 1:50

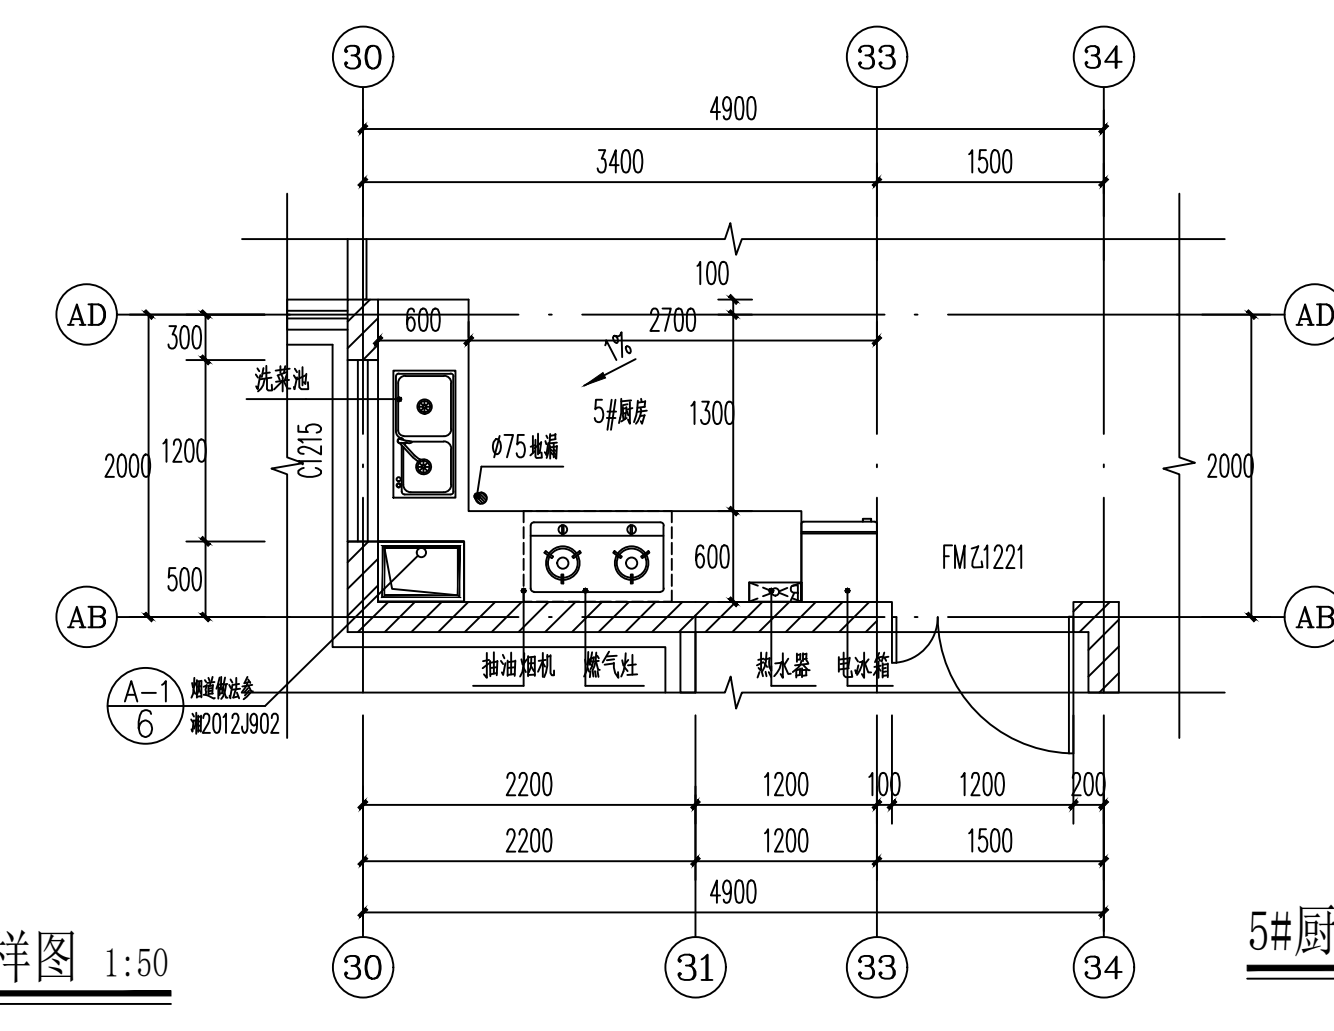

5#厨房大样图 1:50

建设单位/CLIENT:

麻阳苗族自治县远桥房地产开发有限公司

项目名称/PROJECT:

远程国际

子项目名称/SUB-PROJECT:

远程国际

区位图/REGIONAL LOCATION MAP :



图纸名称/TITLE:

LT3、LT4楼梯间大样图二
厨房大样图

项目名称/PROJECT:

远程国际

设计 DESIGNED	古新辉	古新辉
校对 CHECKED	吴新红	吴新红
专业负责人 CHIEF	吴志刚	吴志刚
项目负责人 PROJECT CHIEF	吴志刚	吴志刚
审核 IDENTIFIED	黄展优	黄展优
审定 APPROVED	李 坚	李 坚

业务号/JOB NO.

设计阶段/STATUS: 施工图

专业/DISCIPLINE: 建筑

比例/
SCALE: 1: 100 规格/
SIZE: A1

出图日期/DATE: 2021.06

图号/DRAWING NO. JS-31

版次 NO.	修改内容 DESCRIPTION	日期 DATE

条形码/BARCODE:

版权所有，不得复制、套用。
ALL RIGHTS RESERVED, DON'T COPIED, REPRODUCED.