


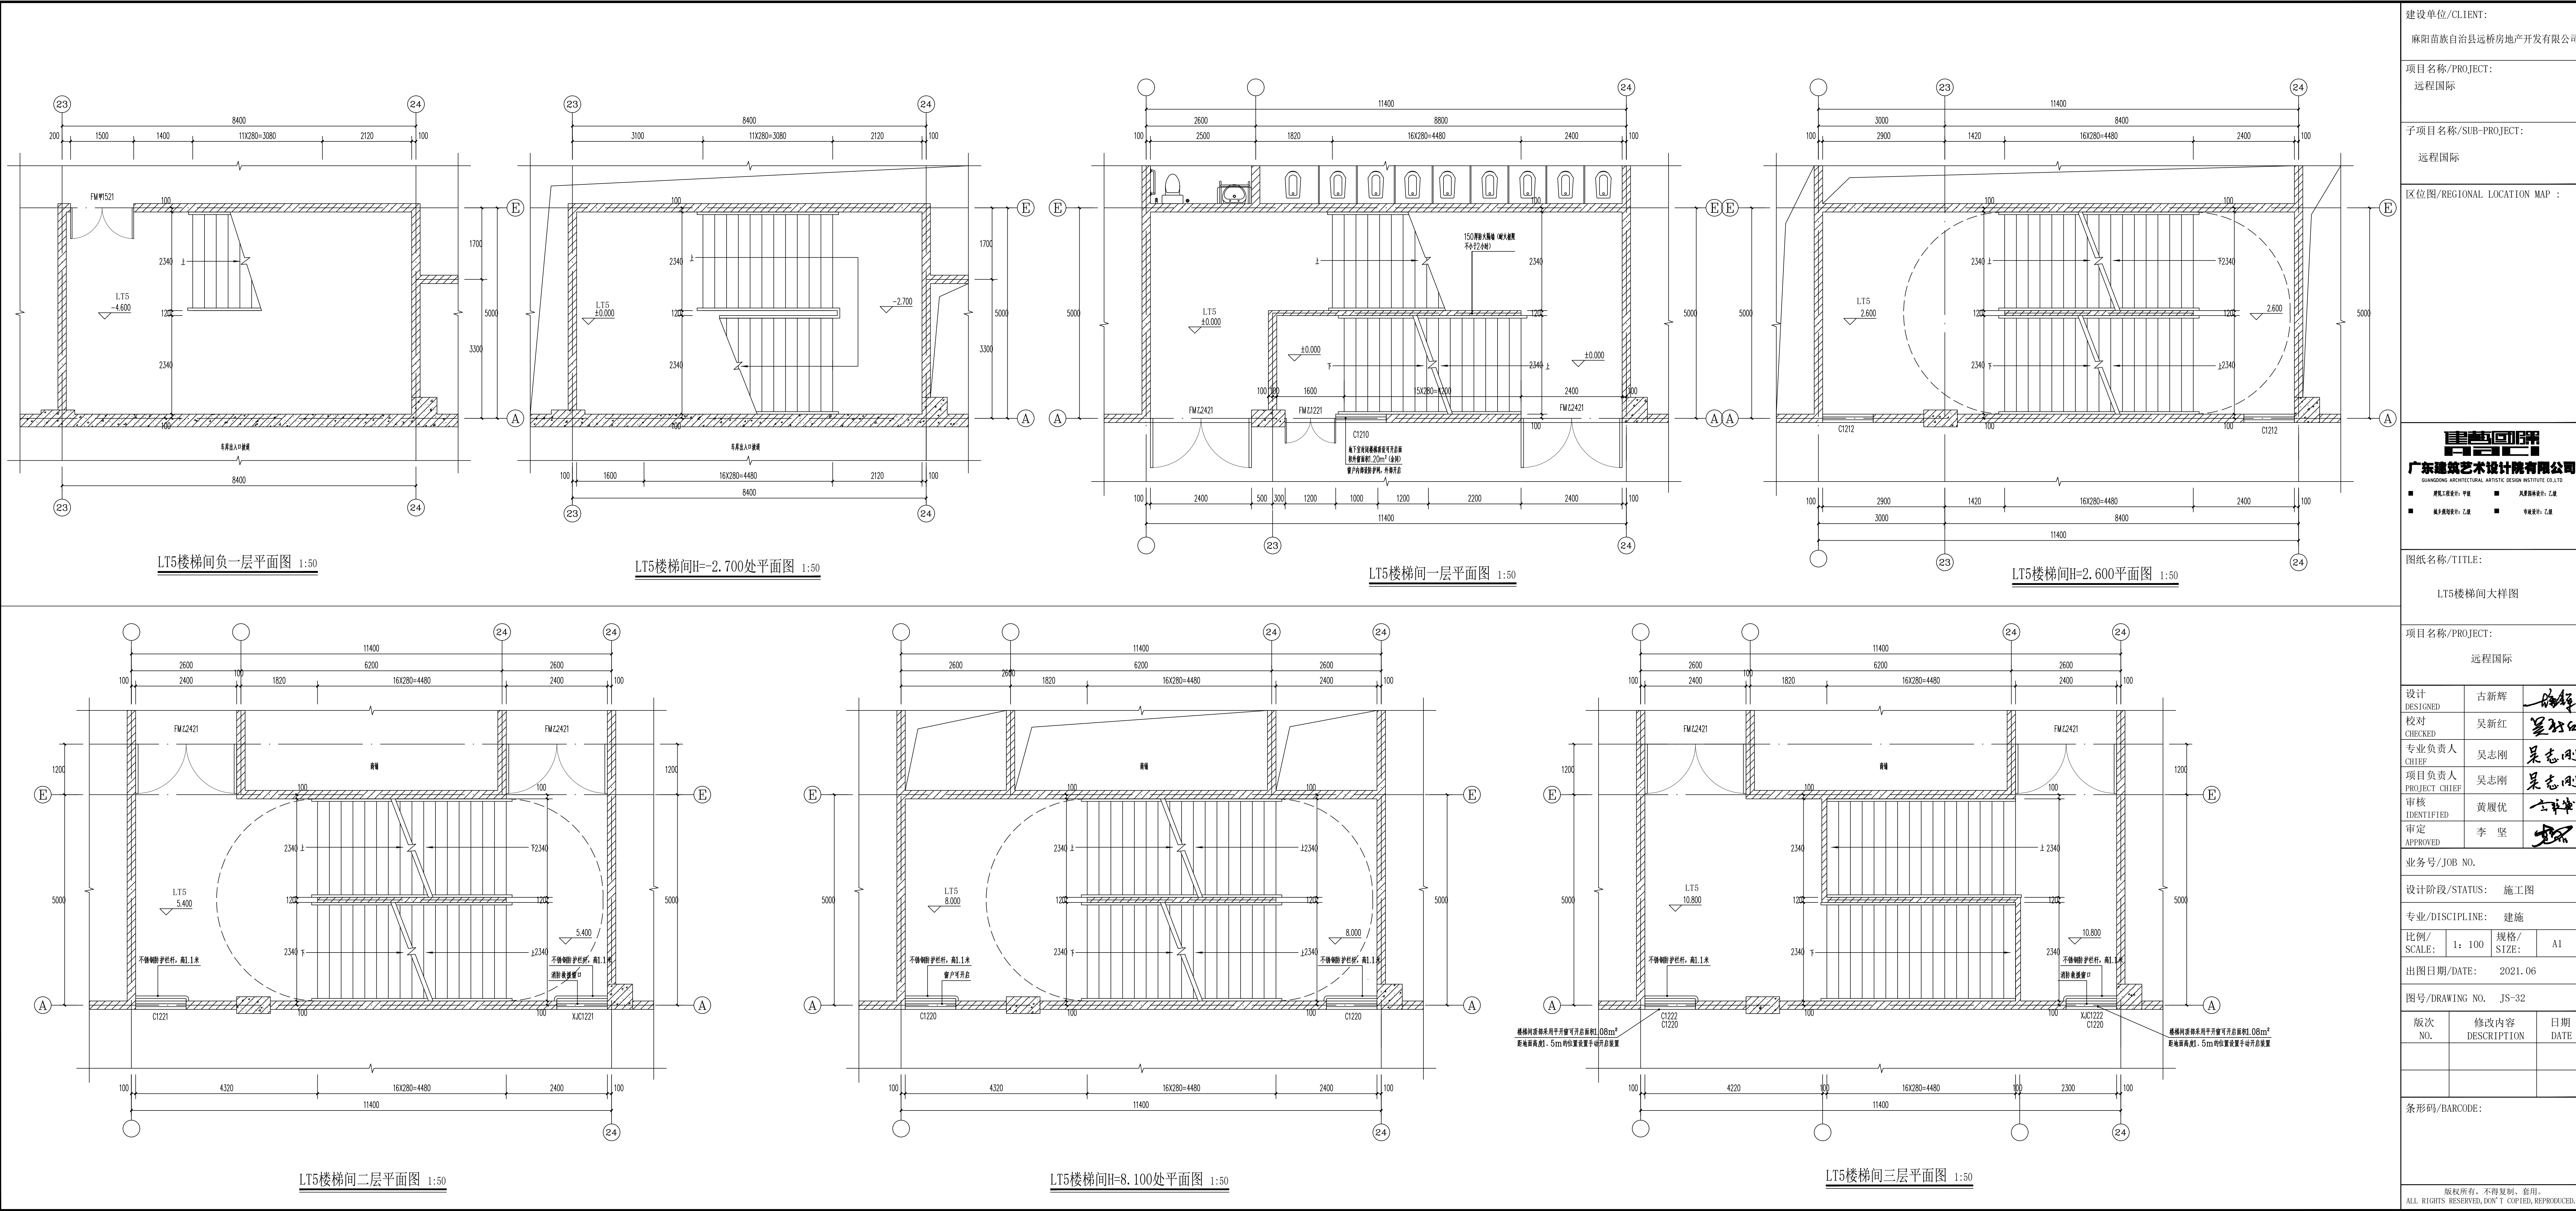

建设单位/CLIENT:

麻阳苗族自治县远桥房地产开发有限公司

项目名称/PROJECT:

远程国际

子项目名称/SUB-PROJECT:

远程国际

区位图/REGIONAL LOCATION MAP :

图纸名称/TITLE:

LT5楼梯间大样图

项目名称/PROJECT:

远程国际

设计DESIGNED

古新辉

校对CHECKED

吴新红

专业负责人CHIEF

吴志刚

项目负责人PROJECT CHIEF

吴志刚

审核IDENTIFIED

黄展优

审定APPROVED

李 坚

业务号/JOB NO.

设计阶段/STATUS:

施工图

专业/DISCIPLINE:

建施

比例/SCALE:

1: 100

规格/SIZE:

A1

出图日期/DATE:

2021. 06

图号/DRAWING NO.

JS-32

版次NO.

修改内容DESCRIPTION

日期DATE

条形码/BARCODE:

版权所有，不得复制、套用。
ALL RIGHTS RESERVED, DON'T COPIED, REPRODUCED.