
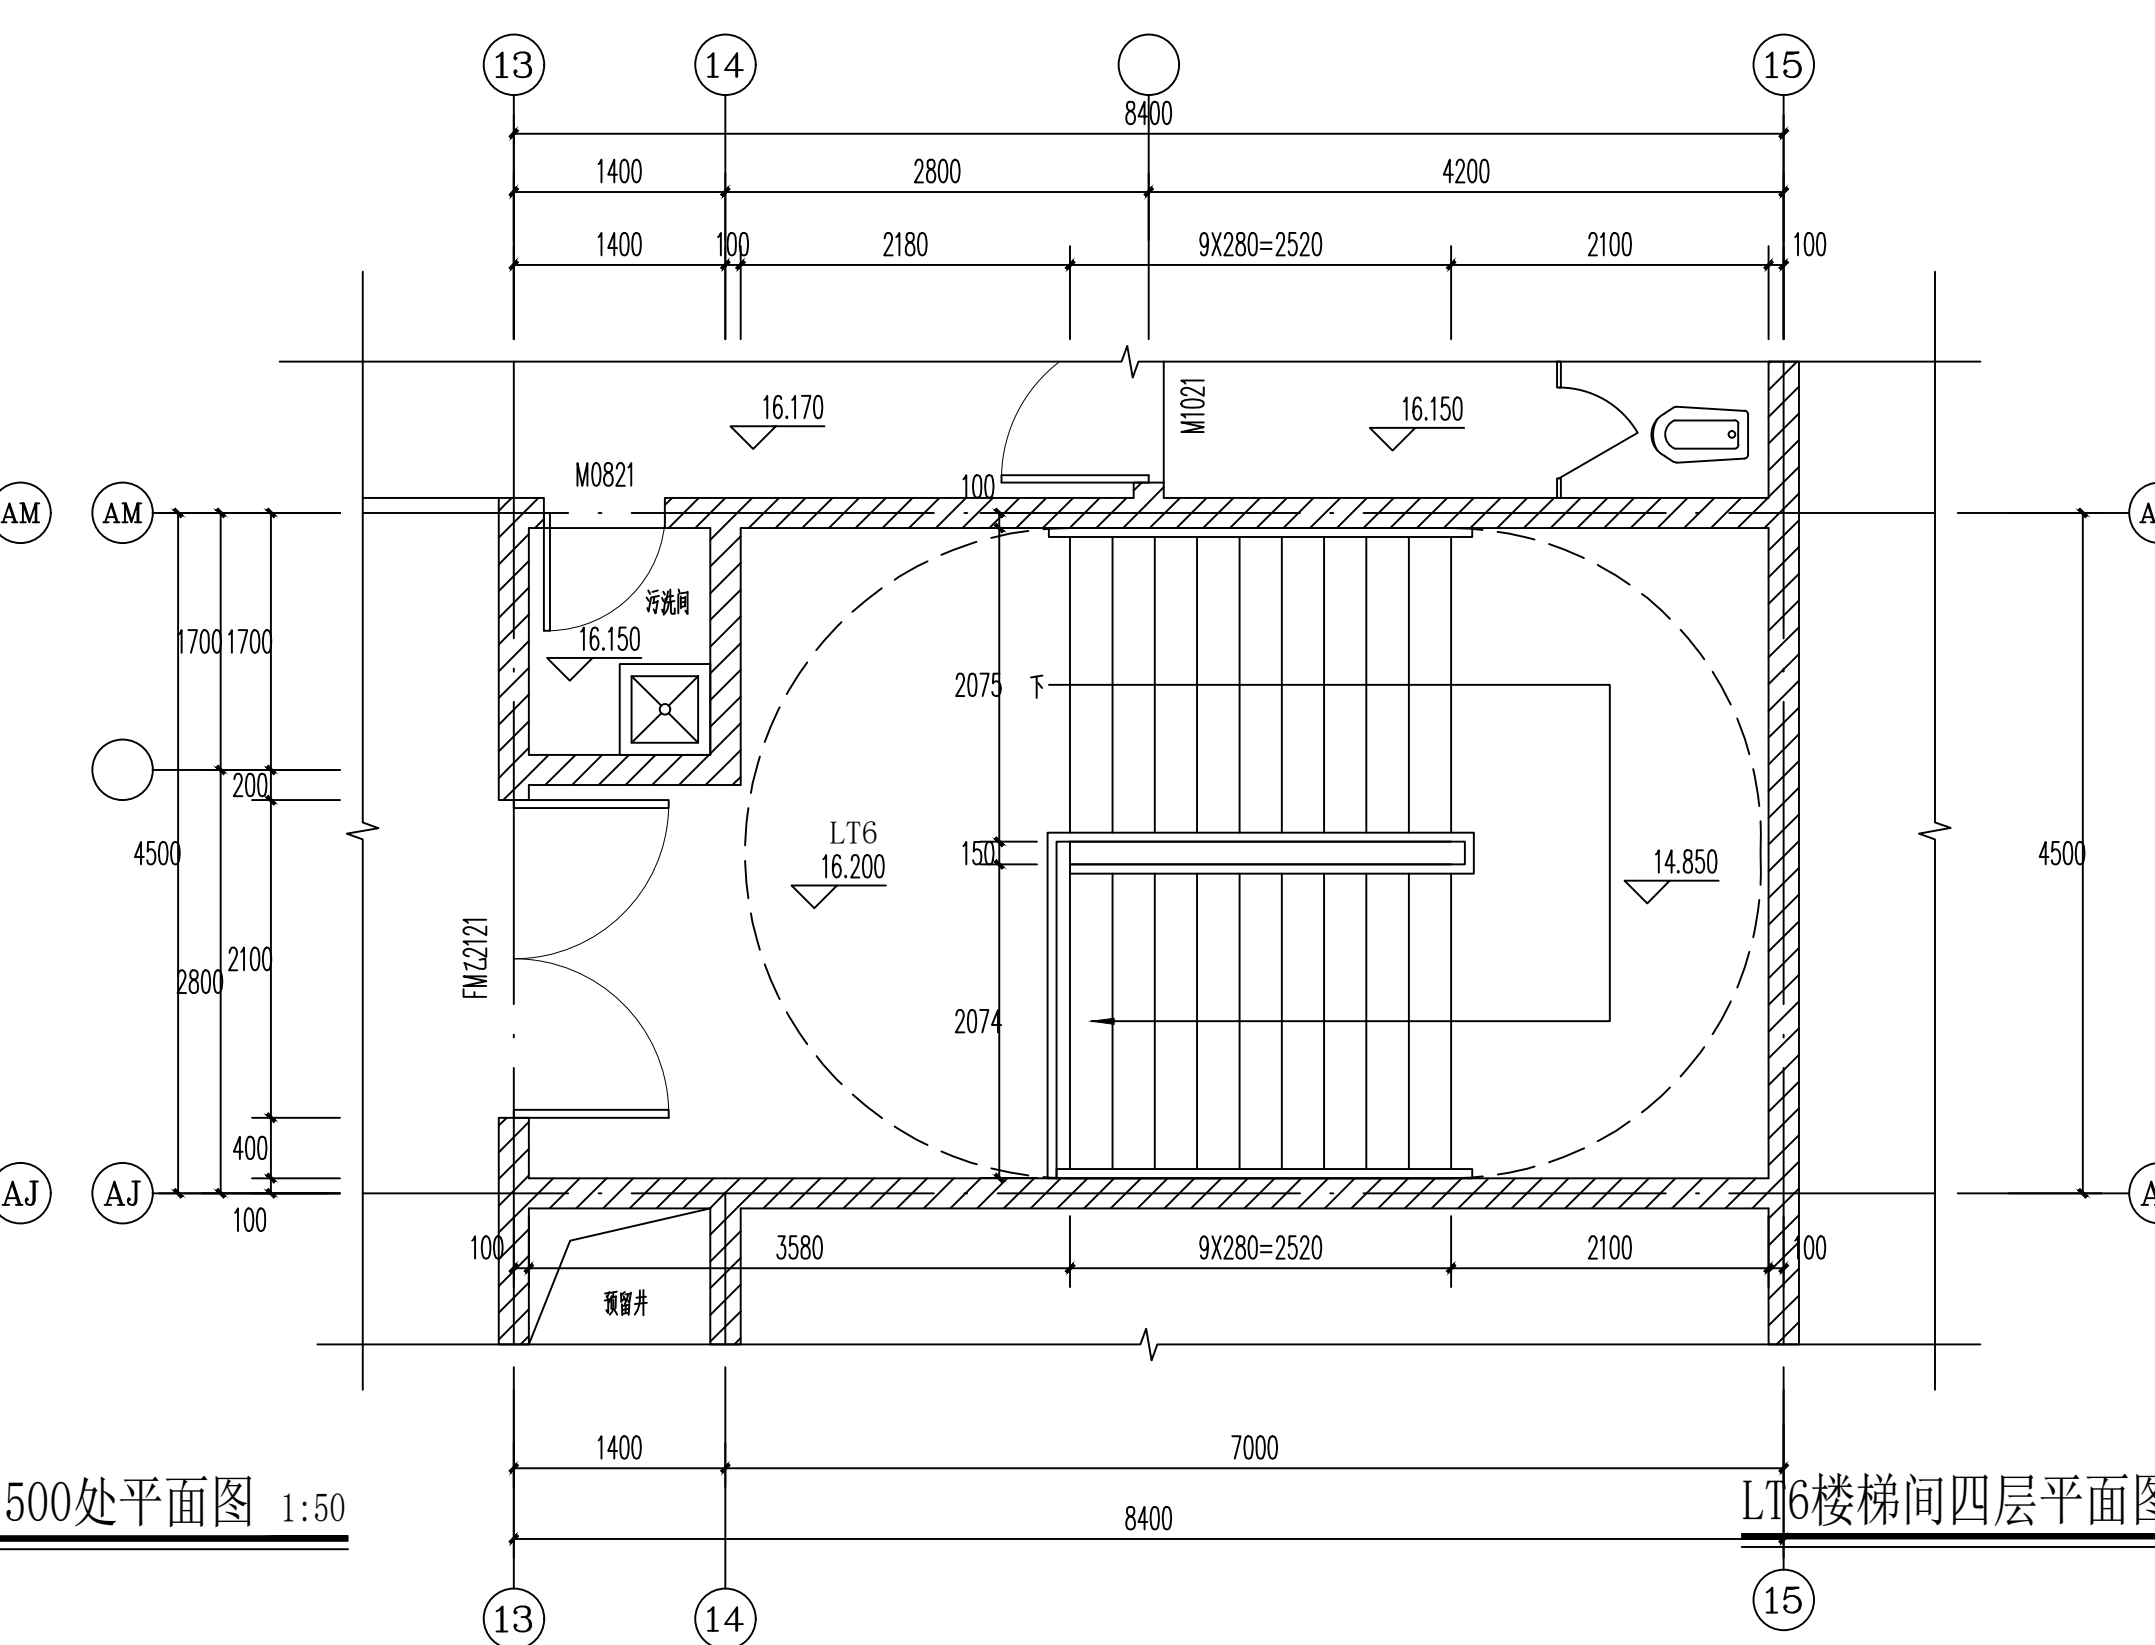
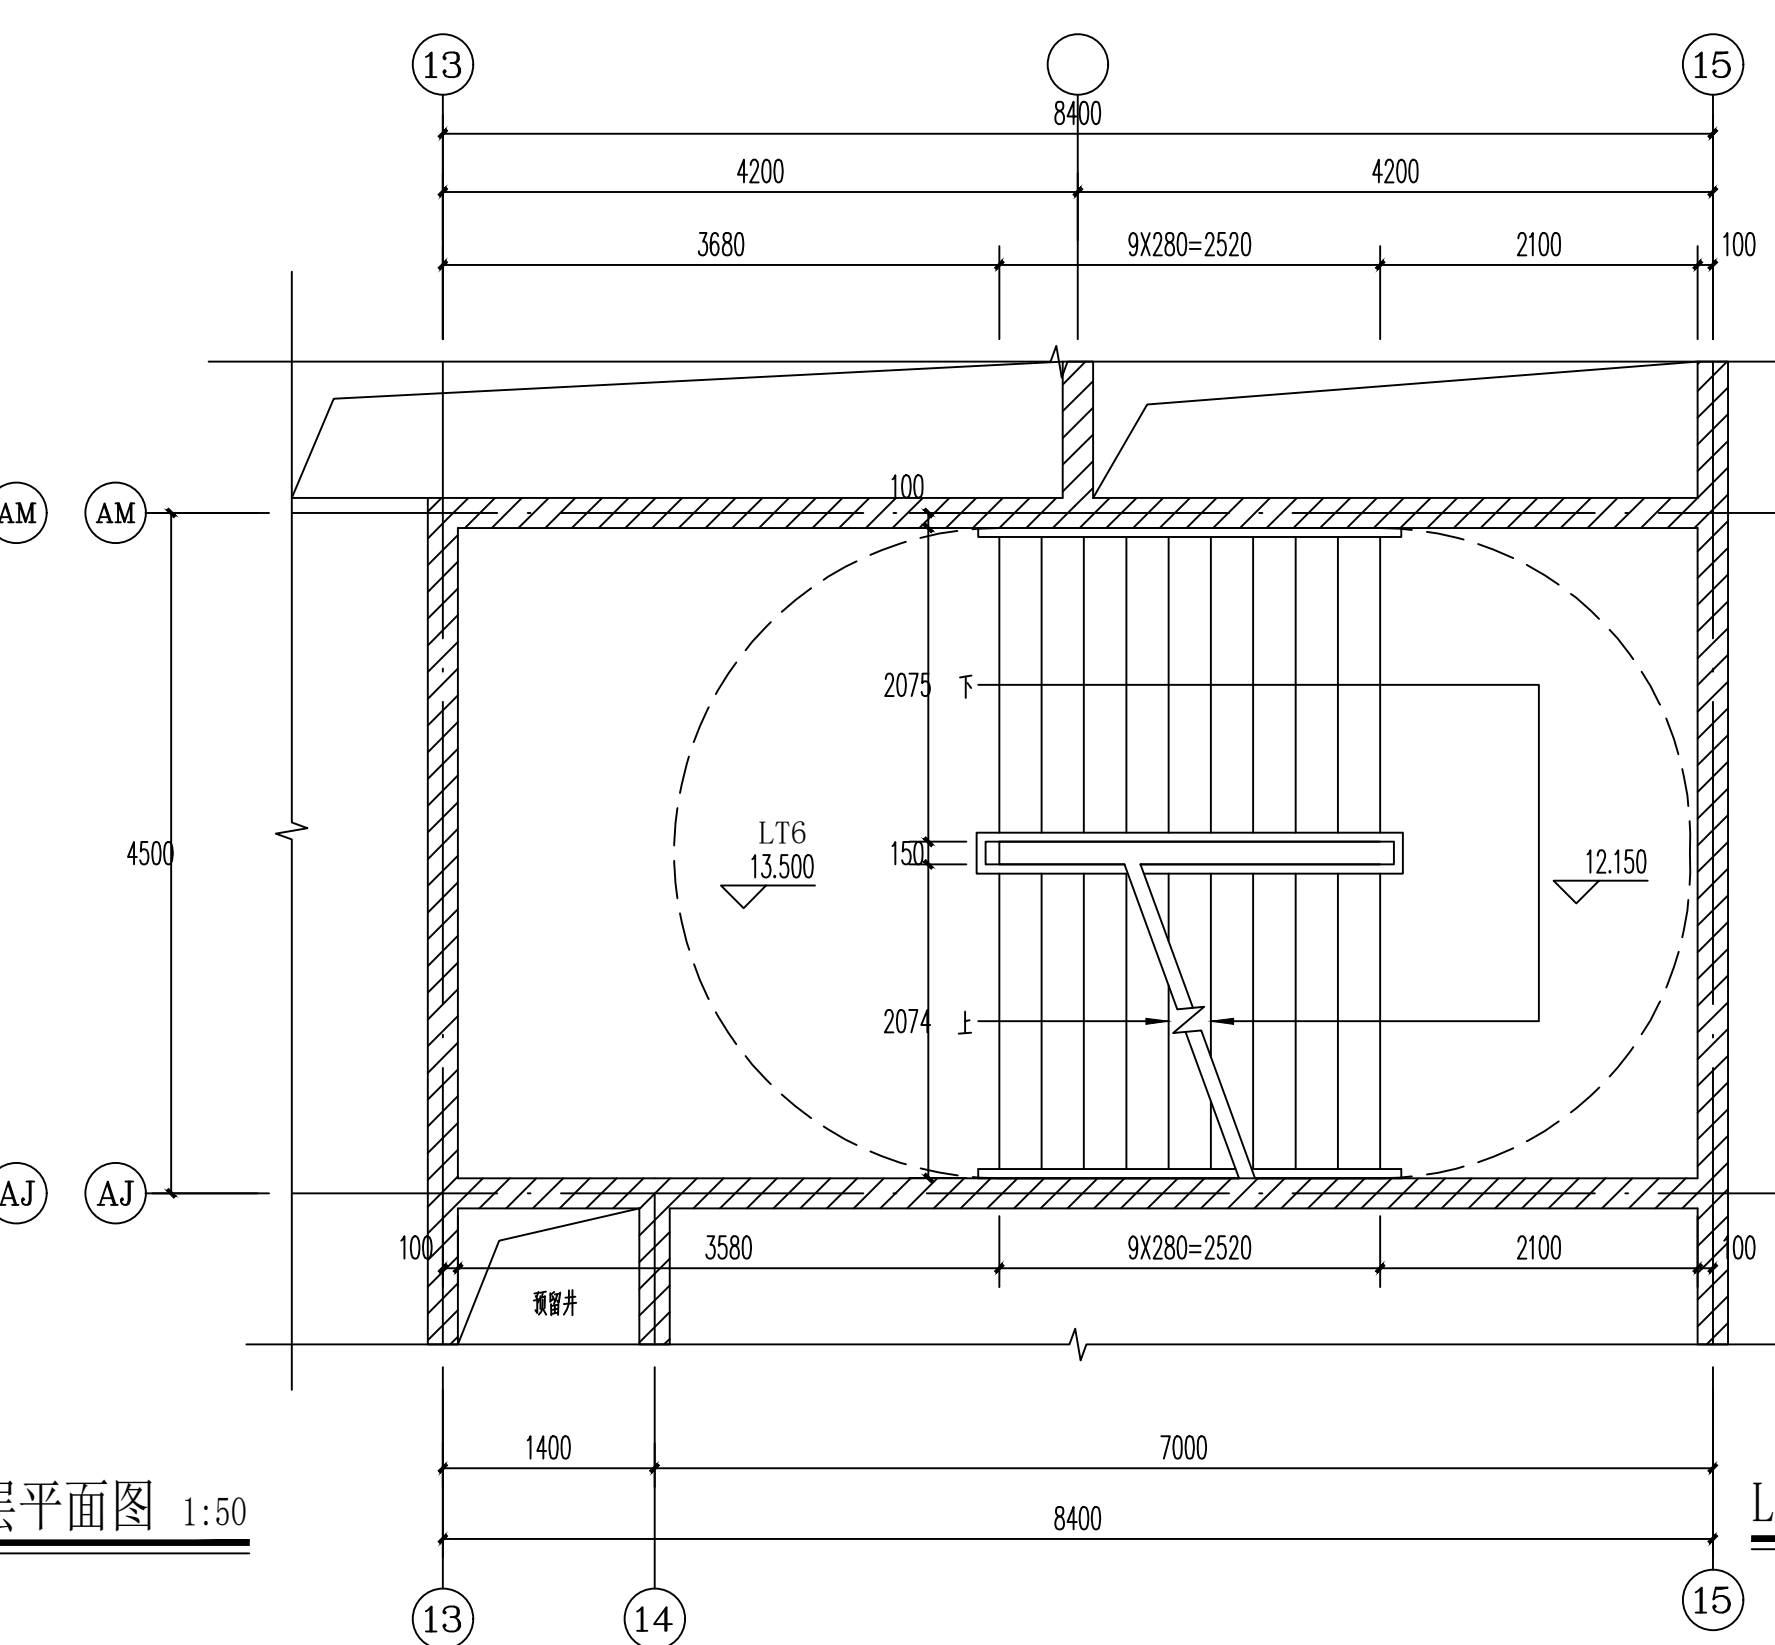
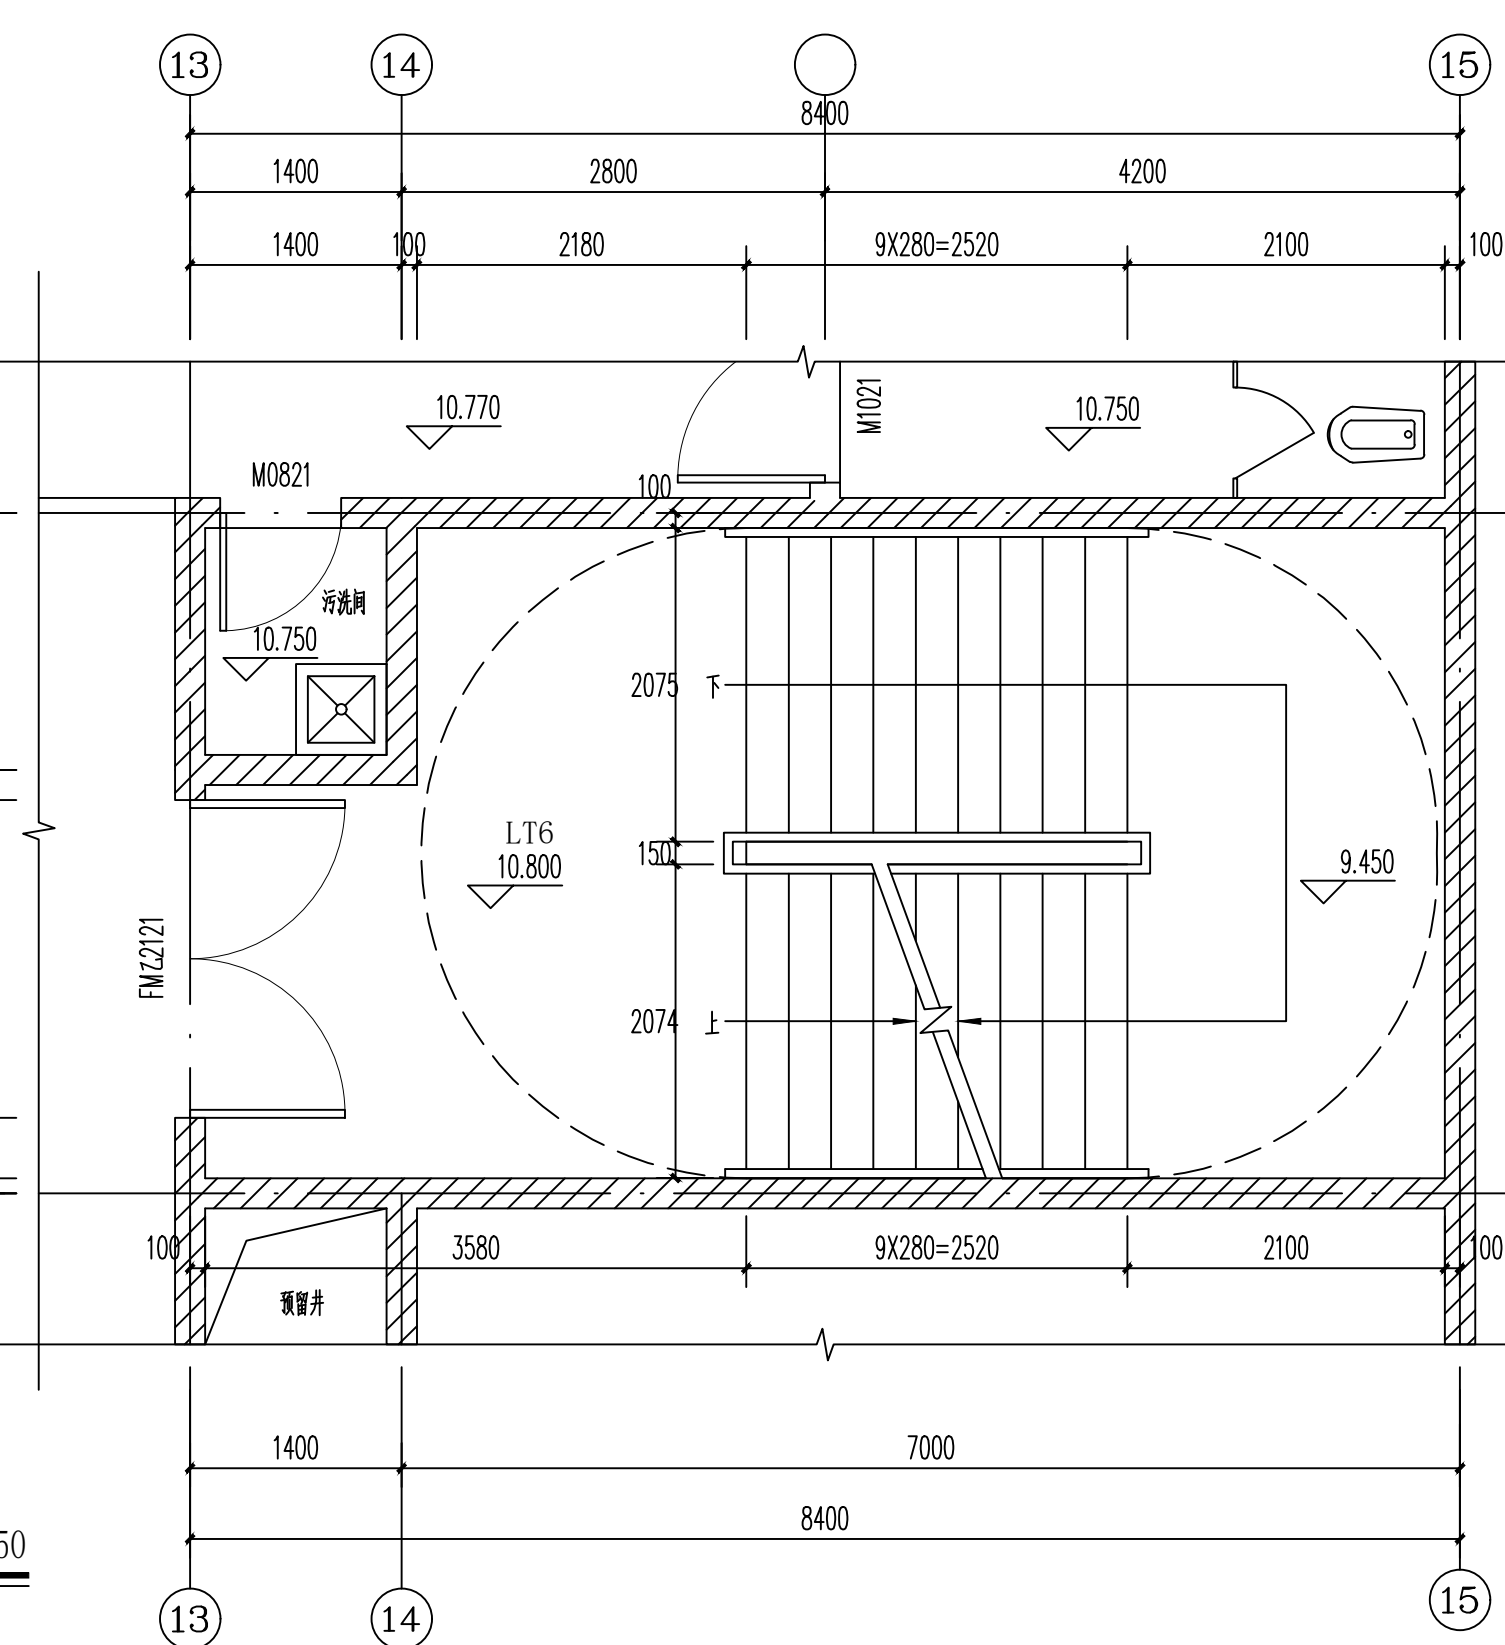
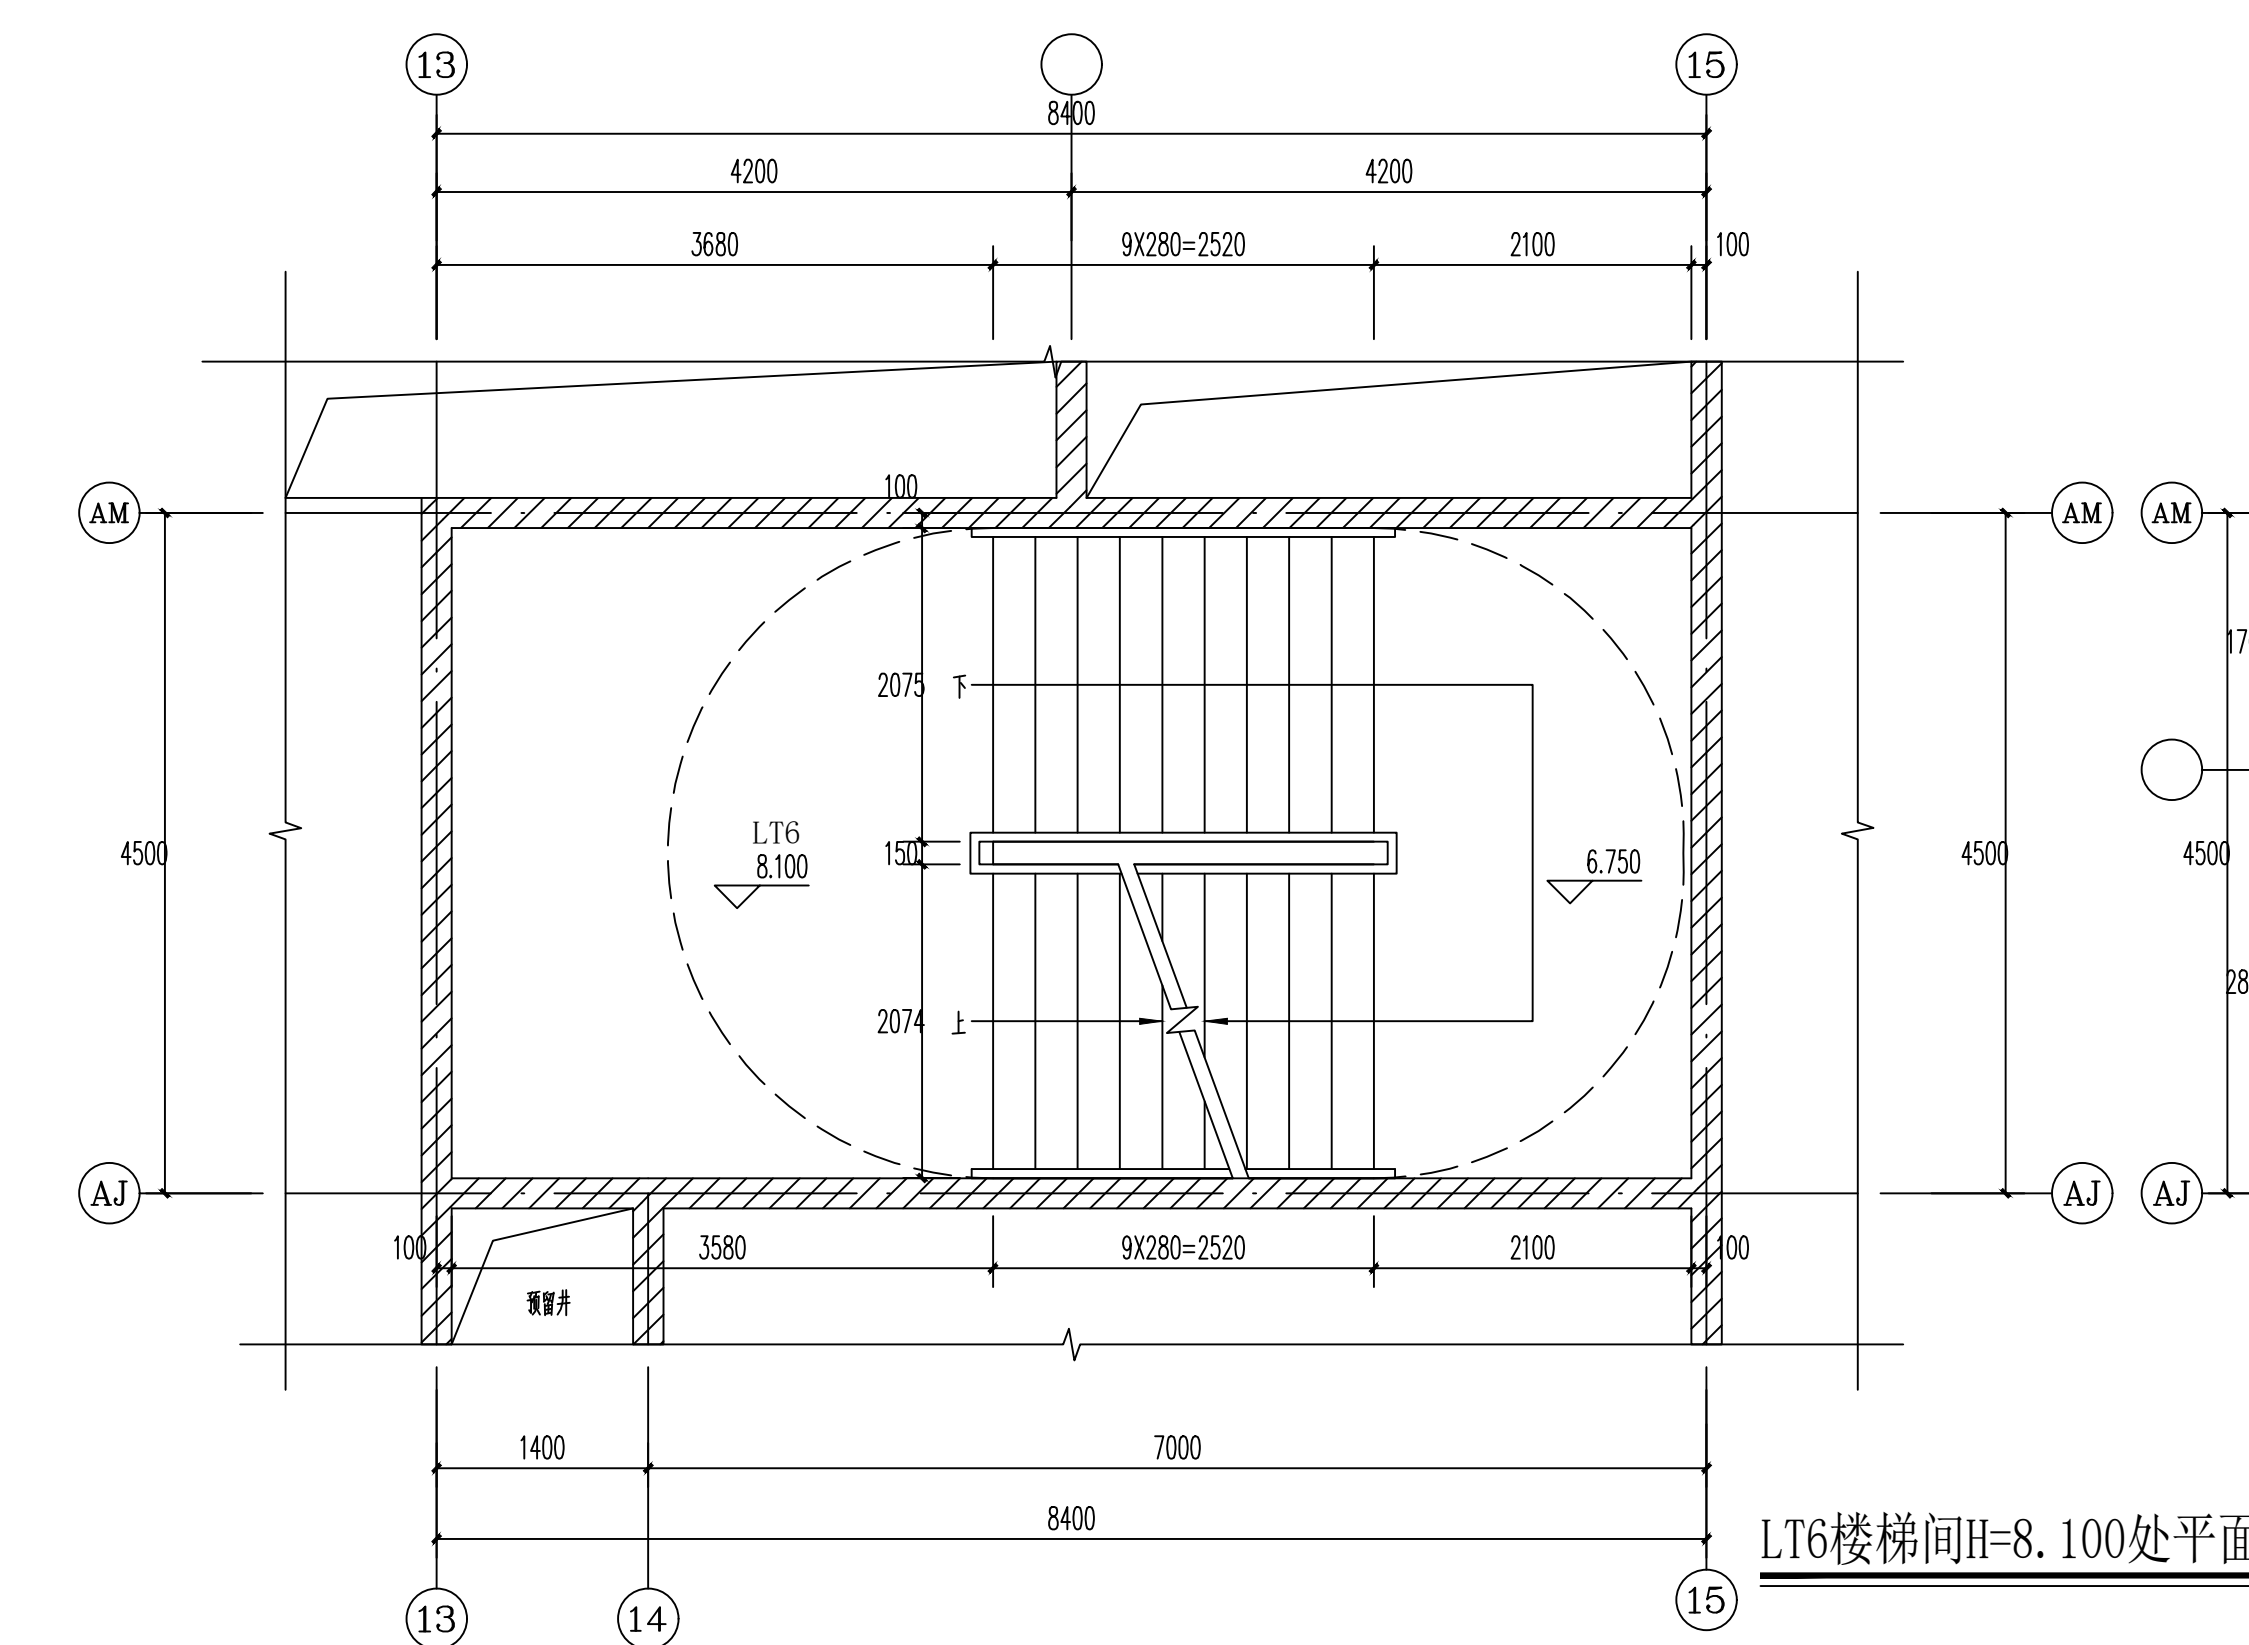
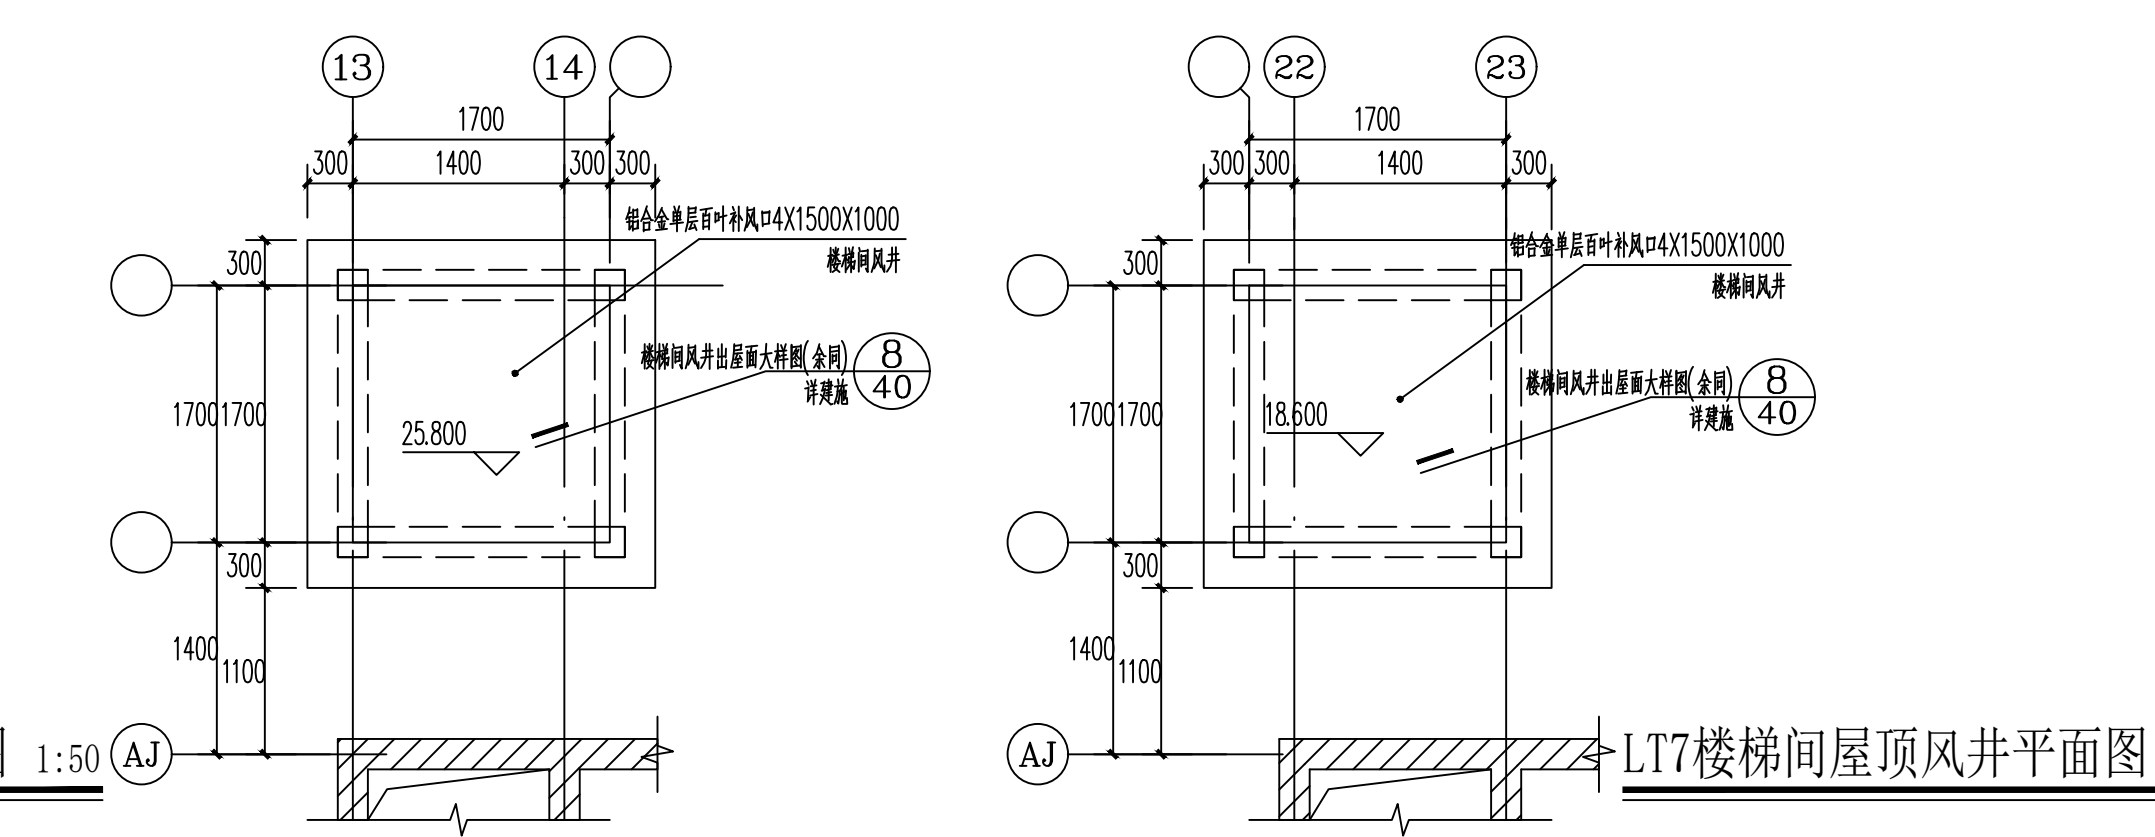
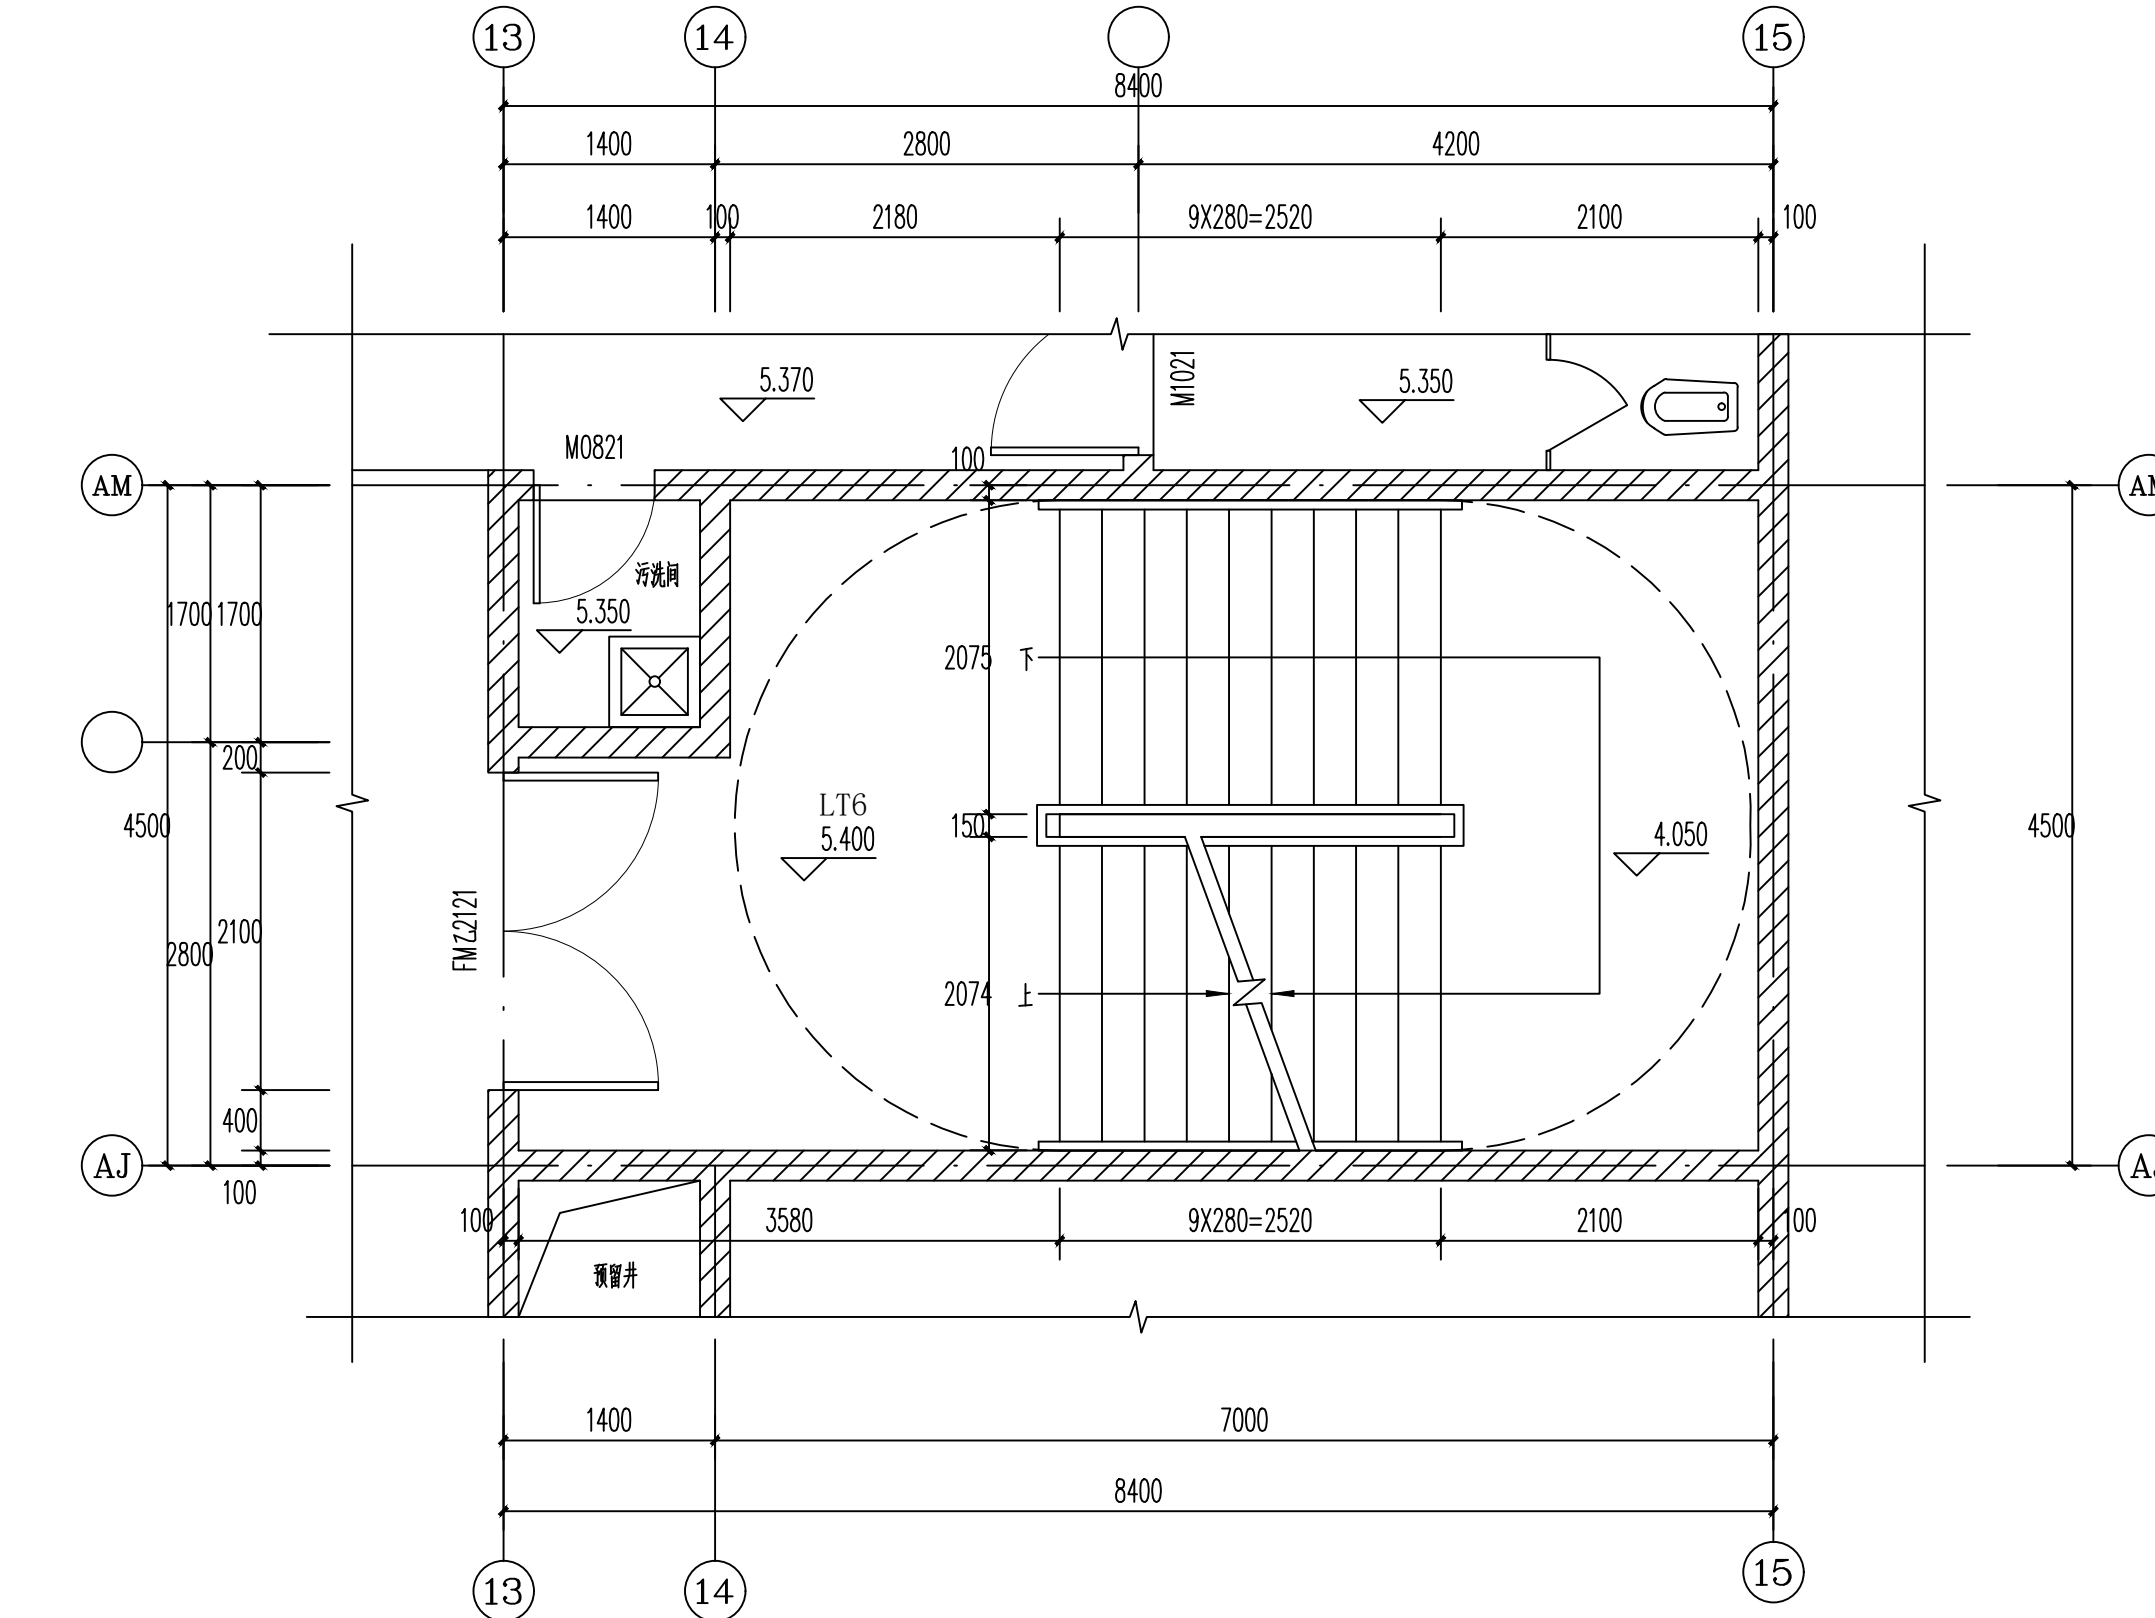
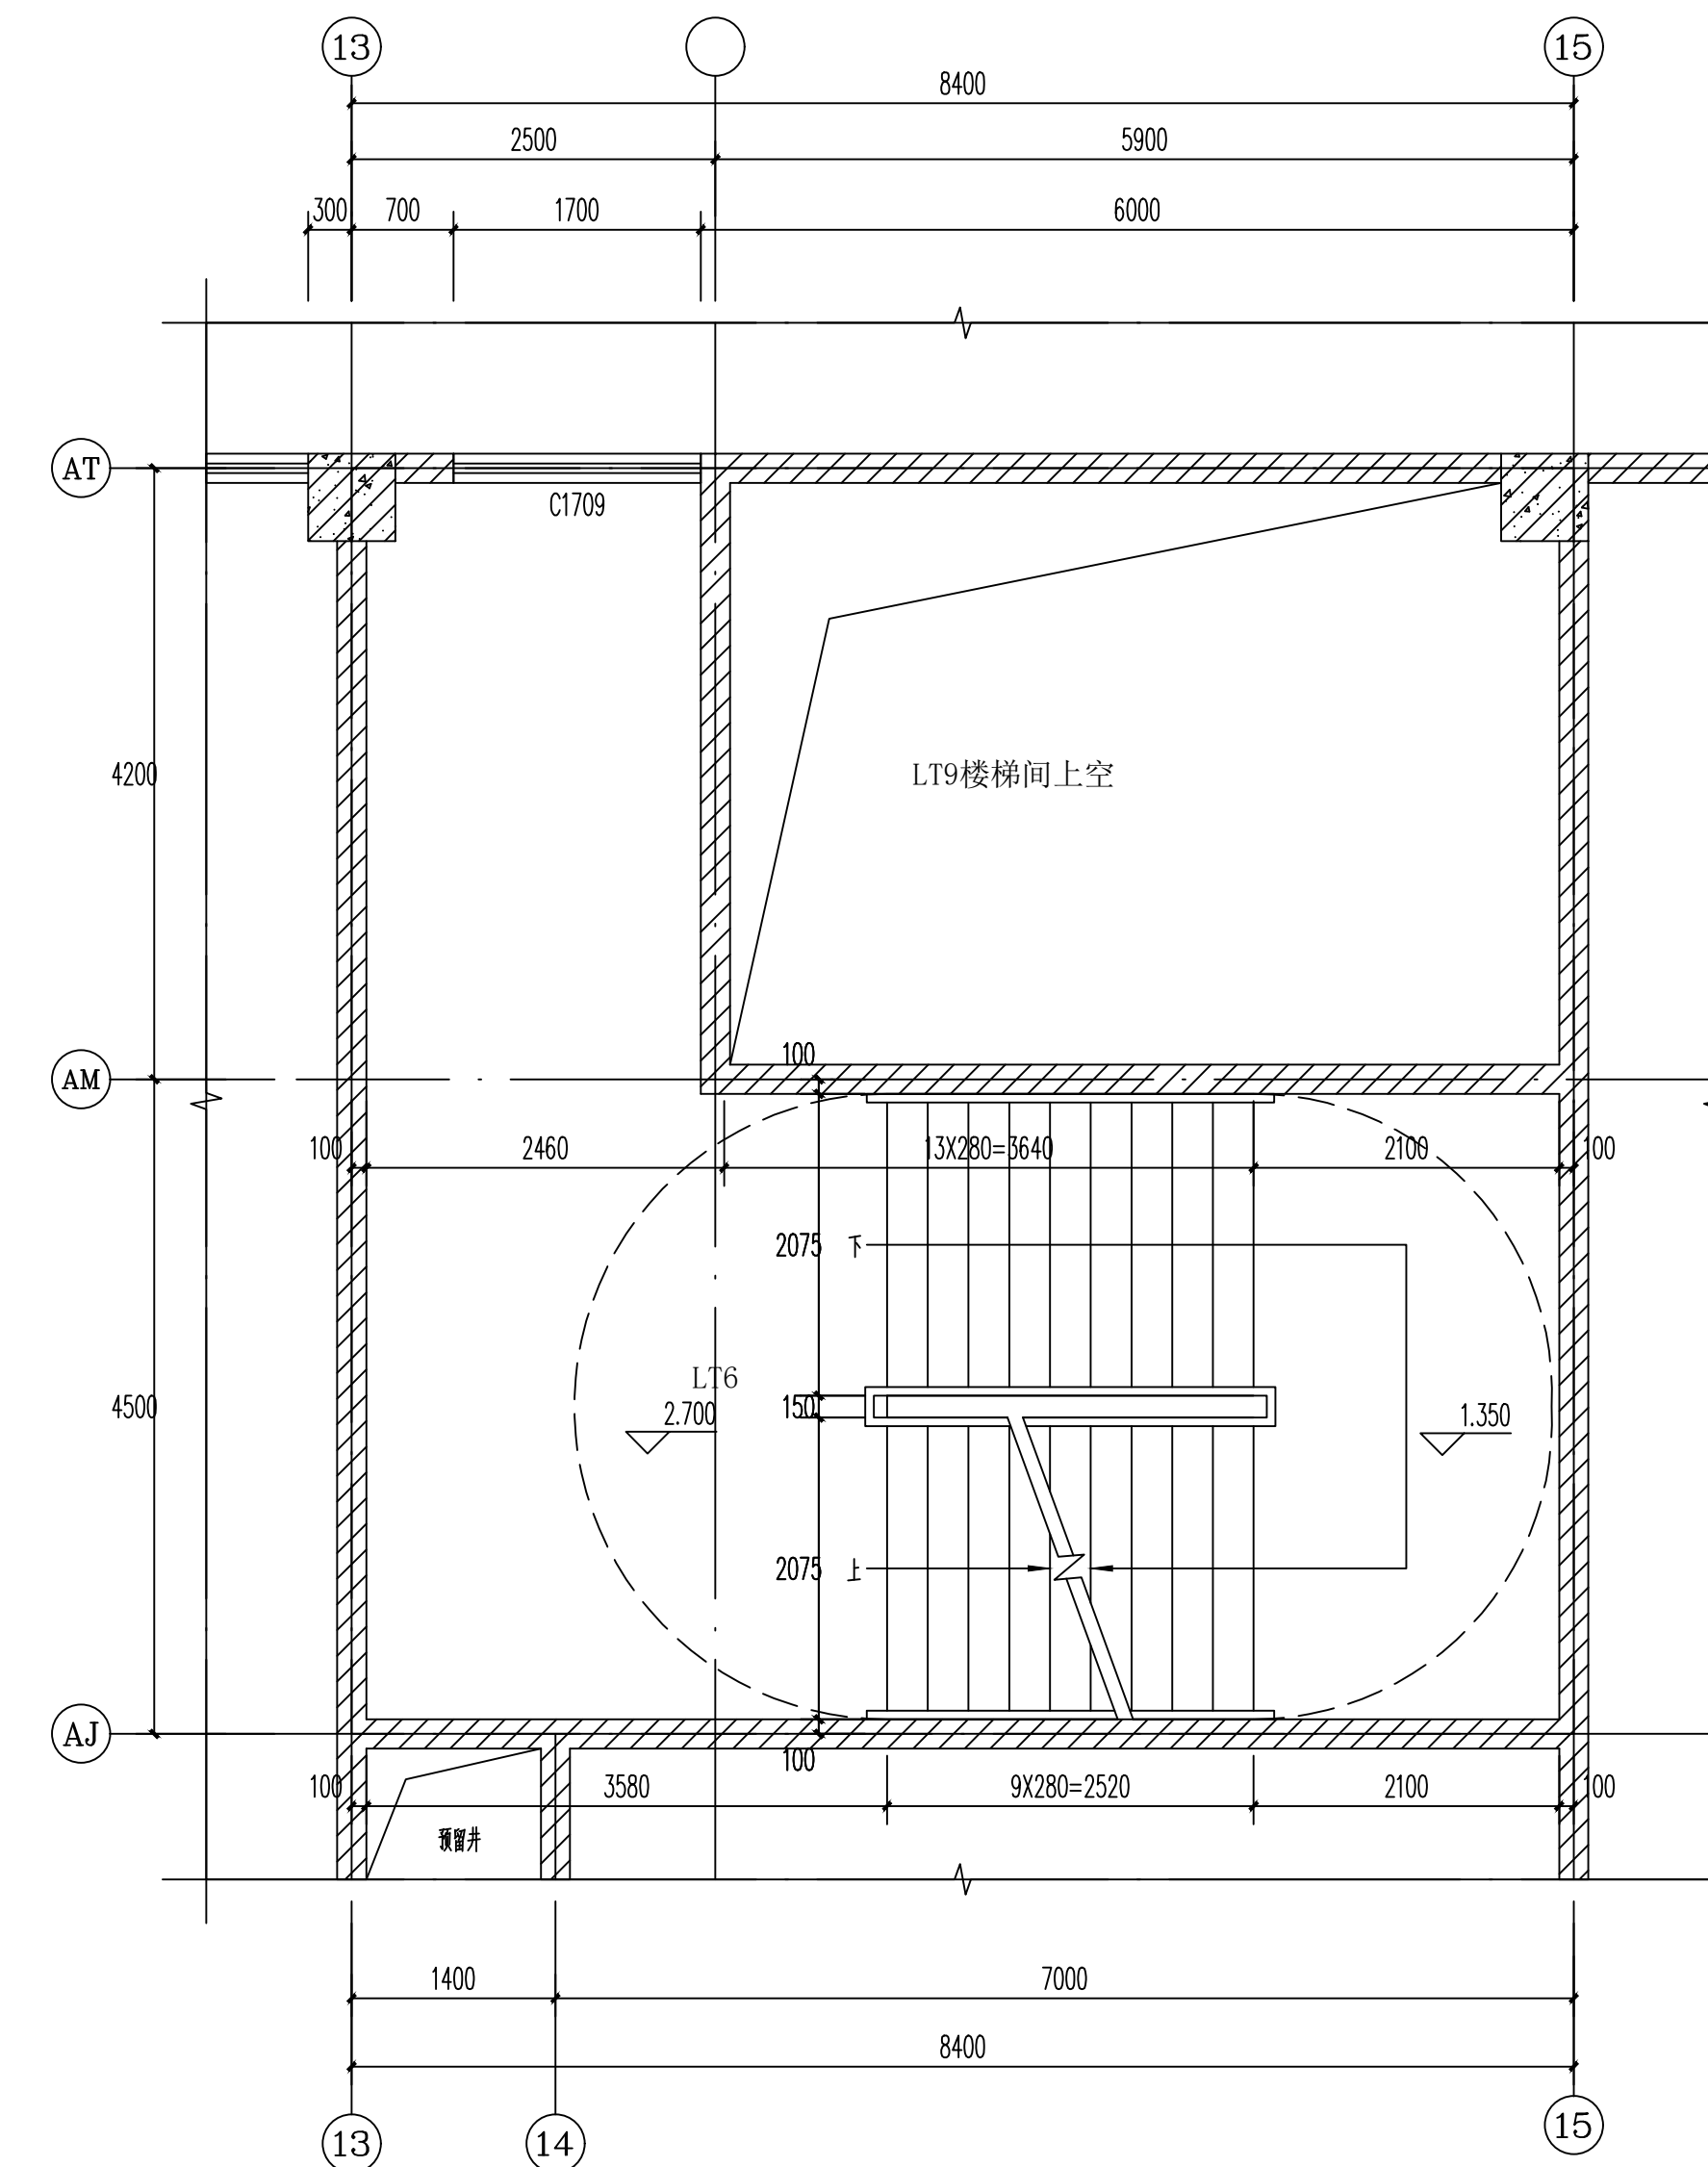
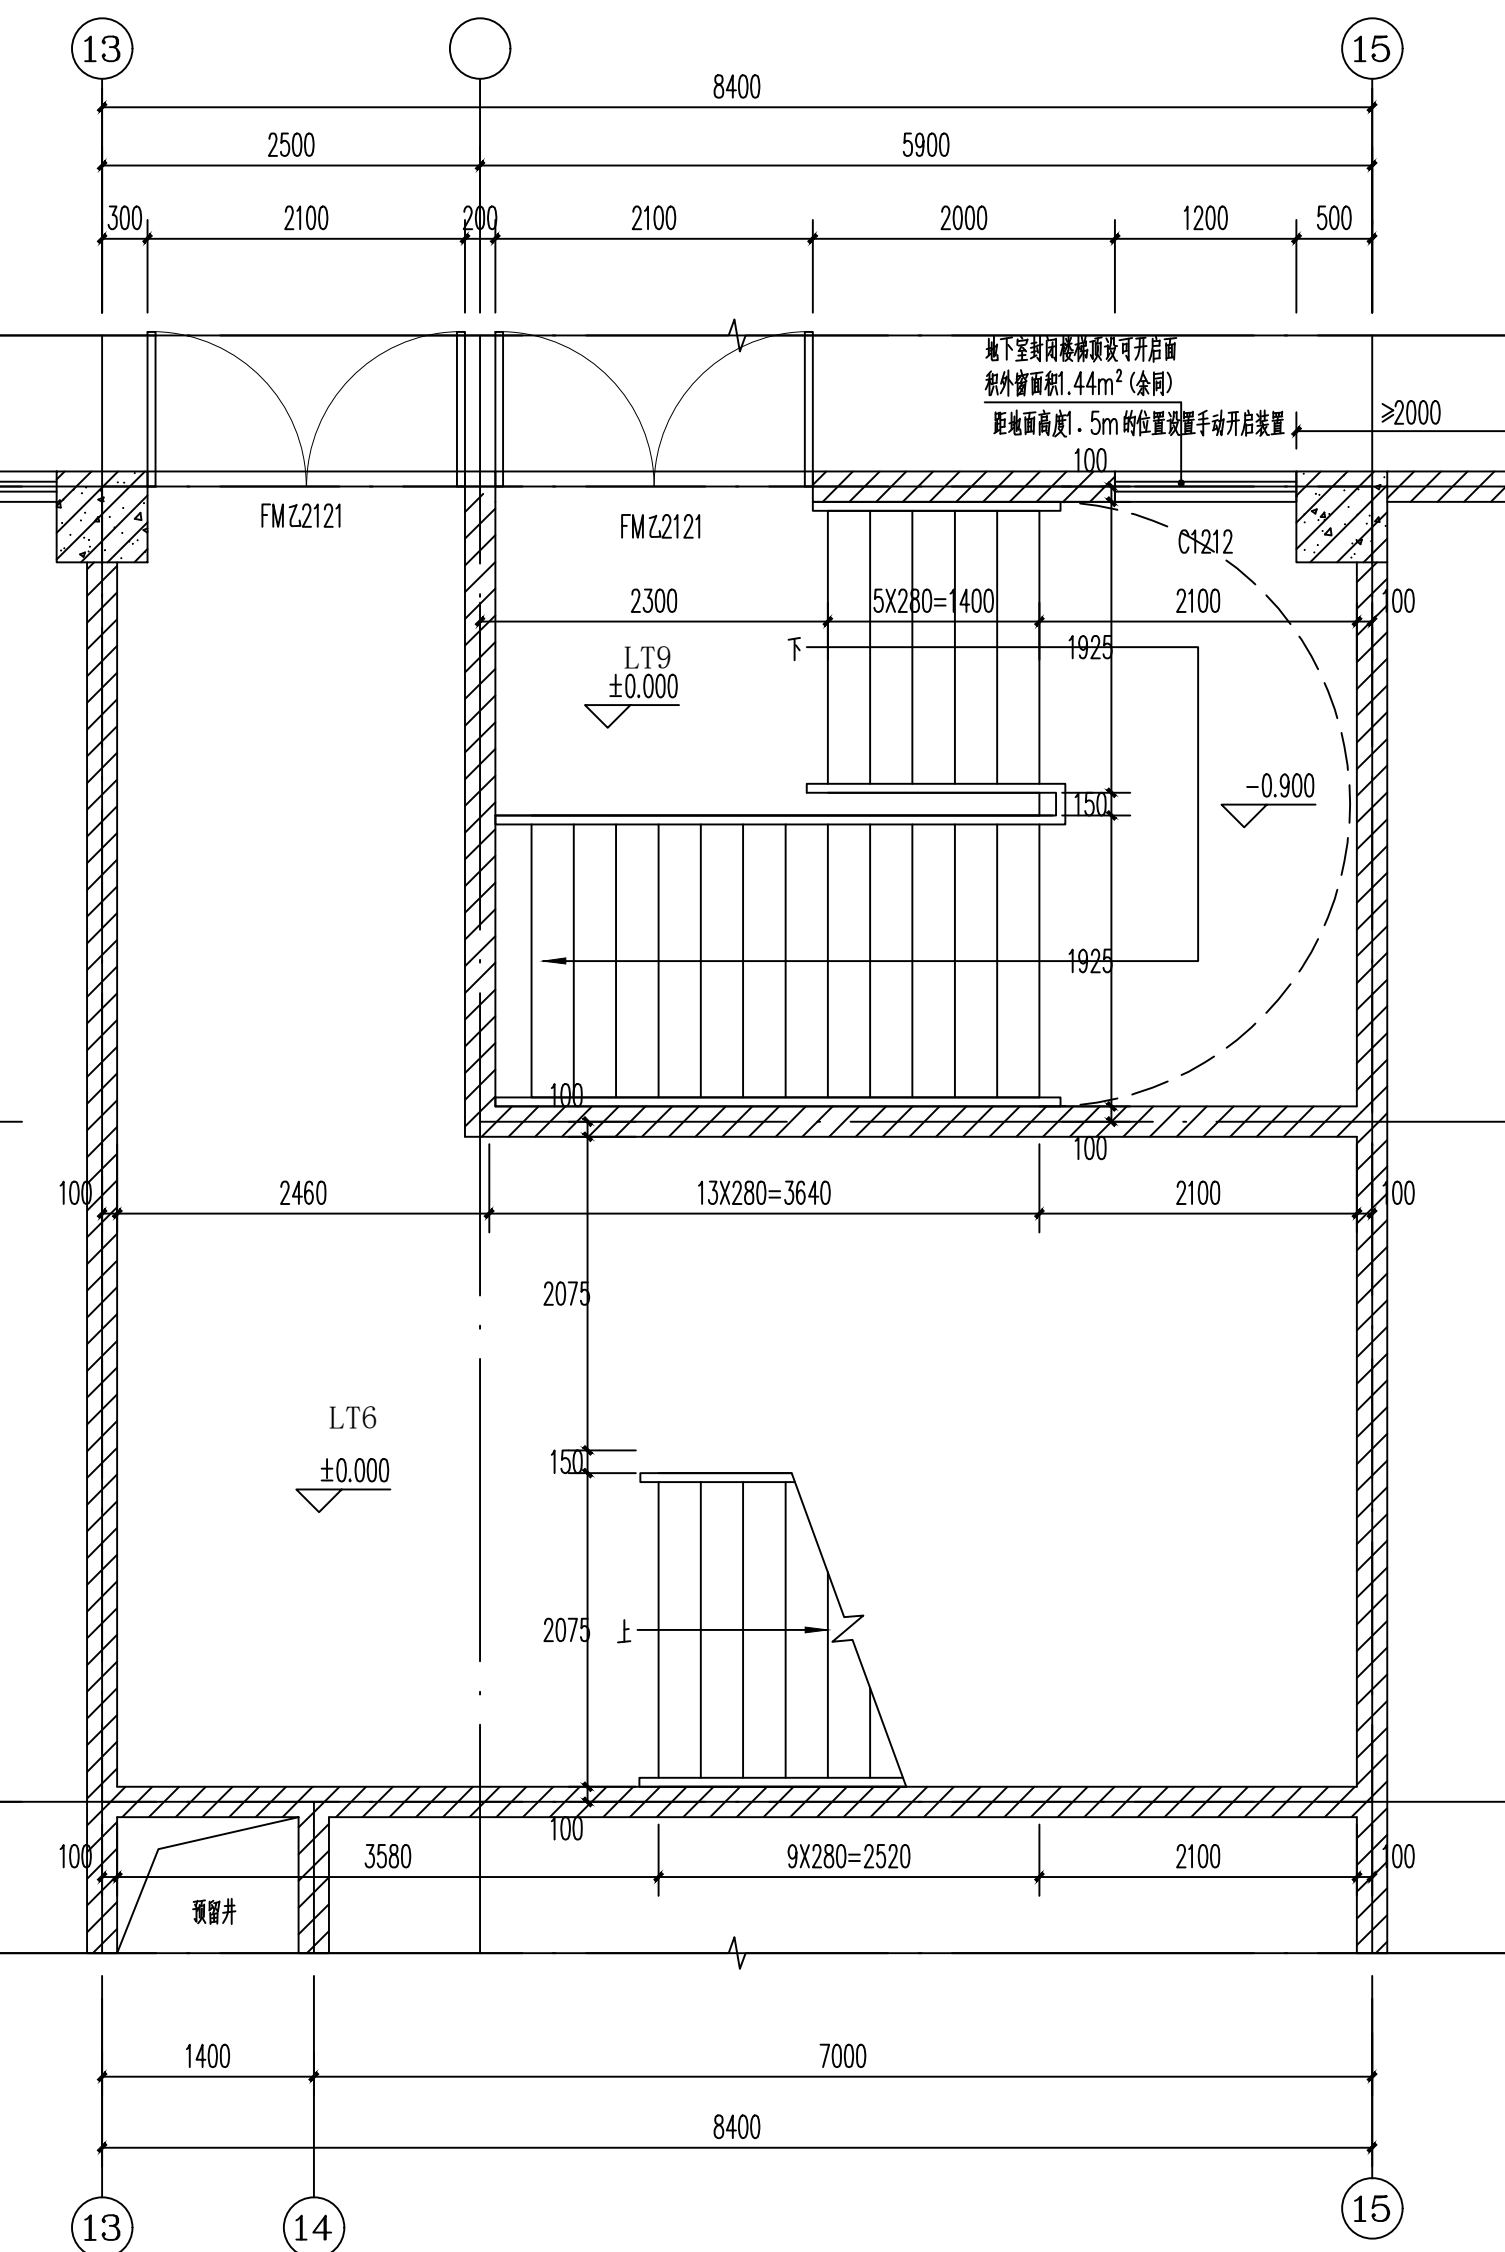
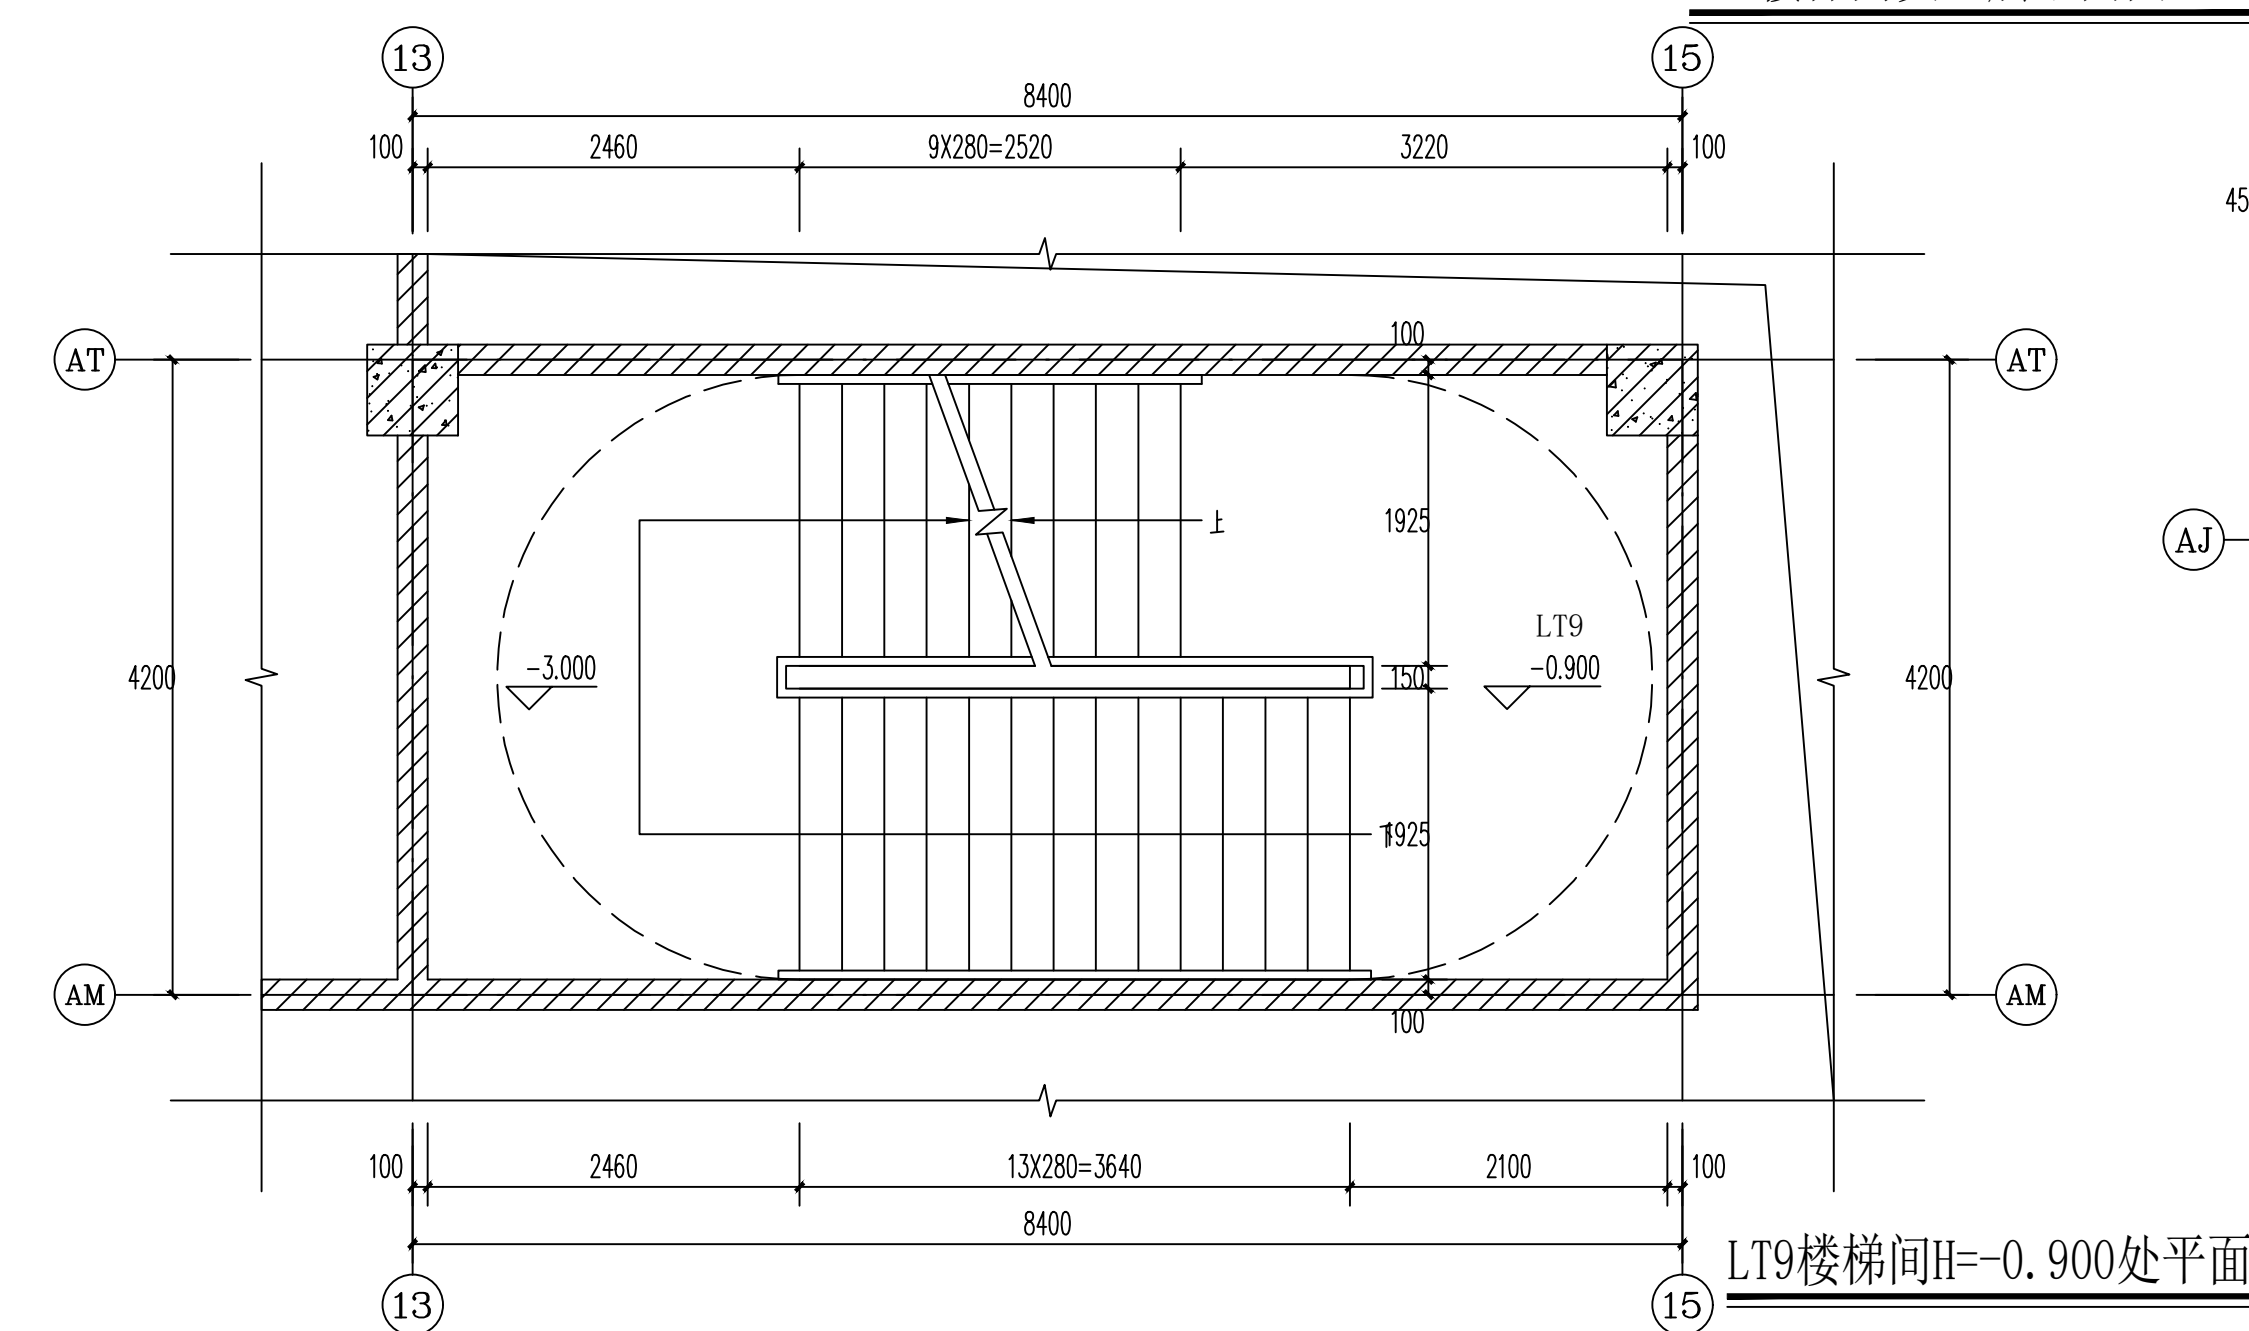


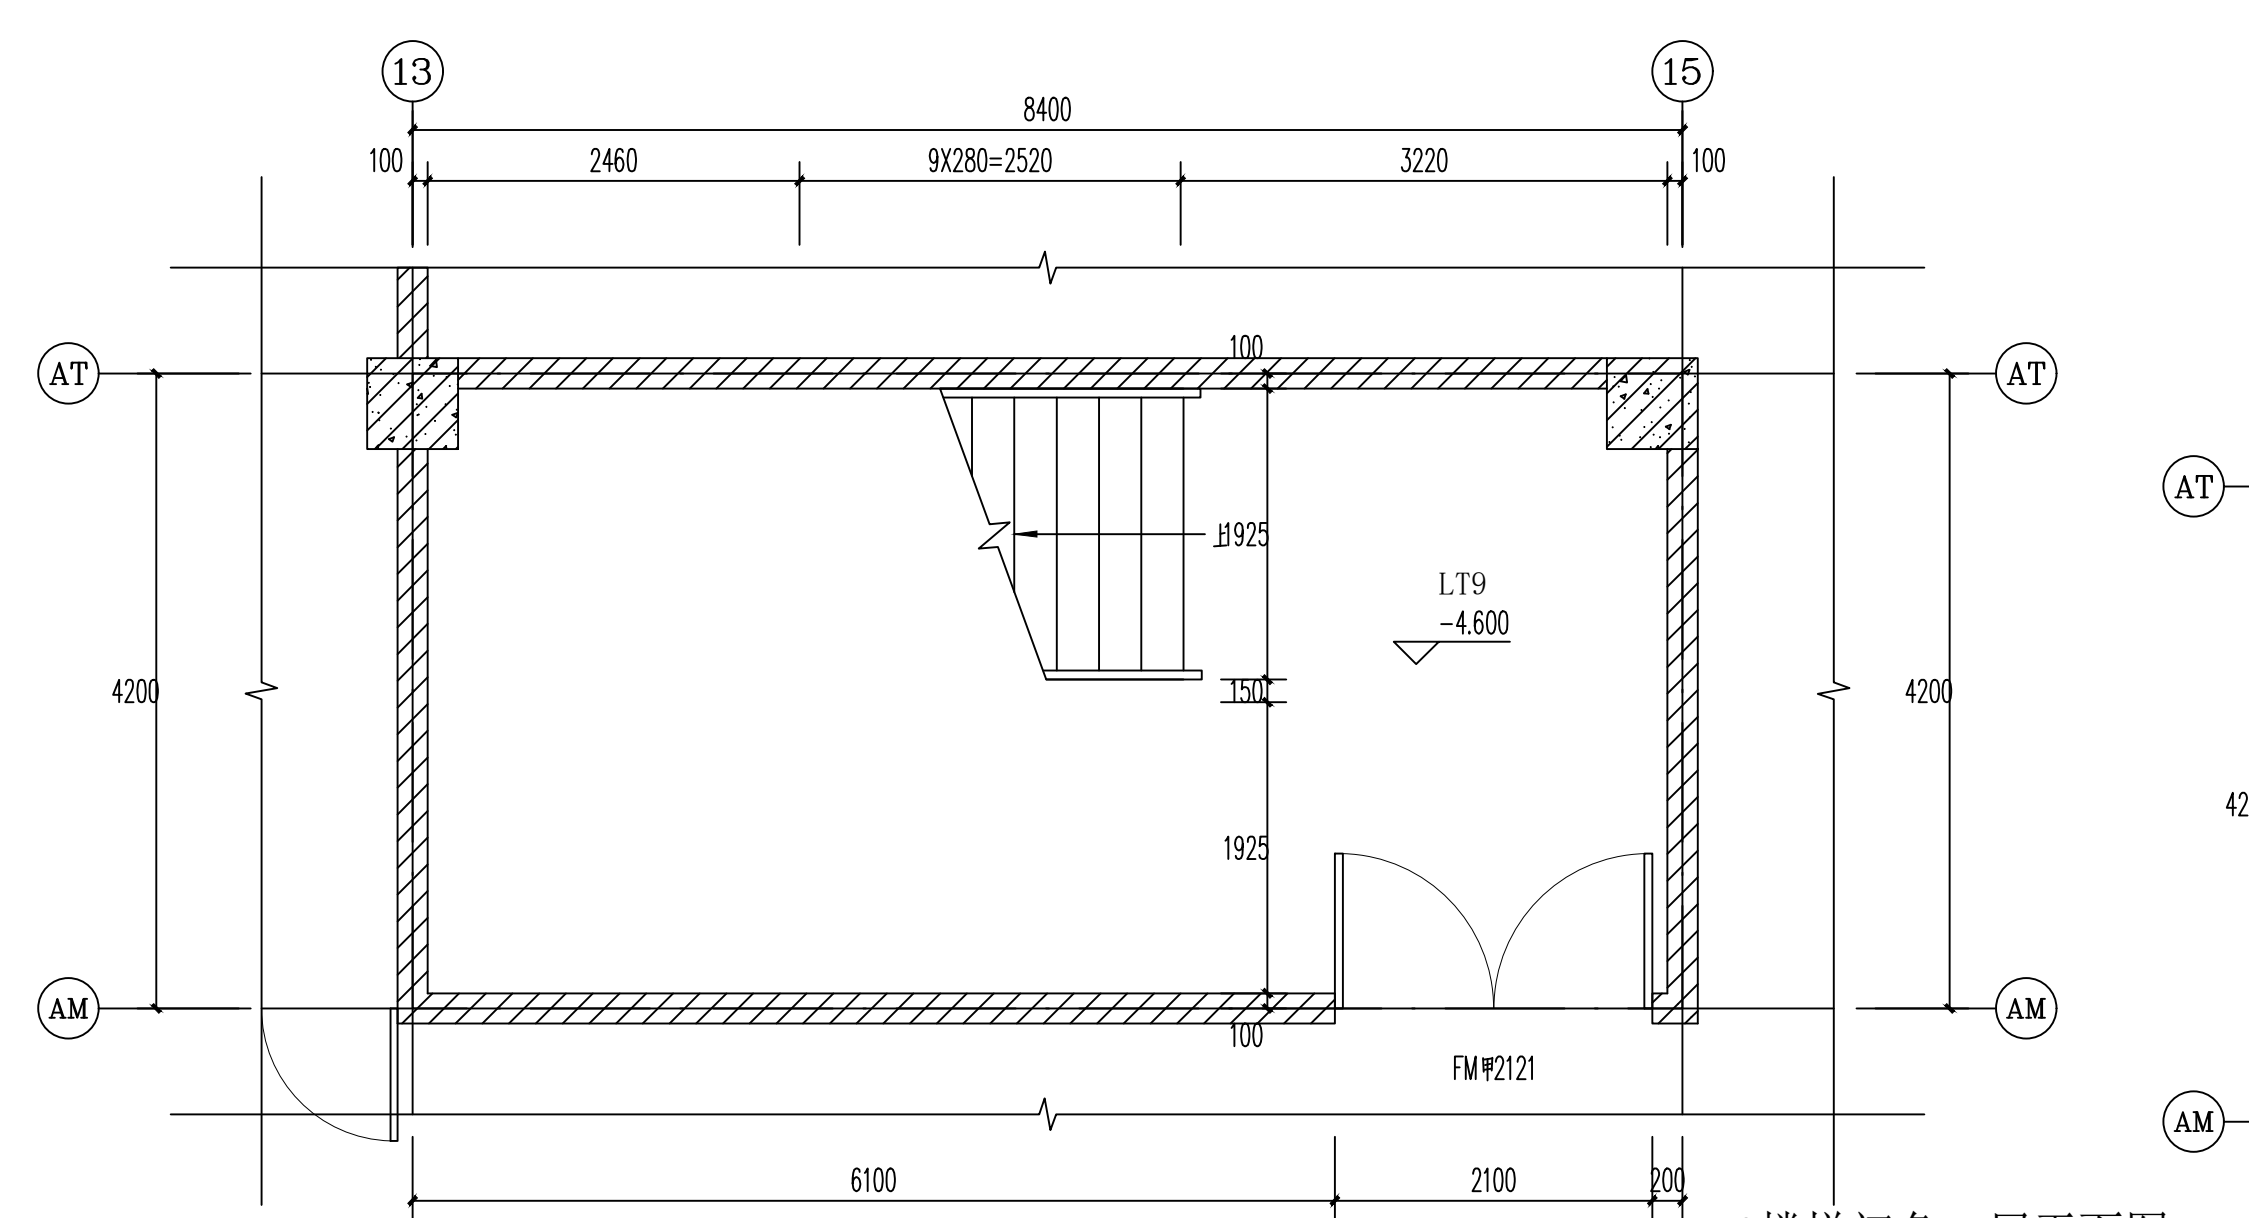

建设单位/CLIENT:

麻阳苗族自治县远桥房地产开发有限公司

项目名称/PROJECT:

远程国际

子项目名称/SUB-PROJECT:

远程国际

区位图/REGIONAL LOCATION MAP :

广东建筑艺术设计研究院有限公司
GUANGDONG ARCHITECTURAL ARTISTIC DESIGN INSTITUTE CO.,LTD

- 建筑工程设计：甲级
- 风景园林设计：乙级
- 城乡规划设计：乙级
- 市政设计：乙级

图纸名称/TITLE:

LT6、LT9楼梯间大样图

项目名称/PROJECT:

远程国际

设计	古新辉	陈永
----	-----	----

DESIGNED		

checked		
专业负责人	吕文刚	吕文刚

CHIEF	吴志刚	吴志刚

项目负责人	吴志刚	吴志刚
-------	-----	-----

PROJECT CHIEF		朱志
审核	曹国栋	曹国栋

业务号/JOB NO.

设计阶段/STATUS: 施工图

专业/DISCIPLINE: 建施

比例/	1 : 100	规格/	A1
-----	---------	-----	----

出图日期/DATE: 2021.06

图号/DRAWING NO. JS-33

版次	修改内容	日期
----	------	----

条形码/BARCODE:

版权所有，不得复制、套用。

ALL RIGHTS RESERVED, DON'T COPIED, REPRODUCED.