



③ 墙身大样三 1:25

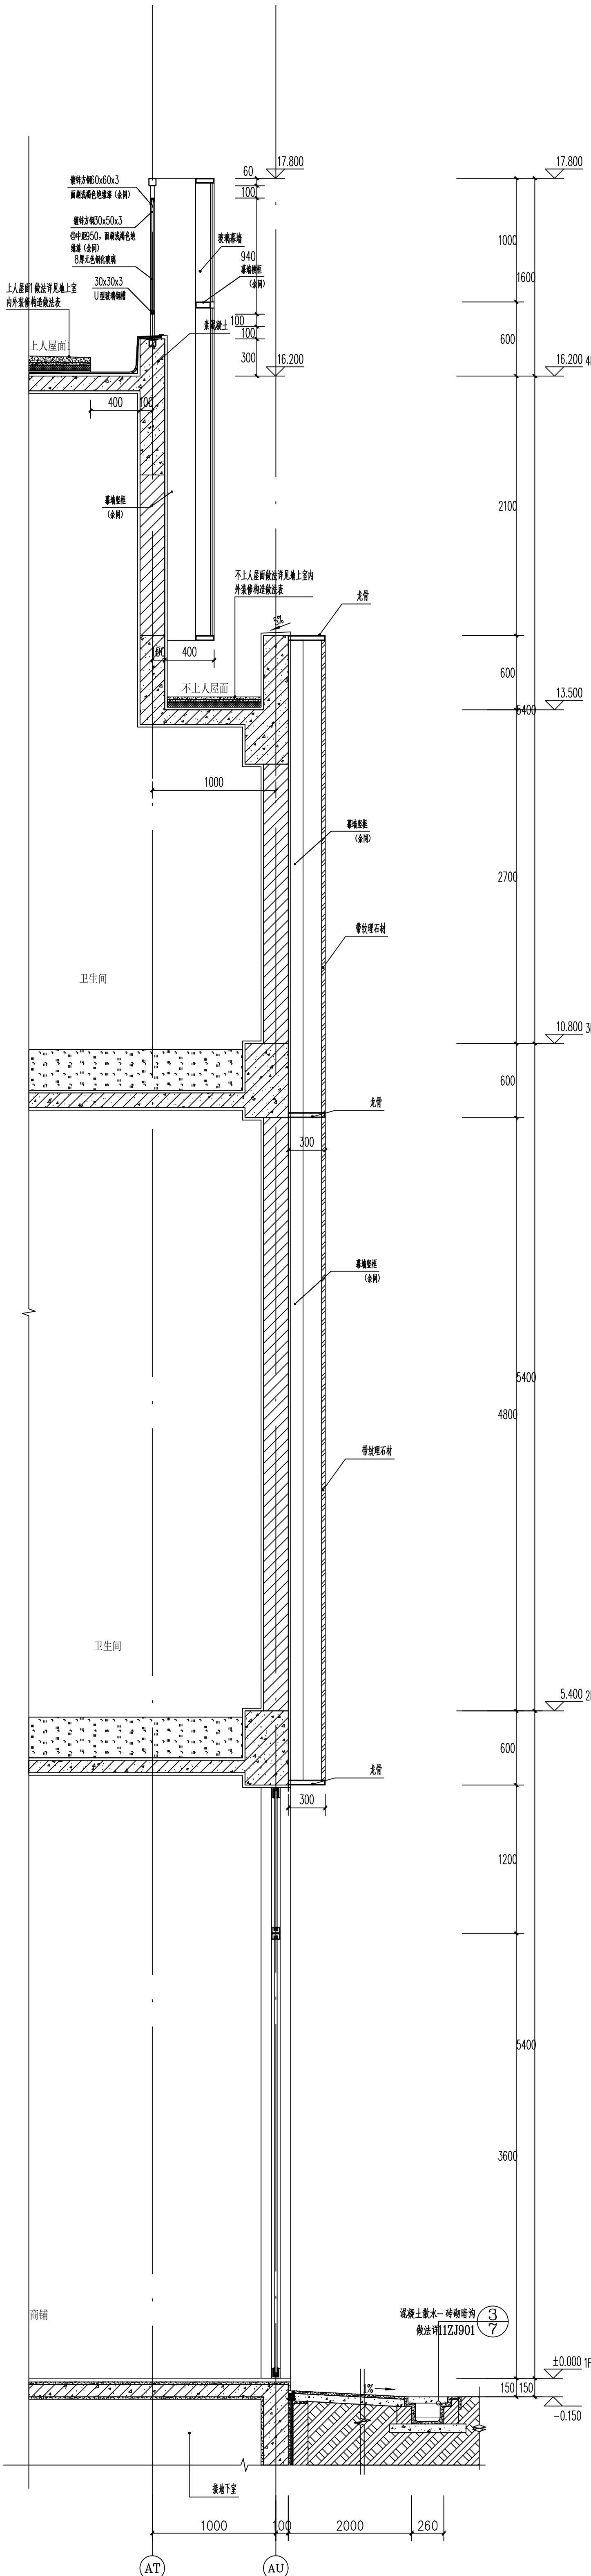

② 墙身大样二 1:25

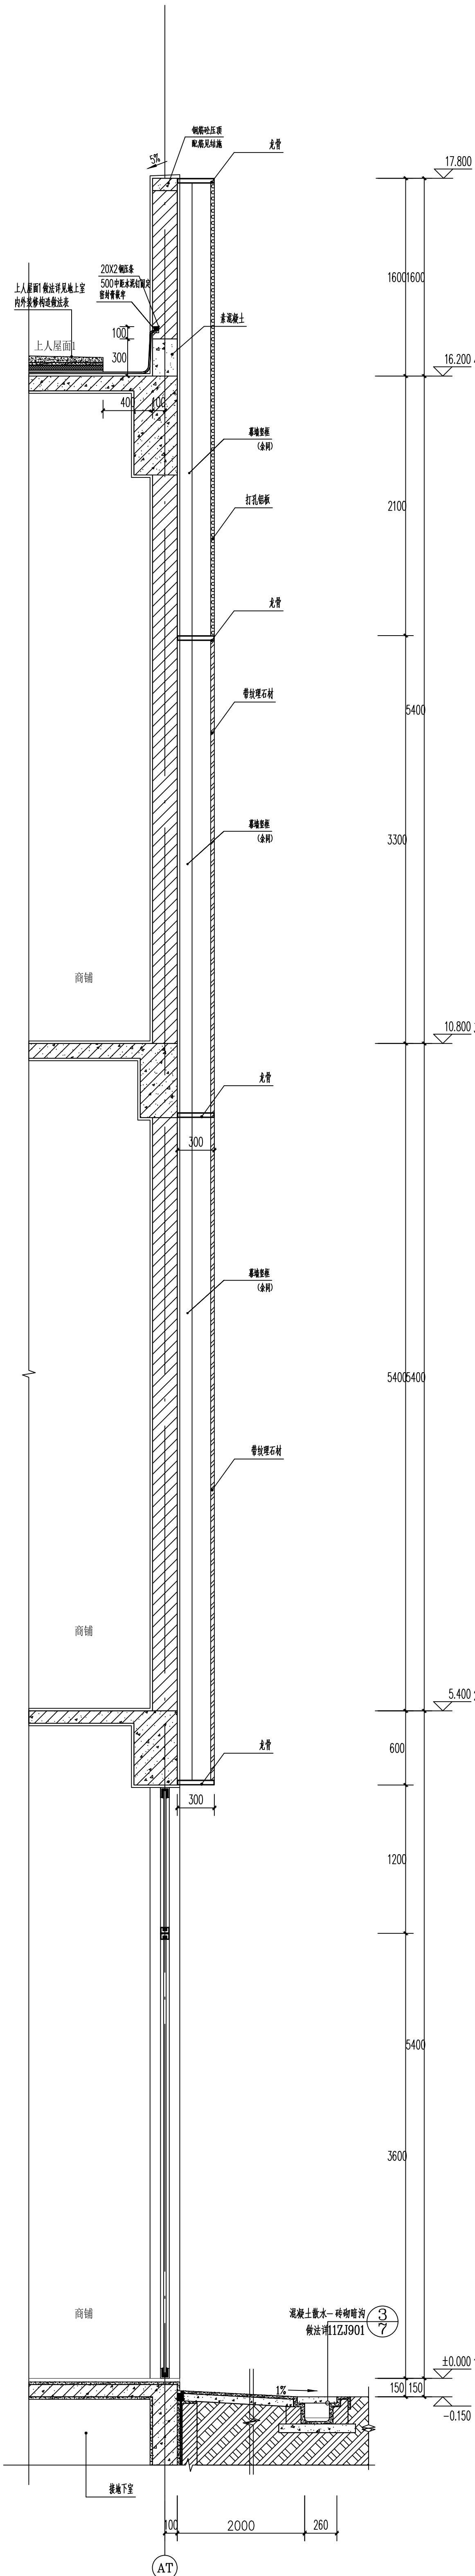

① 墙身大样一 1:25

建设单位/CLIENT:		廉阳苗族自治县远桥房地产开发有限公司	
项目名称/PROJECT:		远桥国际	
子项目名称/SUB-PROJECT:		远桥国际	
区位图/REGIONAL LOCATION MAP:			
图例/LEGEND:		■ 项目用地 ■ 道路 ■ 河流 ■ 其他	
图名/TITLE:		墙身大样图一 墙身大样图二 墙身大样图三	
项目名称/PROJECT:		远桥国际	
设计/DESIGNED:		古新辉	
校对/CHECKED:		吴新红	
专业负责人/PROFESSIONAL:		吴志刚	
项目负责人/PROJECT CHIEF:		吴志刚	
审核/REVIEWED:		黄耀光	
审定/APPROVED:		李 坚	
业务号/JOB NO.:		远桥国际	
设计阶段/STATUS:		施工图	
专业/DISCIPLINE:		建筑	
比例/SCALE:		1:100	
出图日期/DATE:		2021.06	
图号/DRAWING NO.:		JS-36	
版次/NO.:		修改内容	
日期/DATE:			
条形码/BARCODE:			
版权所有, 不得复制或再行使用。		ALL RIGHTS RESERVED. DON'T COPY OR REPRODUCE.	