




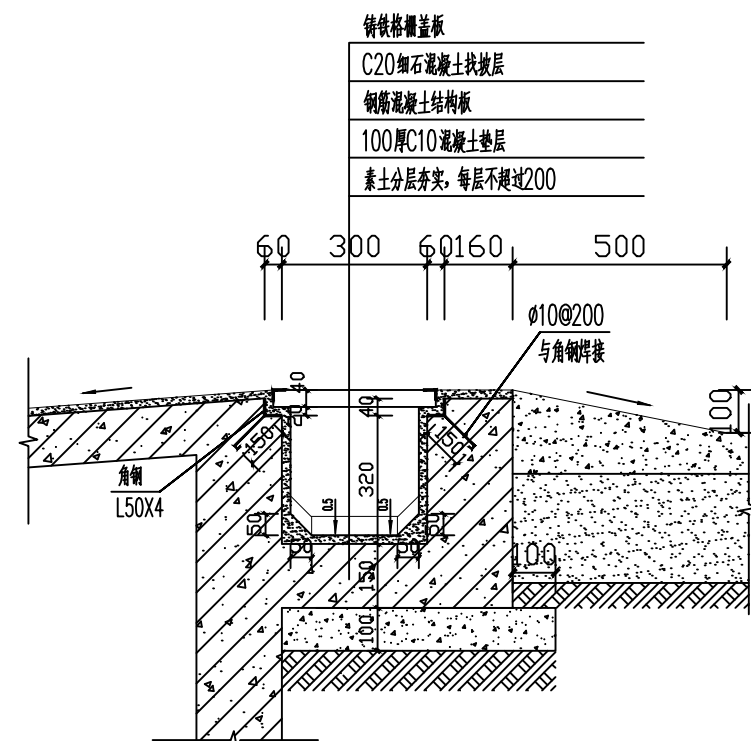


① 车道室外地面截水沟大样 1:25

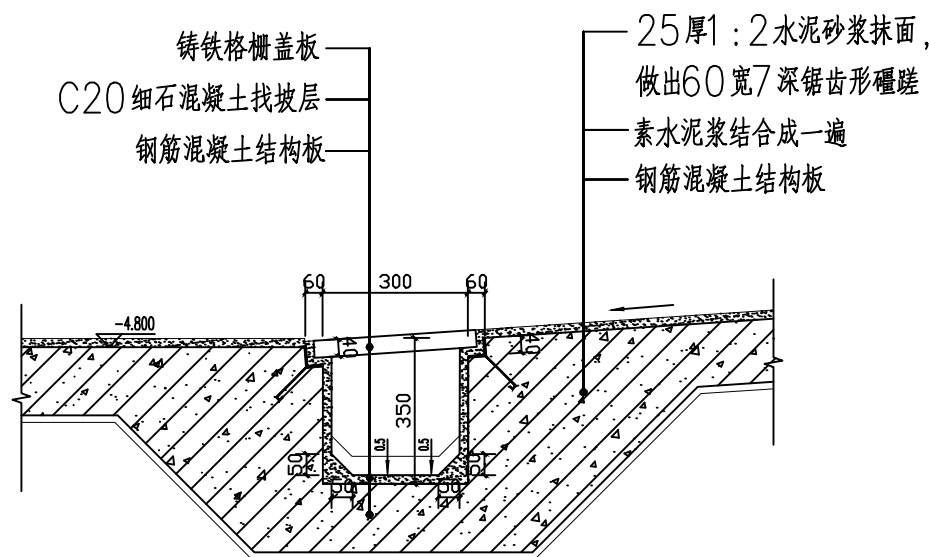


② 车道室内地面截水沟大样 1:25

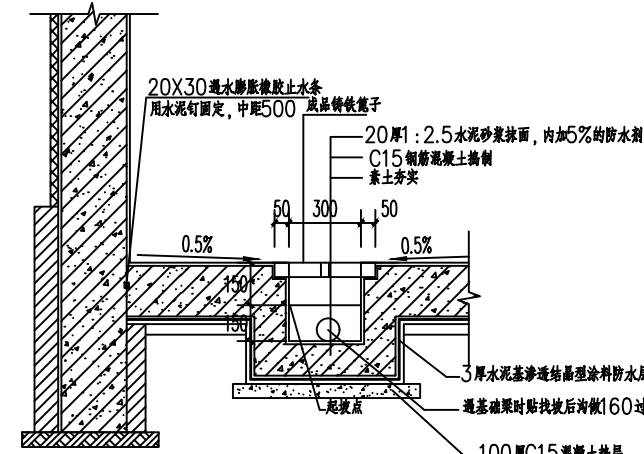


③ 300宽排水沟大样 1:25

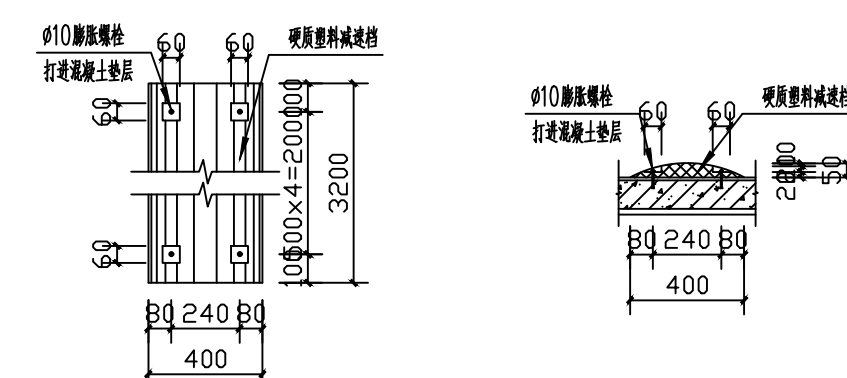


④ 塑料减速档 1:25

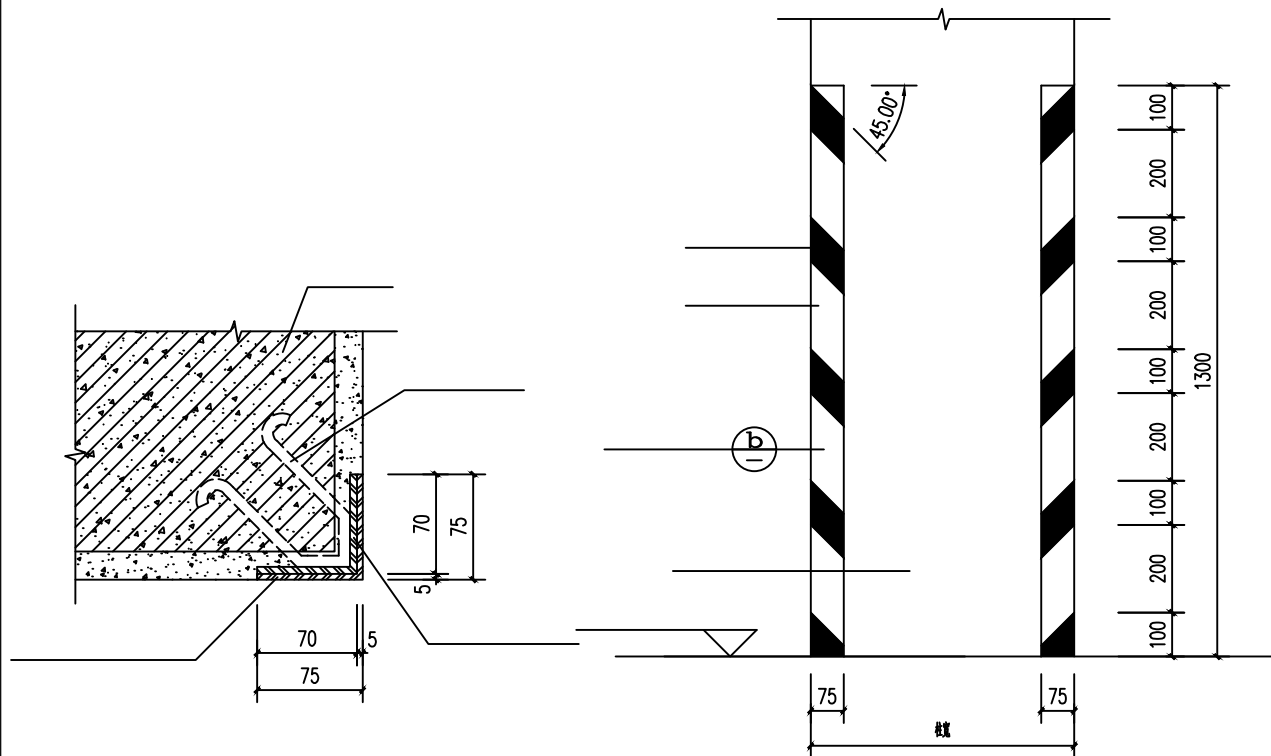

⑤ 车库墙柱防撞保护节点 1:5

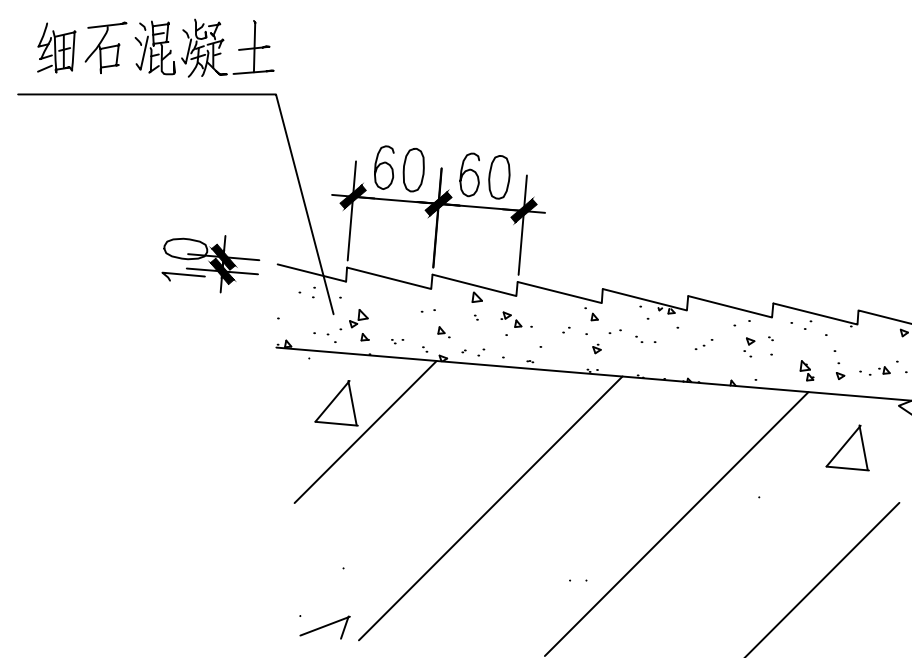


⑥ 车道防滑礅碯详图 1:5

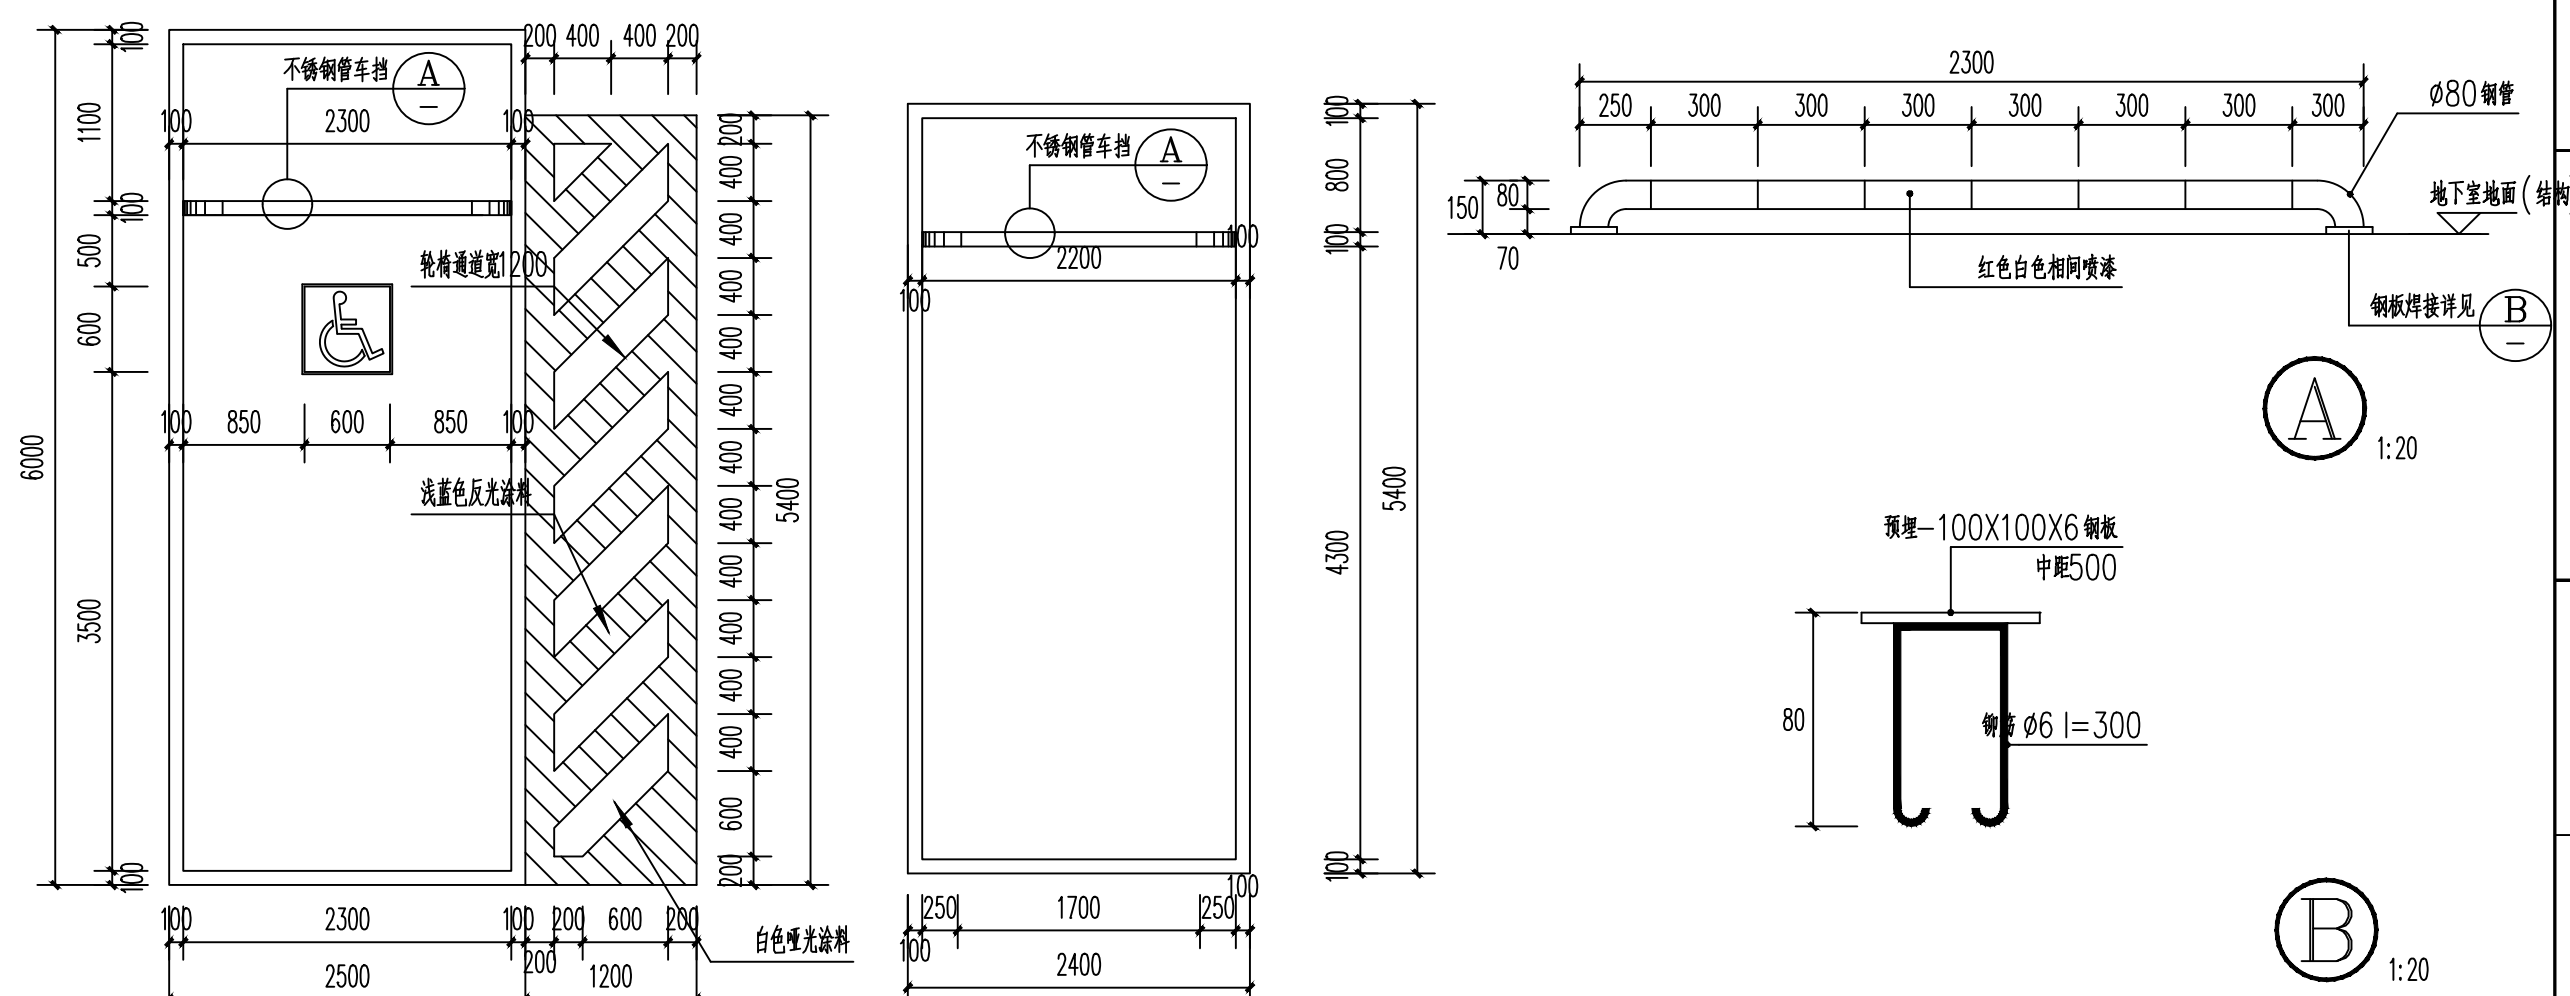


⑦ 无障碍停车位 1:50

⑧普通停车位 1:50

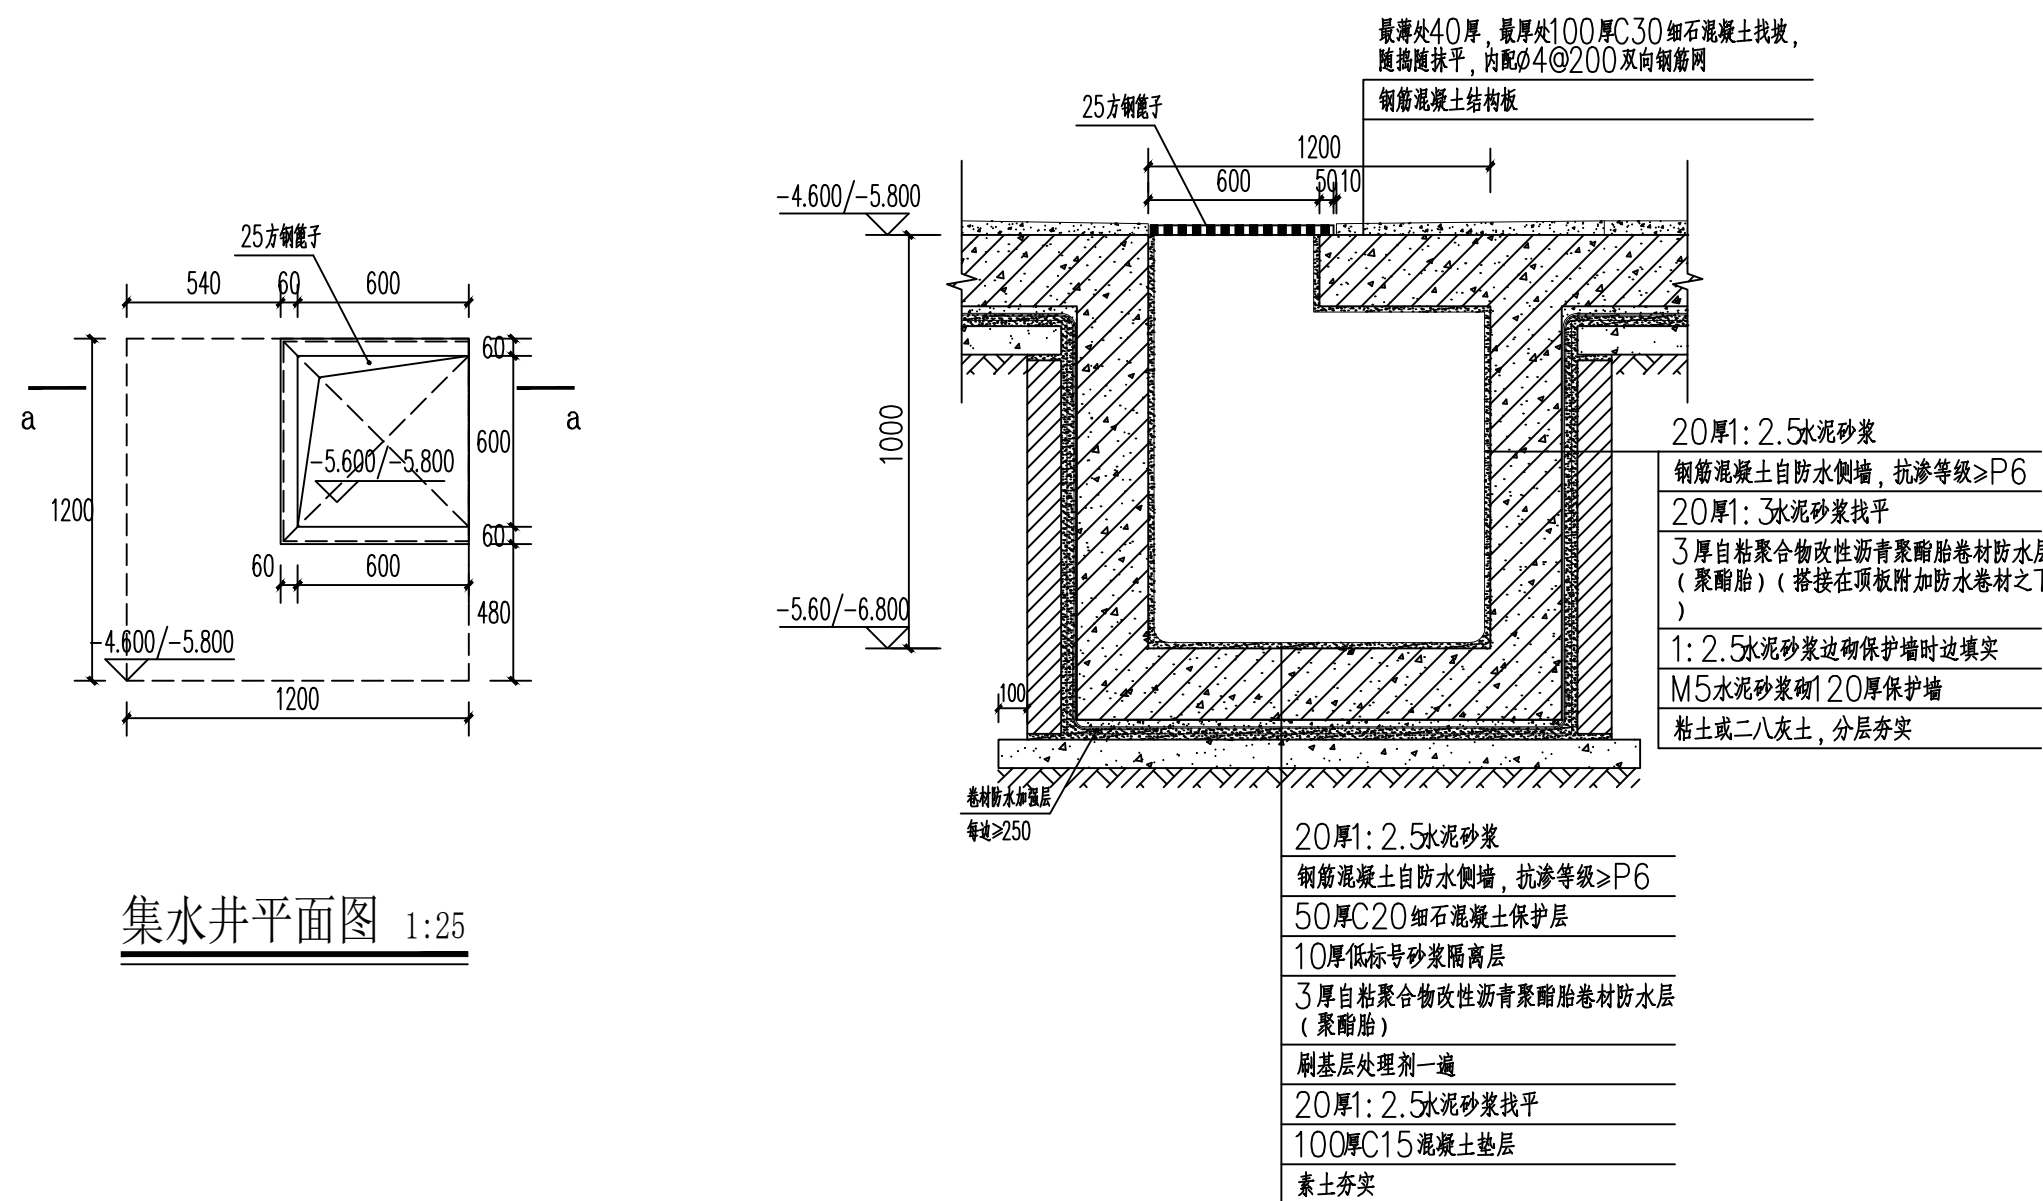

⑨ 集水井大样图 1:25

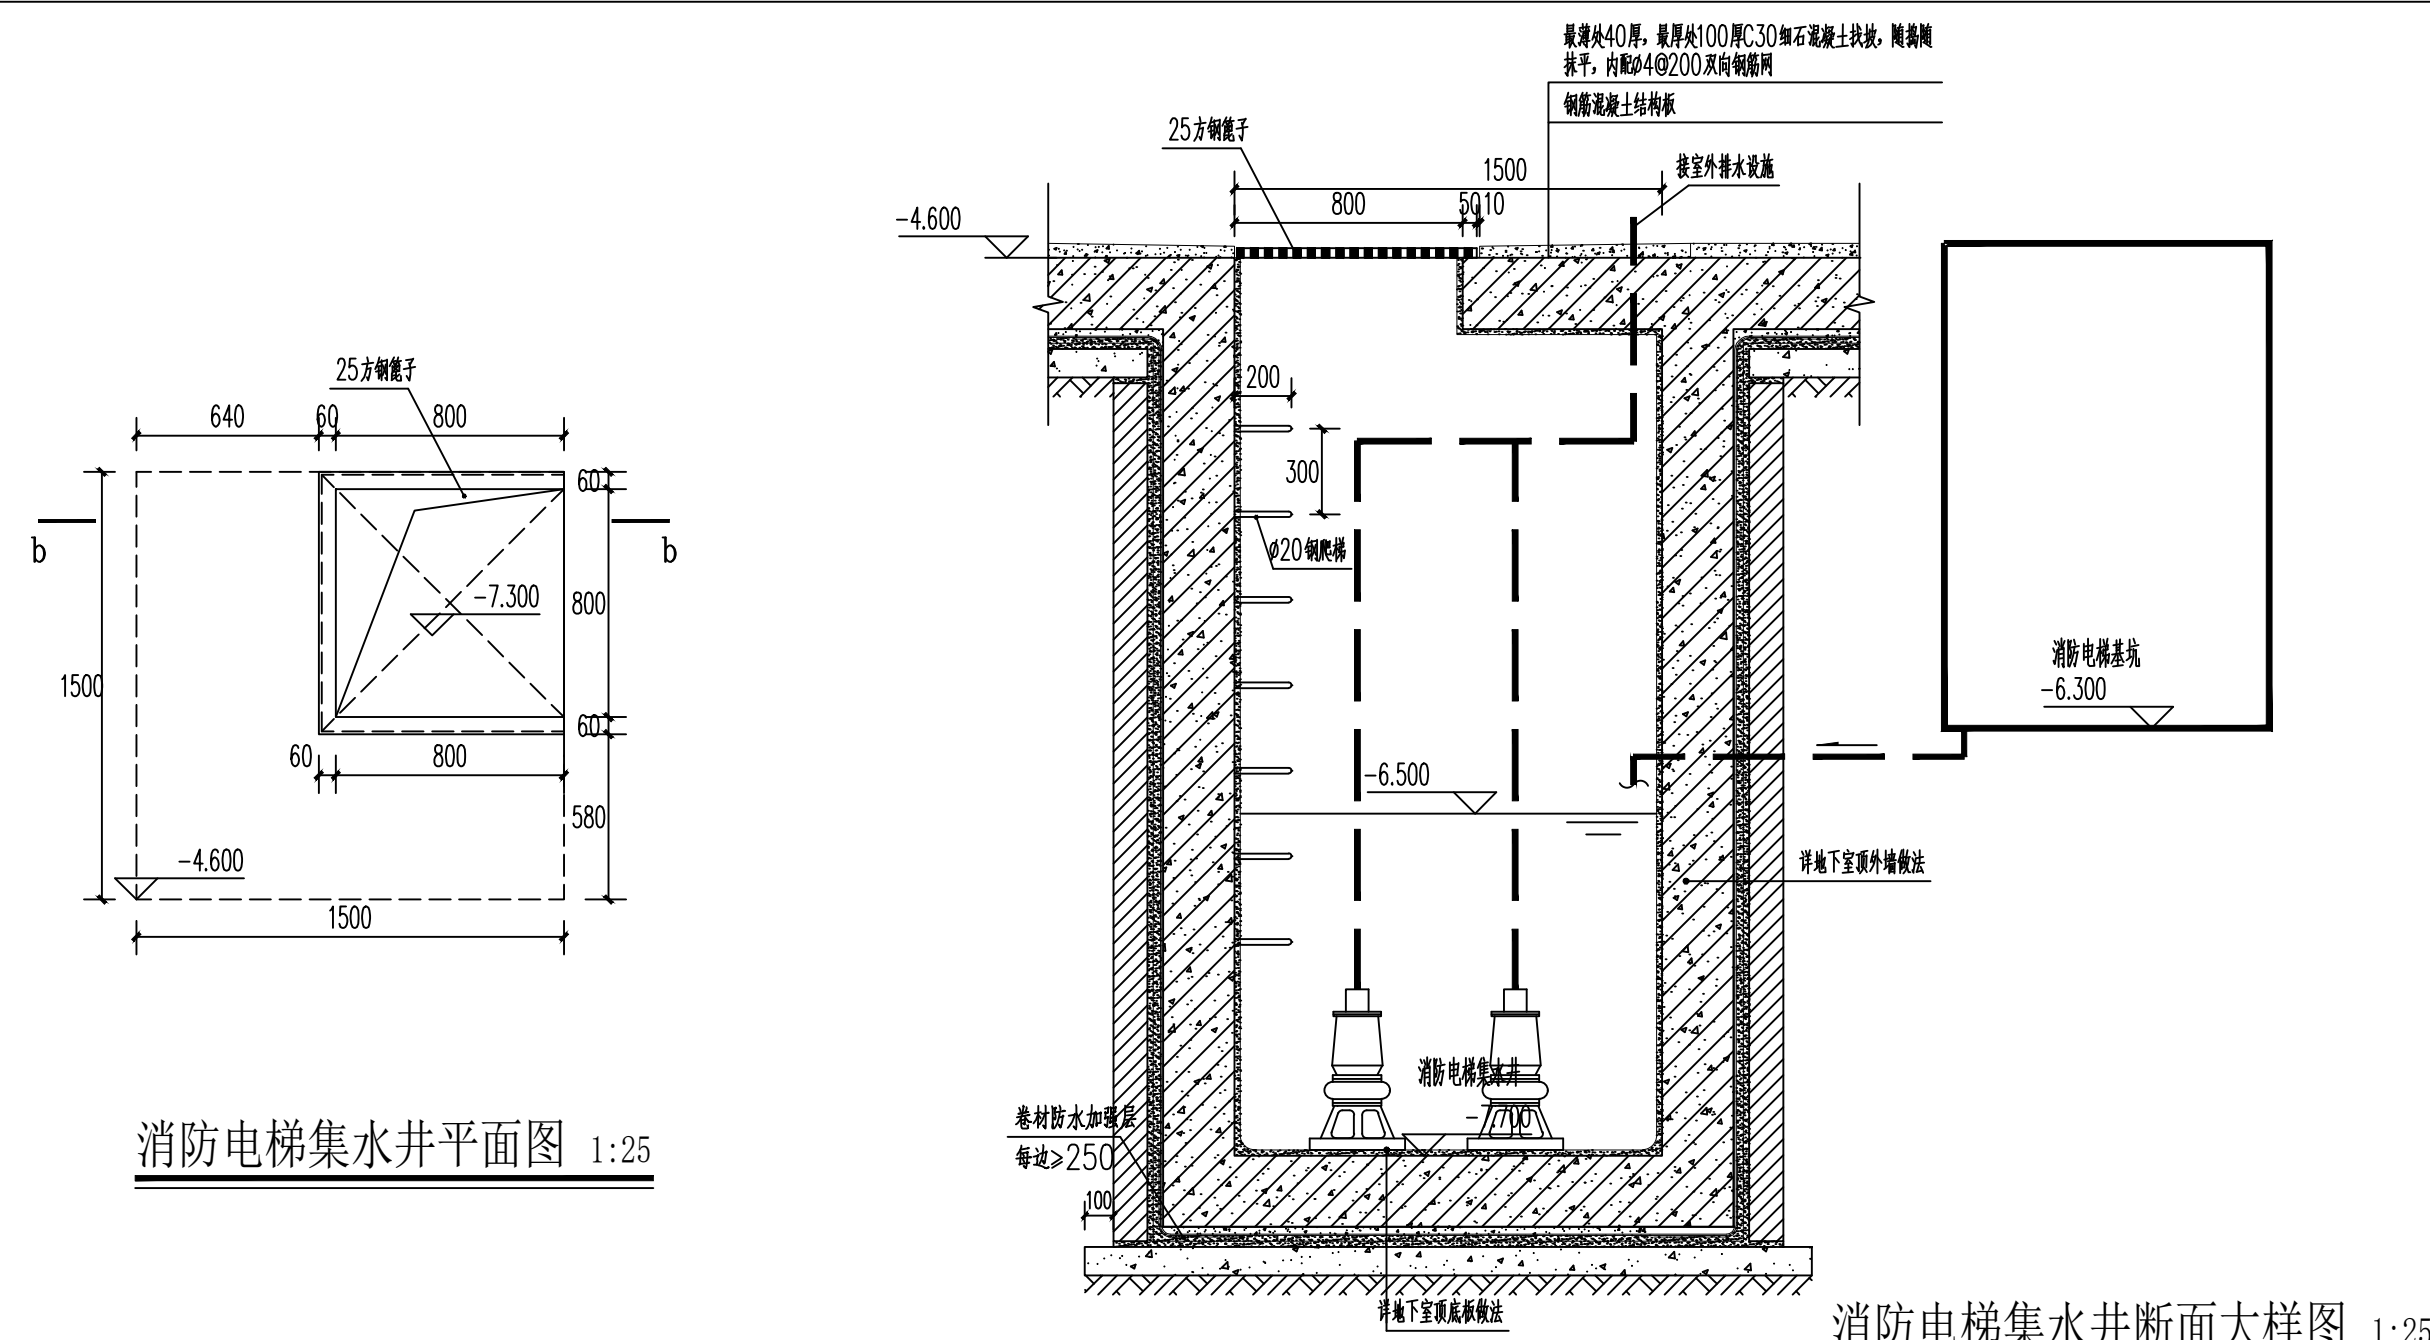

⑩消防电梯集水井大样图 1:25

建设单位/CLIENT:

麻阳苗族自治县远桥房地产开发有限公司

项目名称/PROJECT:
远程国际

子项目名称/SUB-PROJECT:	远程国际
--------------------	------

区位图/REGIONAL LOCATION MAP :

图纸名称/TITLE:

节点大样图二

项目名称/PROJECT: 远程国际

设计 DESIGNED	古新辉	
校对 CHECKED	吴新红	
专业负责人 CHIEF	吴志刚	
项目负责人 PROJECT CHIEF	吴志刚	
审核 IDENTIFIED	黄履优	
审定 APPROVED	李 坚	

业务号/JOB NO.

设计阶段/STATUS: 施工图

专业/DISCIPLINE: 建施

比例/ SCALE:	1: 100	规格/ SIZE:	A1
---------------	--------	--------------	----

出图日期/DATE: 2021.06

图号/DRAWING NO. JS-41

版次 NO.	修改内容 DESCRIPTION	日期 DATE

条形码/BARCODE:

版权所有，不得复制、套用。
ALL RIGHTS RESERVED, DON'T COPIED, REPRODUCED.