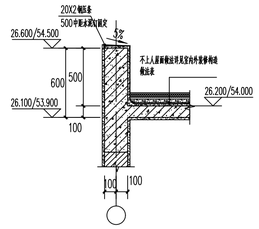

① 返边大样图 1:25

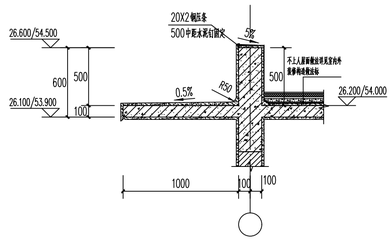

② 雨蓬大样图 1:25

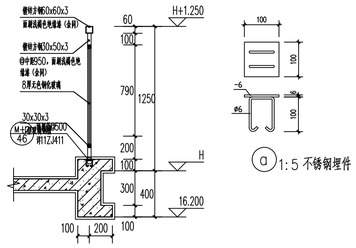

③ 阳台栏杆大样图 1:25

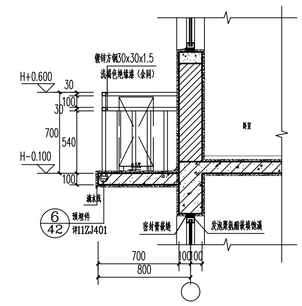

④ 空调板大样图 1:25

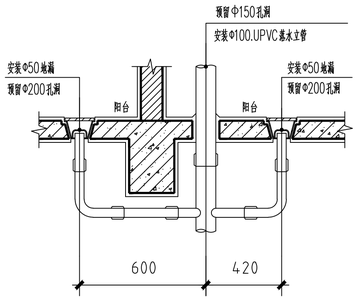

⑤ 双阳台排水大样图 1:25

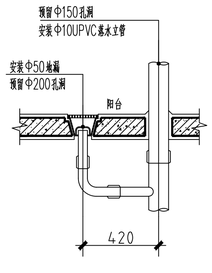

⑥ 单阳台排水大样图 1:25

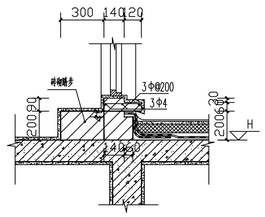

⑦ 屋顶出入口大样图 1:25

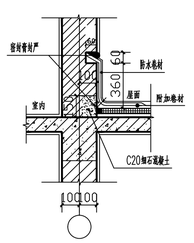

⑧ 屋面泛水大样图 1:25

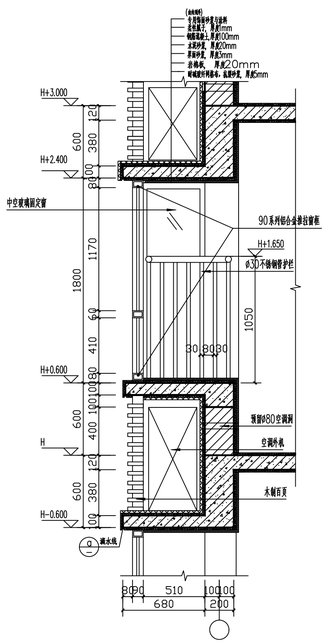

B-B剖面图 1:20

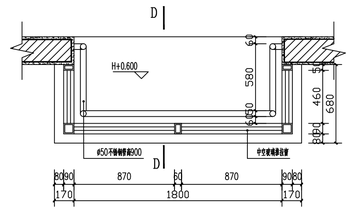

TC1平面图 1:20

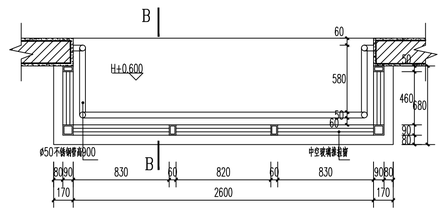

TC2平面图 1:20

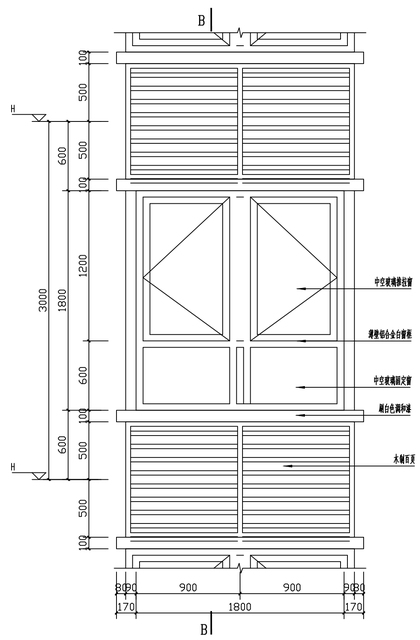

TC1立面 1:20

⑨ TC1大样图 1:20

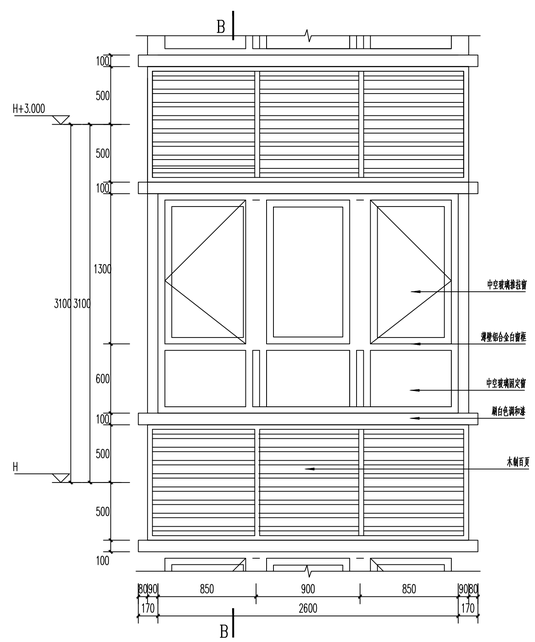

TC2立面 1:20

⑩ TC2大样图 1:20

注：所有凸窗设置百叶帘遮阳系统，详11ZJ903 1/38

建设单位/CLIENT:

麻阳苗族自治县远桥房地产开发有限公司

项目名称/PROJECT:

远程国际

子项目名称/SUB-PROJECT:

远程国际

区位图/REGIONAL LOCATION MAP :

广东建筑艺术设计院有限公司
GUANGDONG ARCHITECTURAL ARTISTIC DESIGN INSTITUTE CO.,LTD
■ 建筑工程设计：甲级 ■ 风景园林设计：乙级
■ 城乡规划设计：乙级 ■ 市政设计：乙级

图纸名称/TITLE:

节点大样图三

项目名称/PROJECT:

远程国际

设计 DESIGNED	古新辉	
校对 CHECKED	吴新红	
专业负责人 CHIEF	吴志刚	
项目负责人 PROJECT CHIEF	吴志刚	
审核 IDENTIFIED	黄履优	
审定 APPROVED	李 坚	

业务号/JOB NO.

设计阶段/STATUS: 施工图

专业/DISCIPLINE: 建施

比例/SCALE:	1：100	规格/SIZE:	A1

出图日期/DATE: 2021.06

图号/DRAWING NO. JS-42

版次 NO.	修改内容 DESCRIPTION	日期 DATE

条形码/BARCODE:

版权所有，不得复制、套用。
ALL RIGHTS RESERVED,DON'T COPIED,REPRODUCED.