
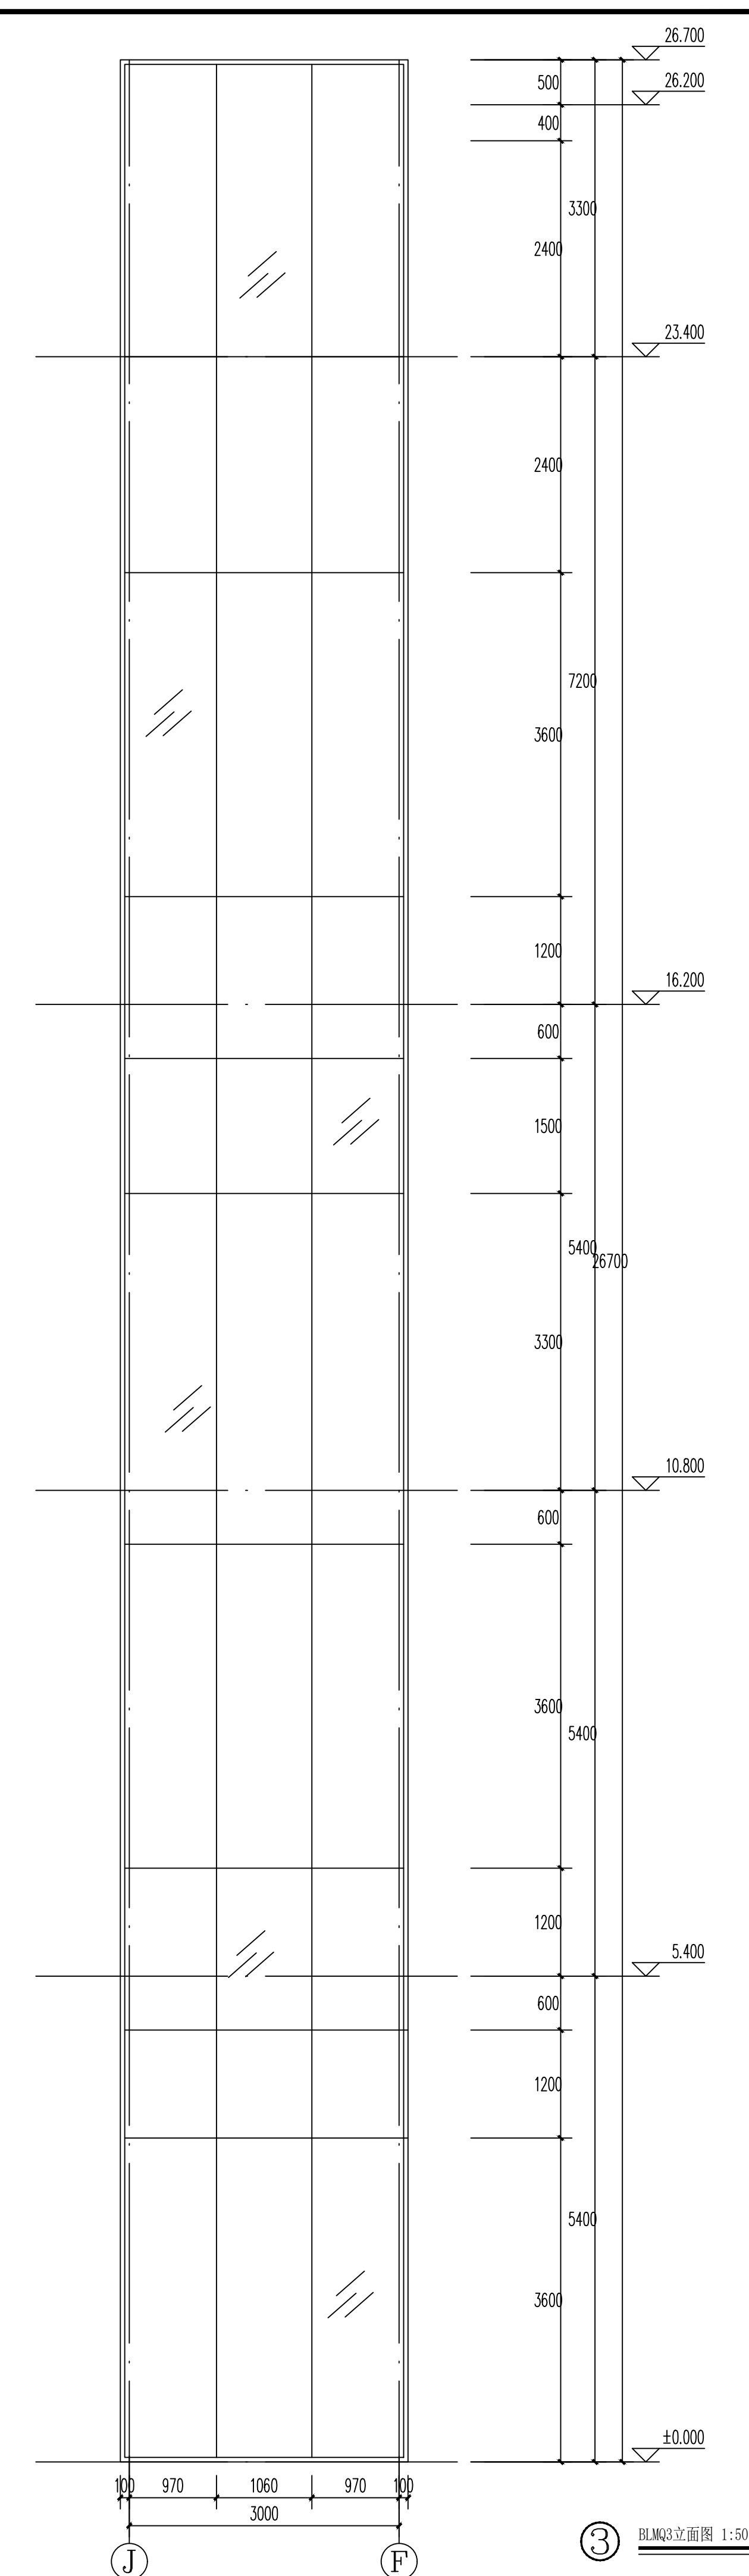
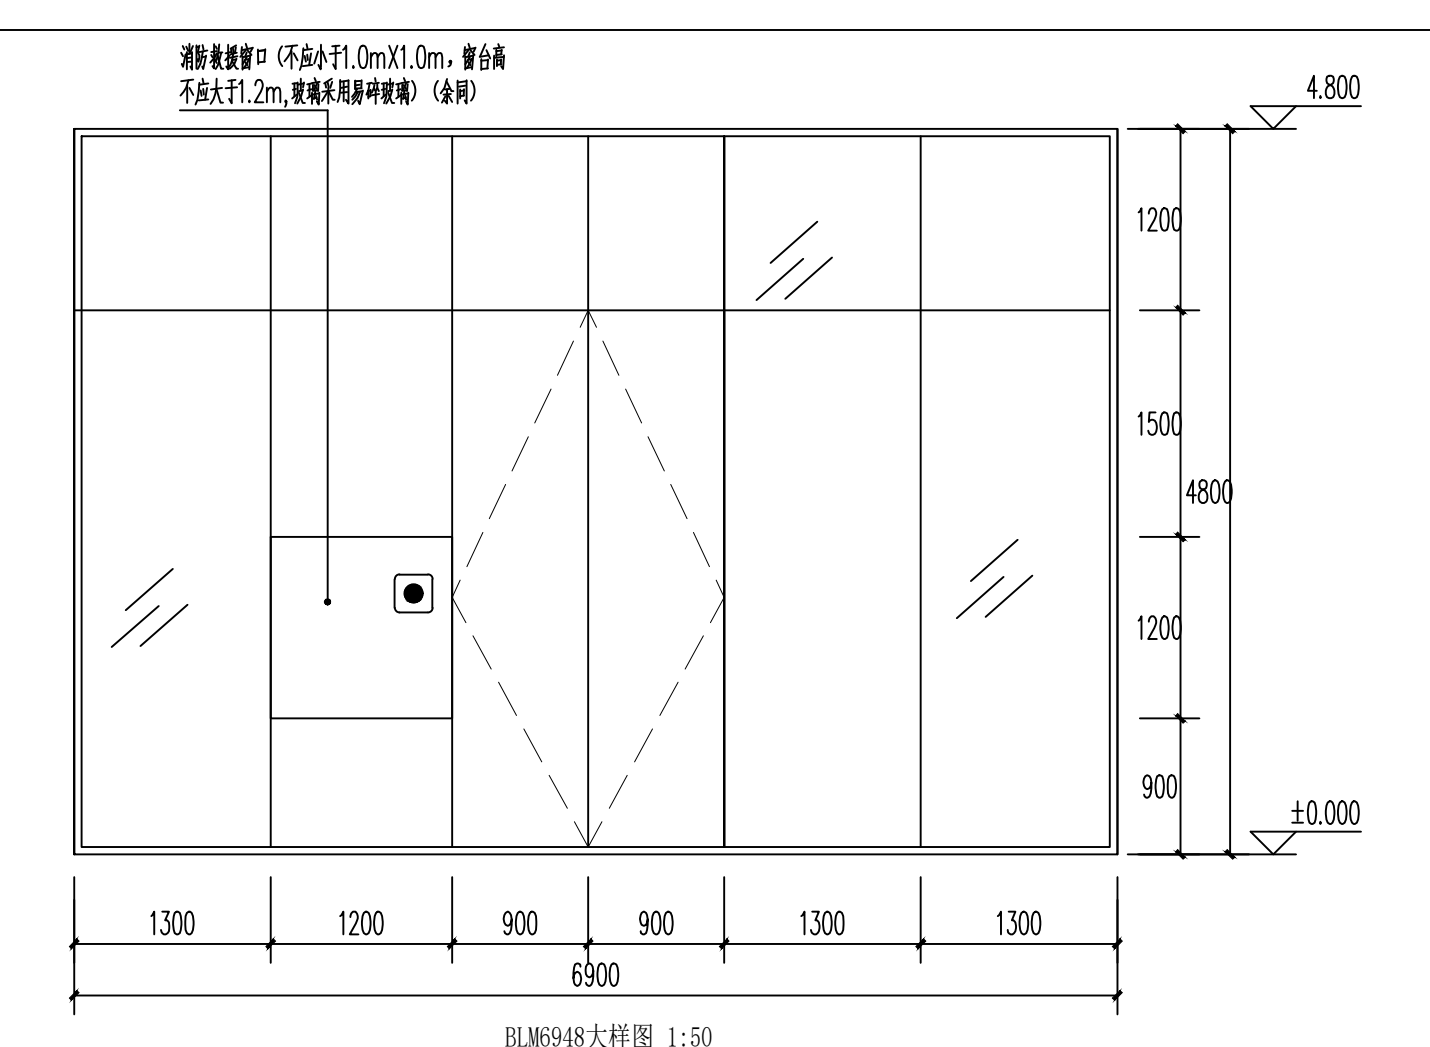
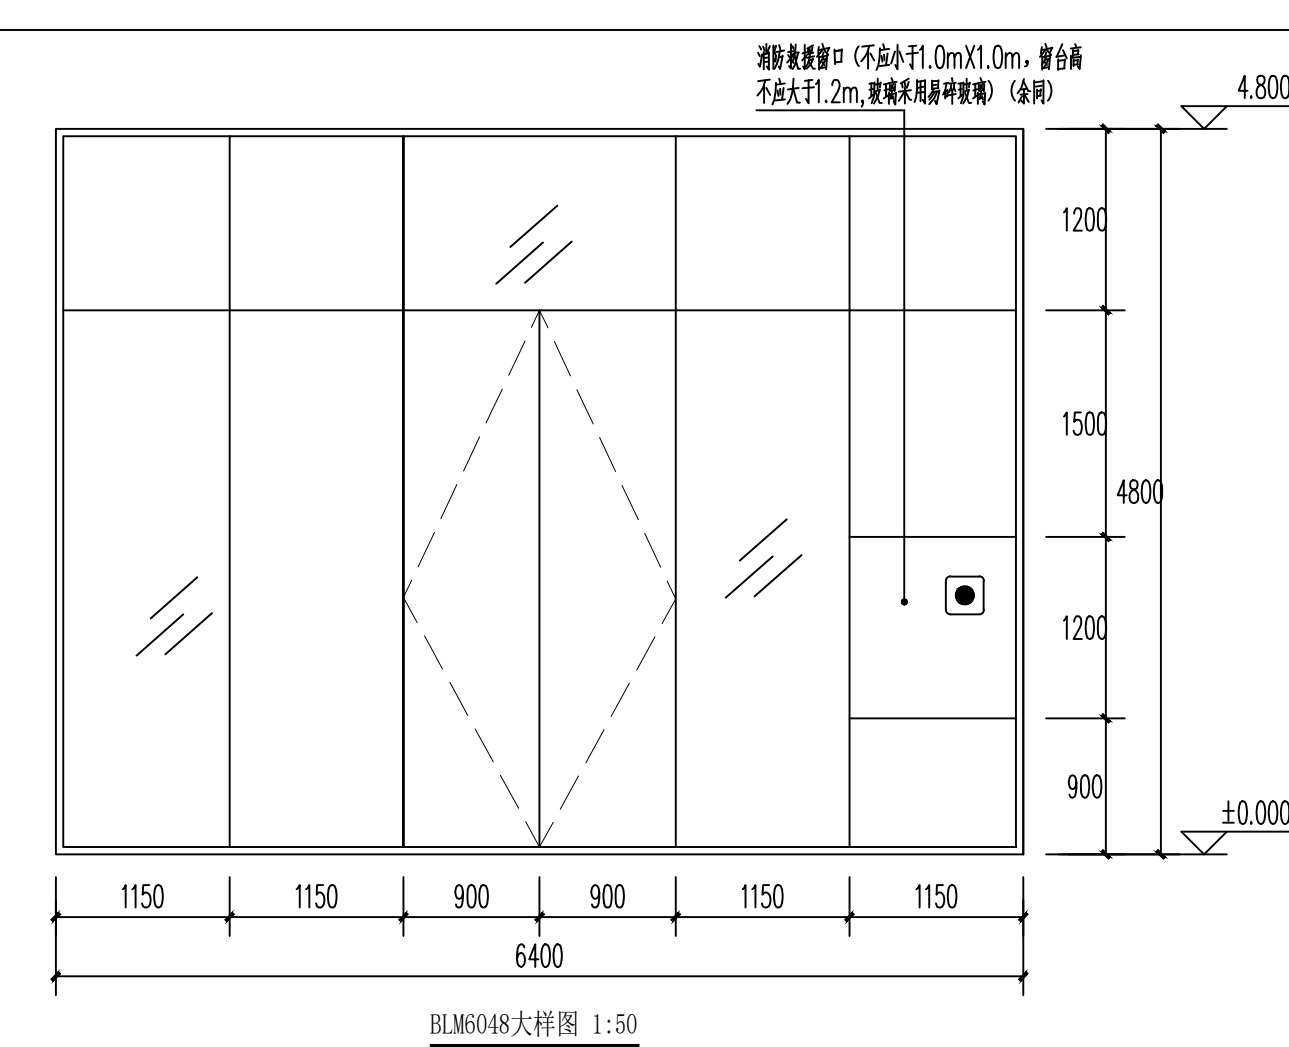
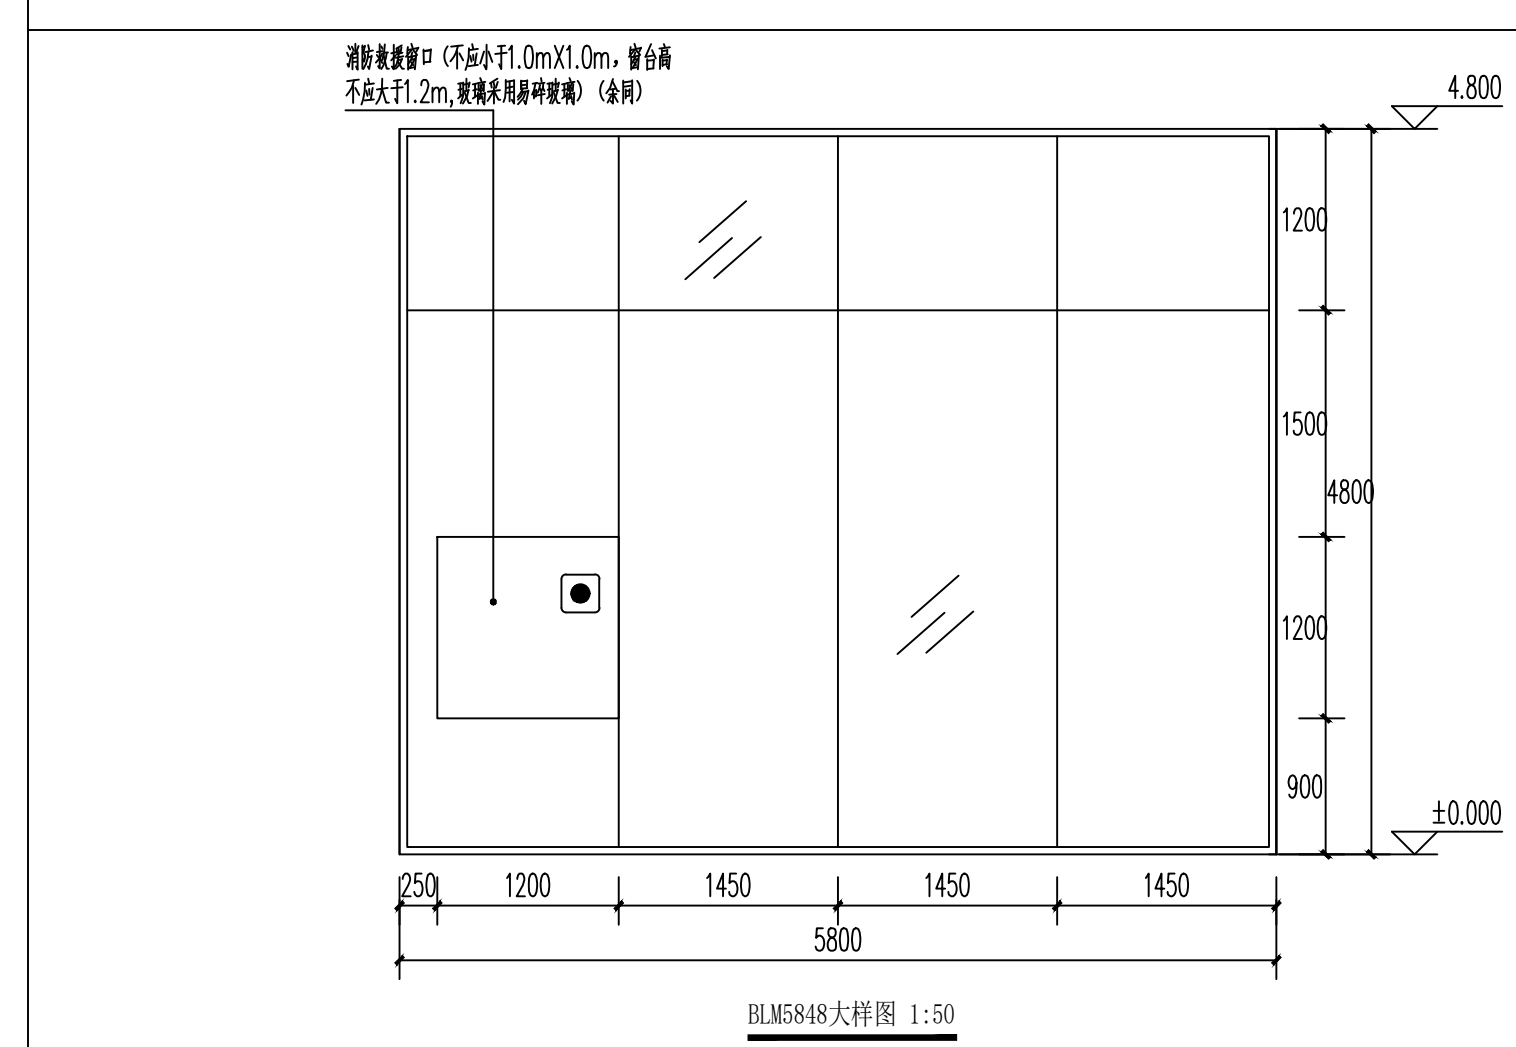
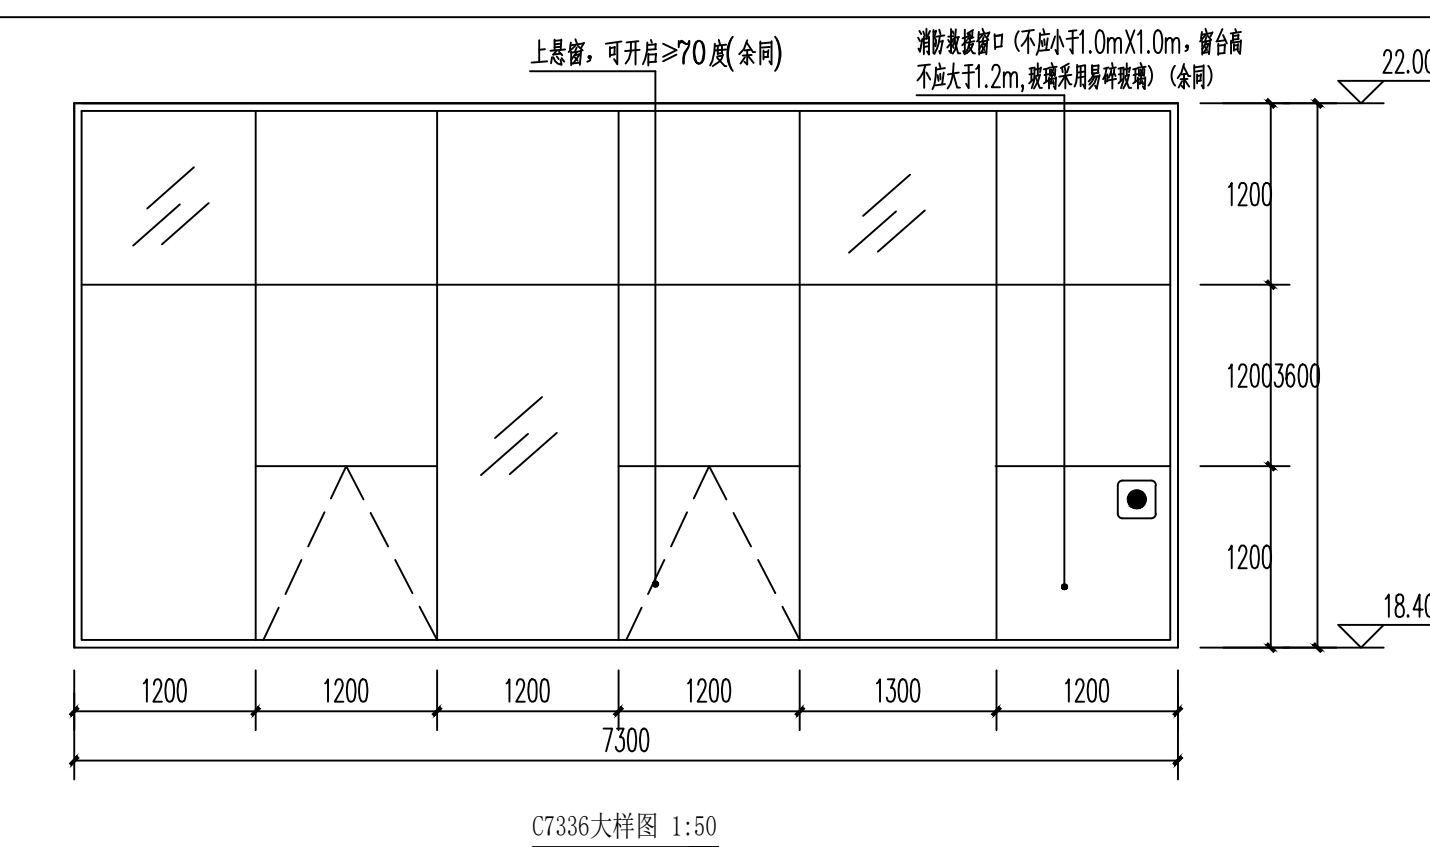
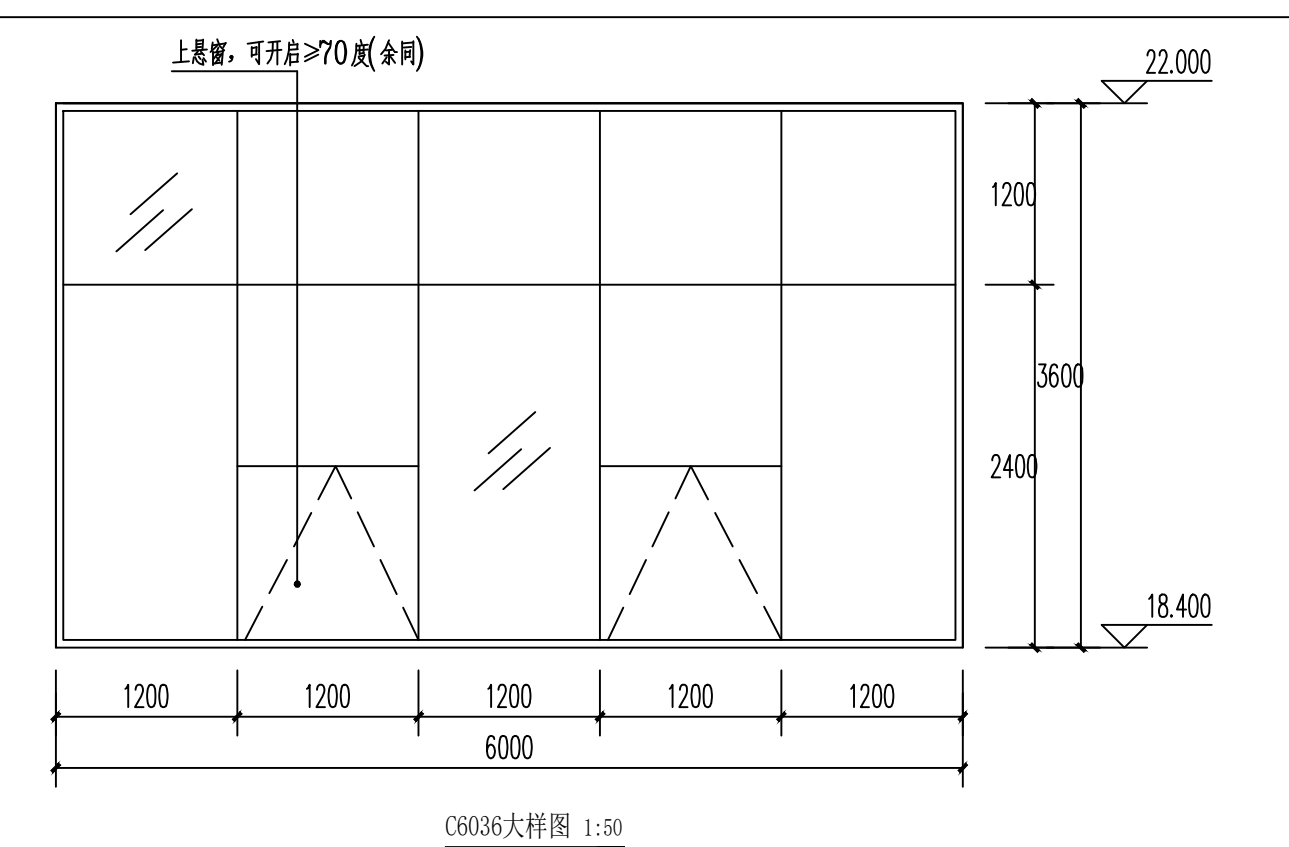
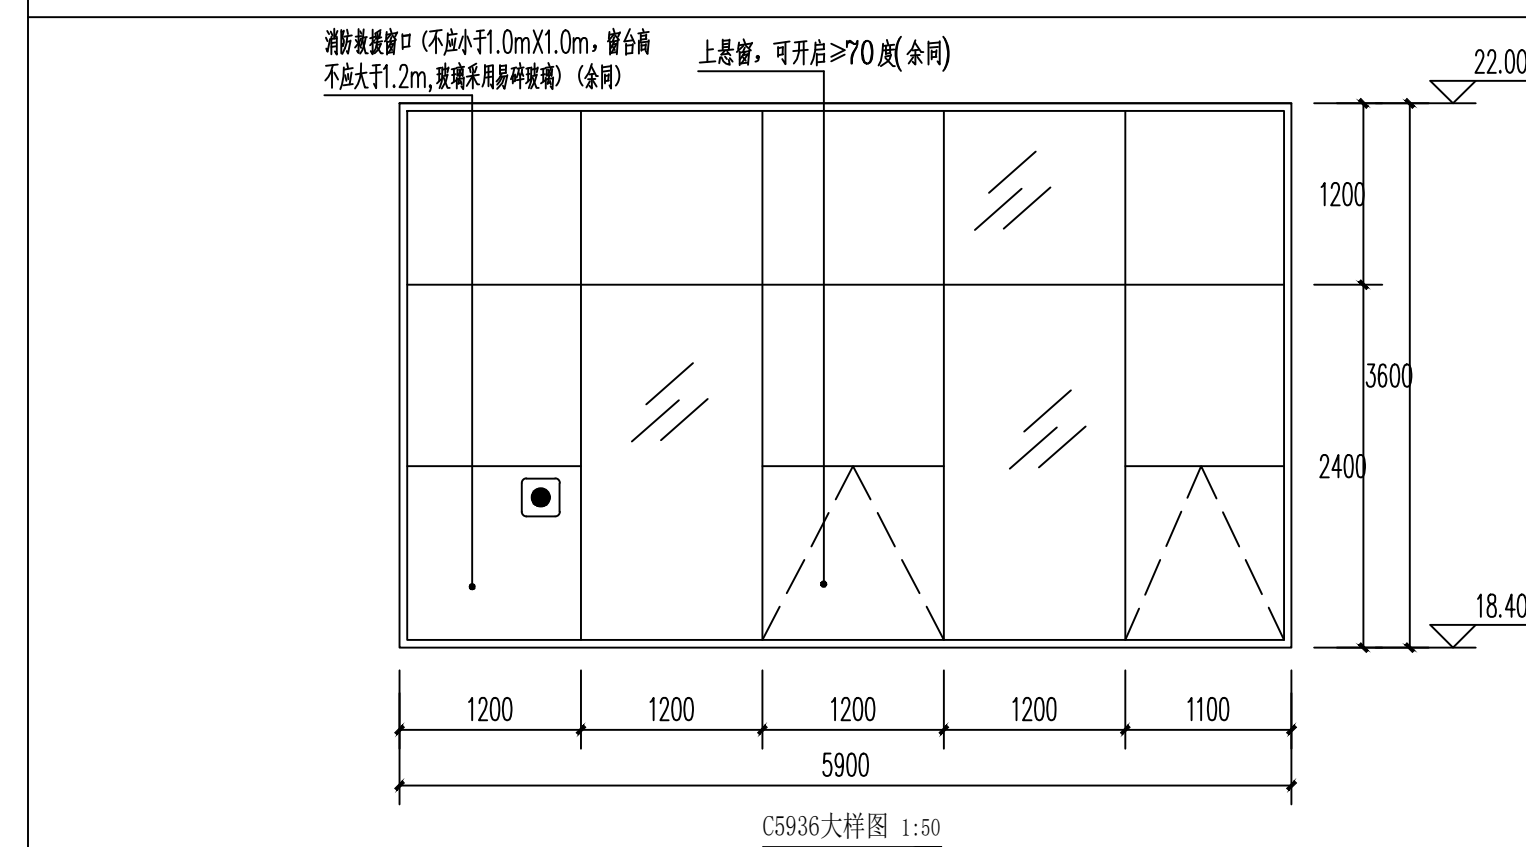
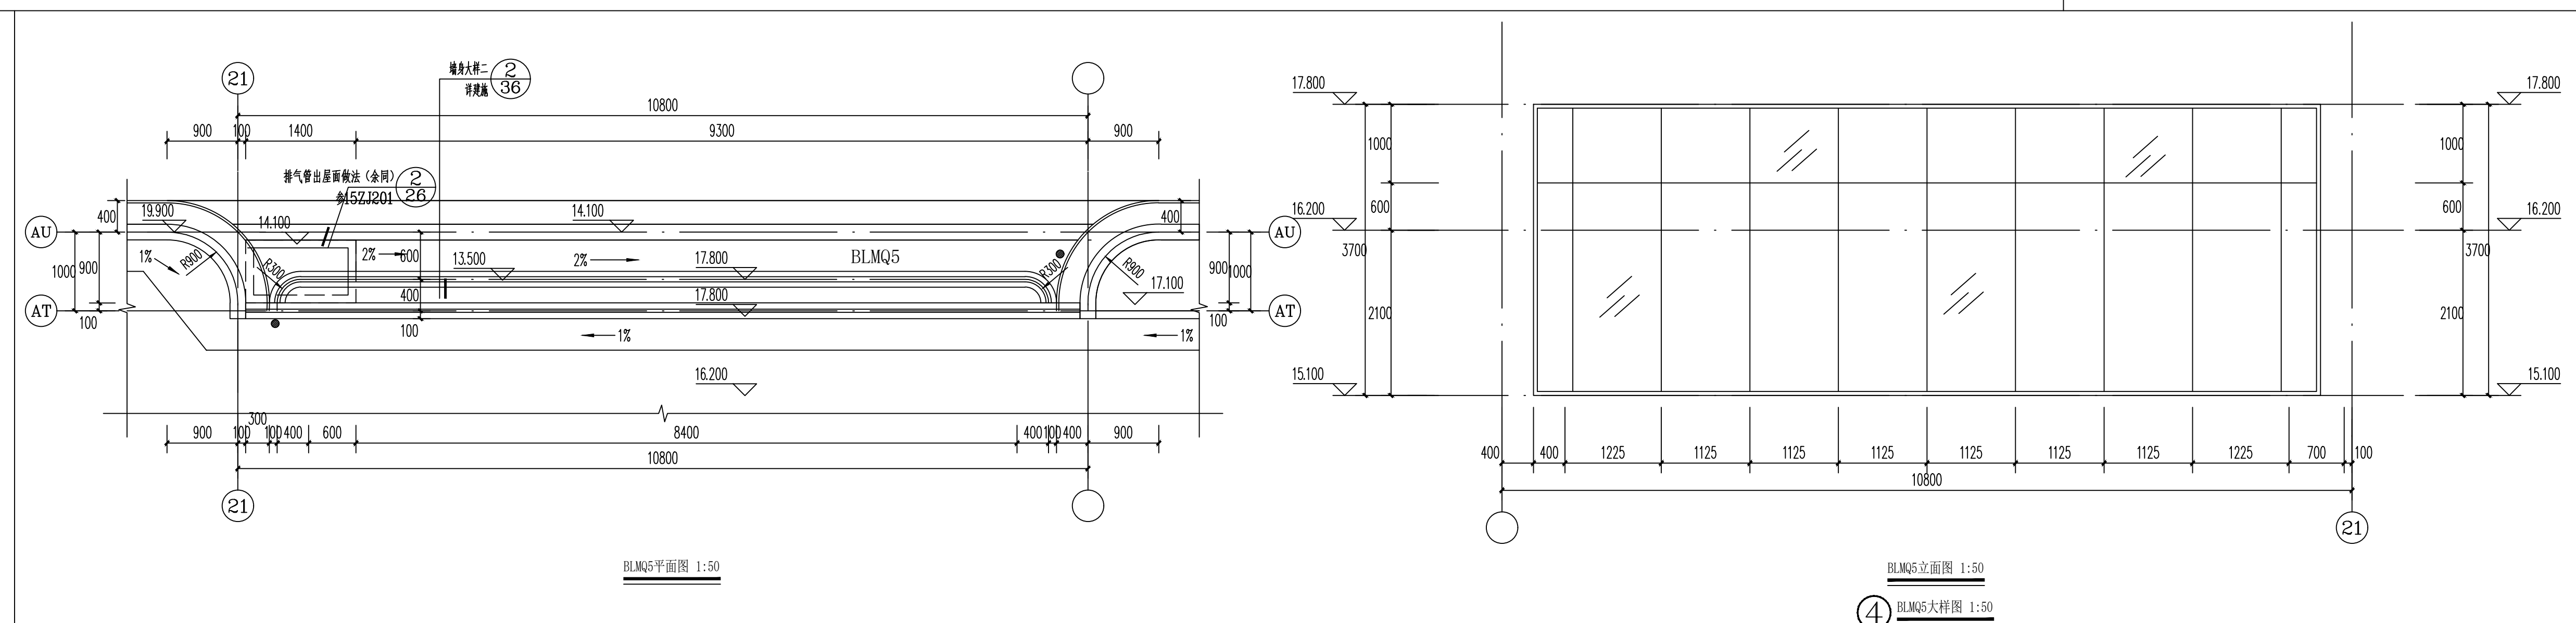
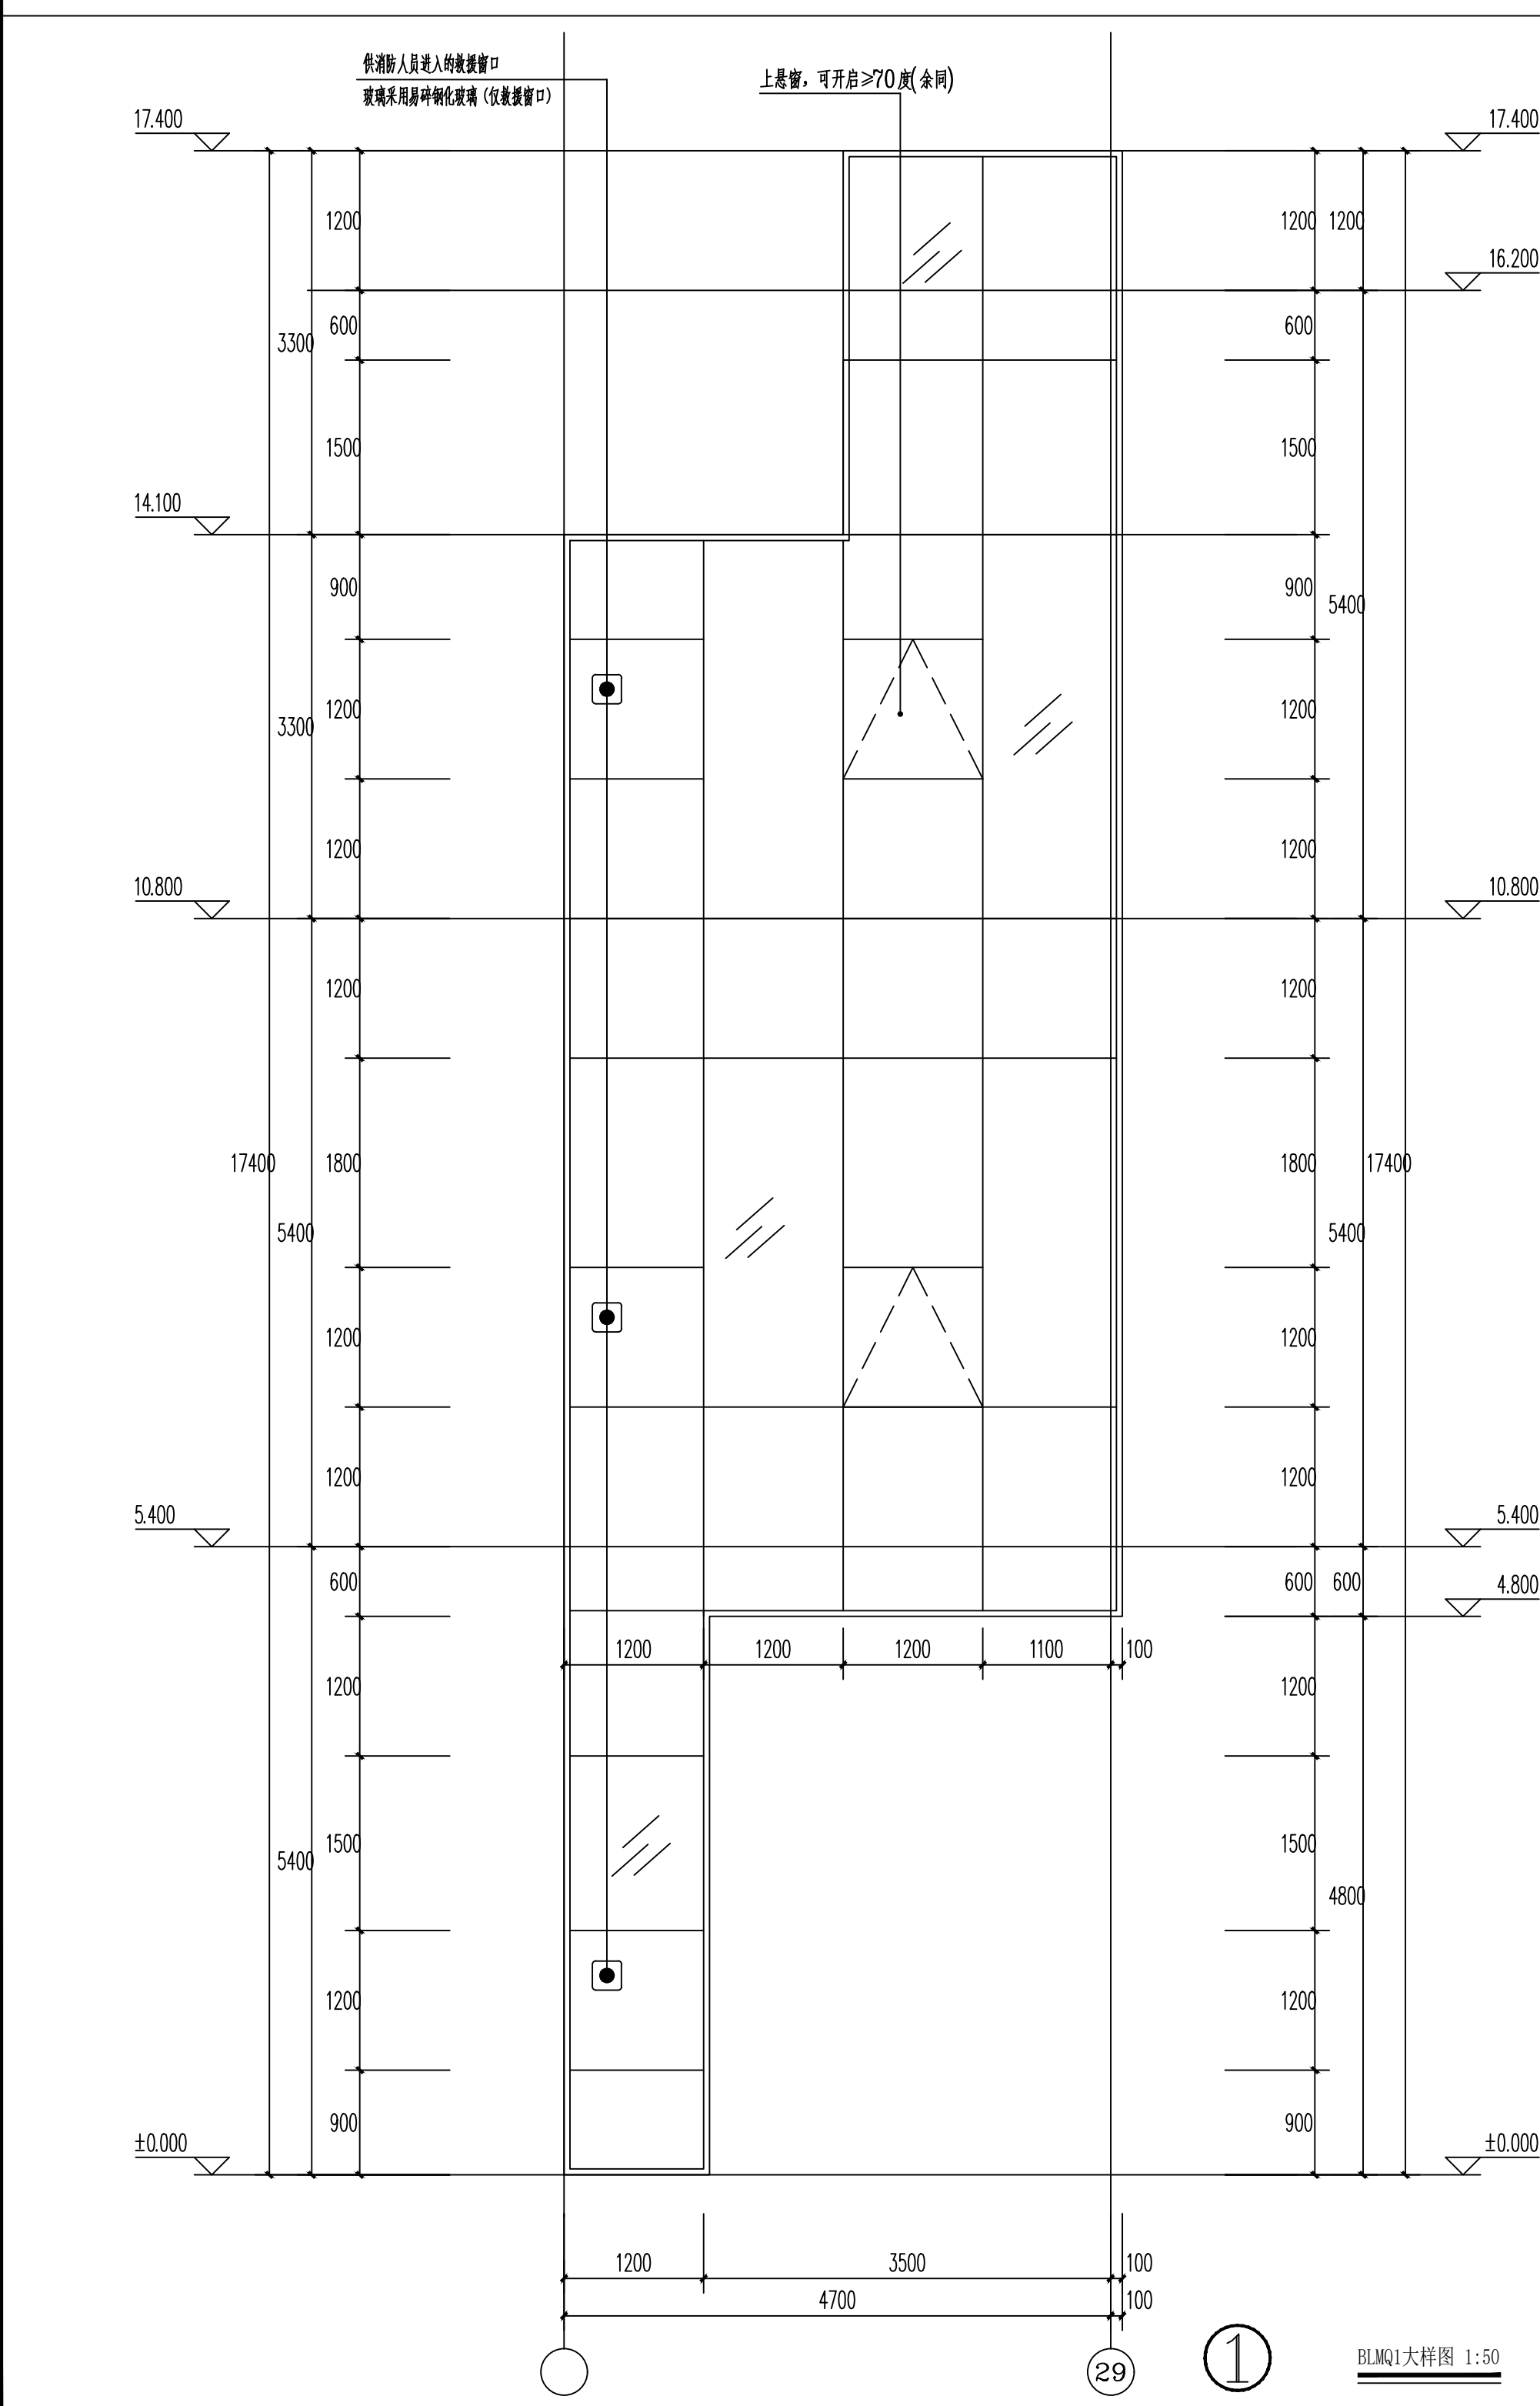
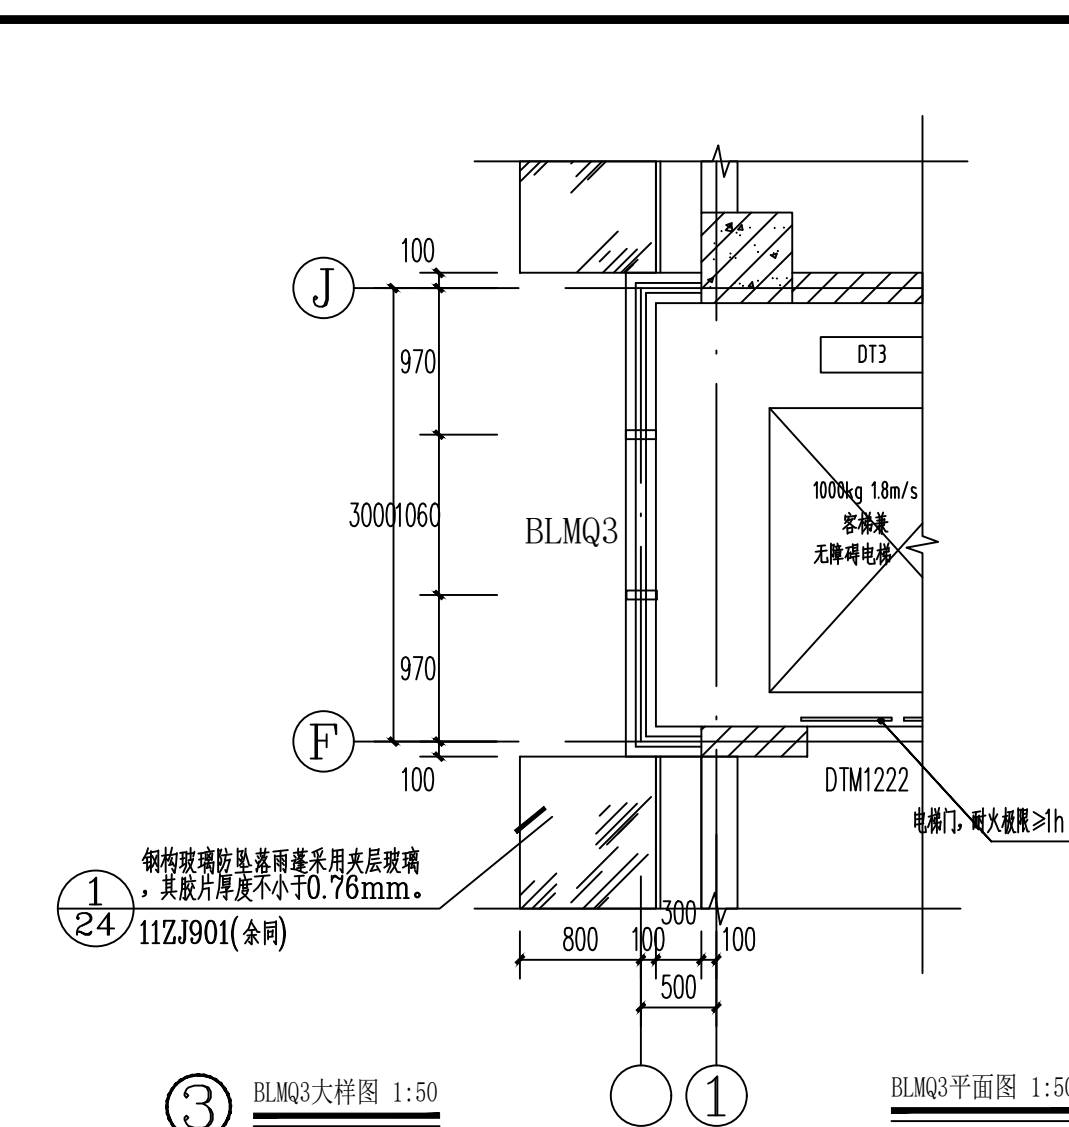


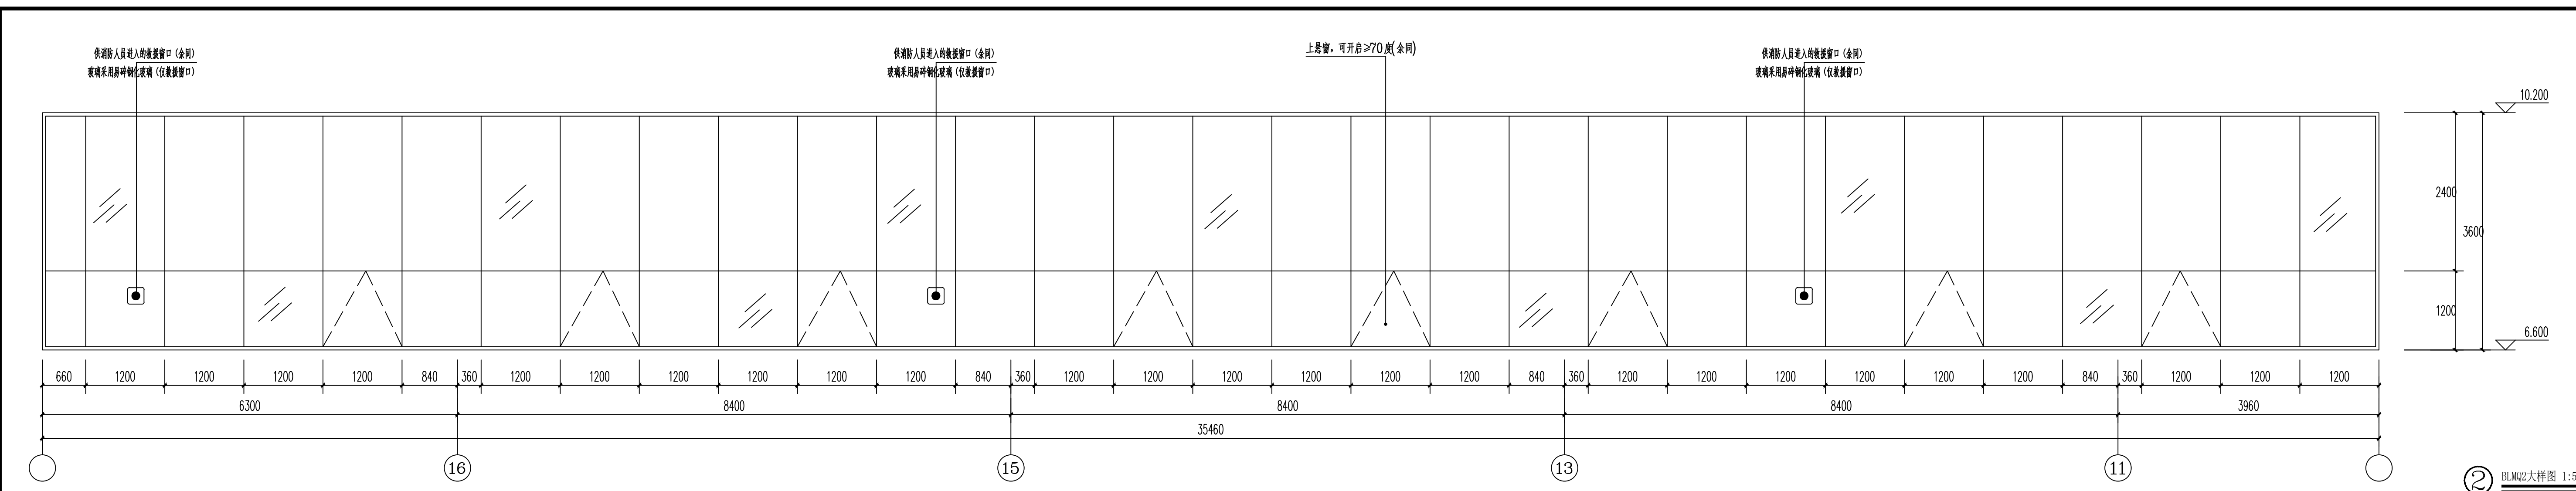

建设单位/CLIENT:

麻阳苗族自治县远桥房地产开发有限公司


项目名称/PROJECT:

远程国际

子项目名称/SUB-PROJECT:

远程国际

区位图/REGIONAL LOCATION MAP :

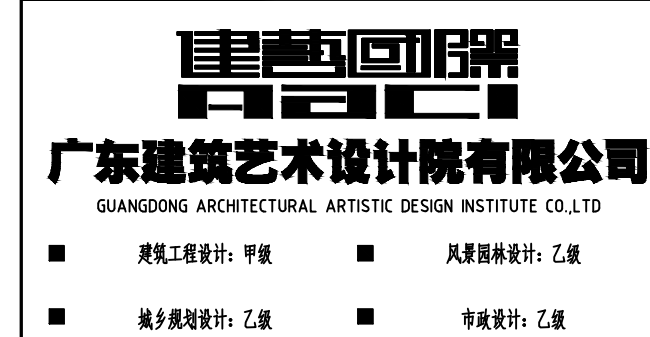

图纸名称/TITLE:

玻璃幕墙大样图一

项目名称/PROJECT:

远程国际

设计 DESIGNED	古新辉	
校对 CHECKED	吴新红	
专业负责人 CHIEF	吴志刚	
项目负责人 PROJECT CHIEF	吴志刚	
审核 IDENTIFIED	黄履优	
审定 APPROVED	李 坚	

校对 CHECKED	吴新红	吴新红
---------------	-----	-----

专业负责人	早主刚	早主刚
-------	-----	-----

CHIEF	吴冠中	吴冠中
项目负责人	吴冠中	吴冠中

项目负责人 PROJECT CHIEF	吴志刚	吴志刚
------------------------	-----	-----

审核	黄履优	
IDENTIFIED		

业务号/JOB NO.

设计阶段/STATUS: 施工图

专业/DISCIPLINE: 建施

比例/	1:100	规格/	A1
-----	-------	-----	----

SCALE:	1: ---	SIZE:	---

出图日期/DATE: 2021.06

图号/DRAWING NO. JS-43

版次	修改内容	日期
----	------	----

条形码/BARCODE:

版权所有，不得复制、套用。
ALL RIGHTS RESERVED, DON'T COPIED, REPRODUCED.